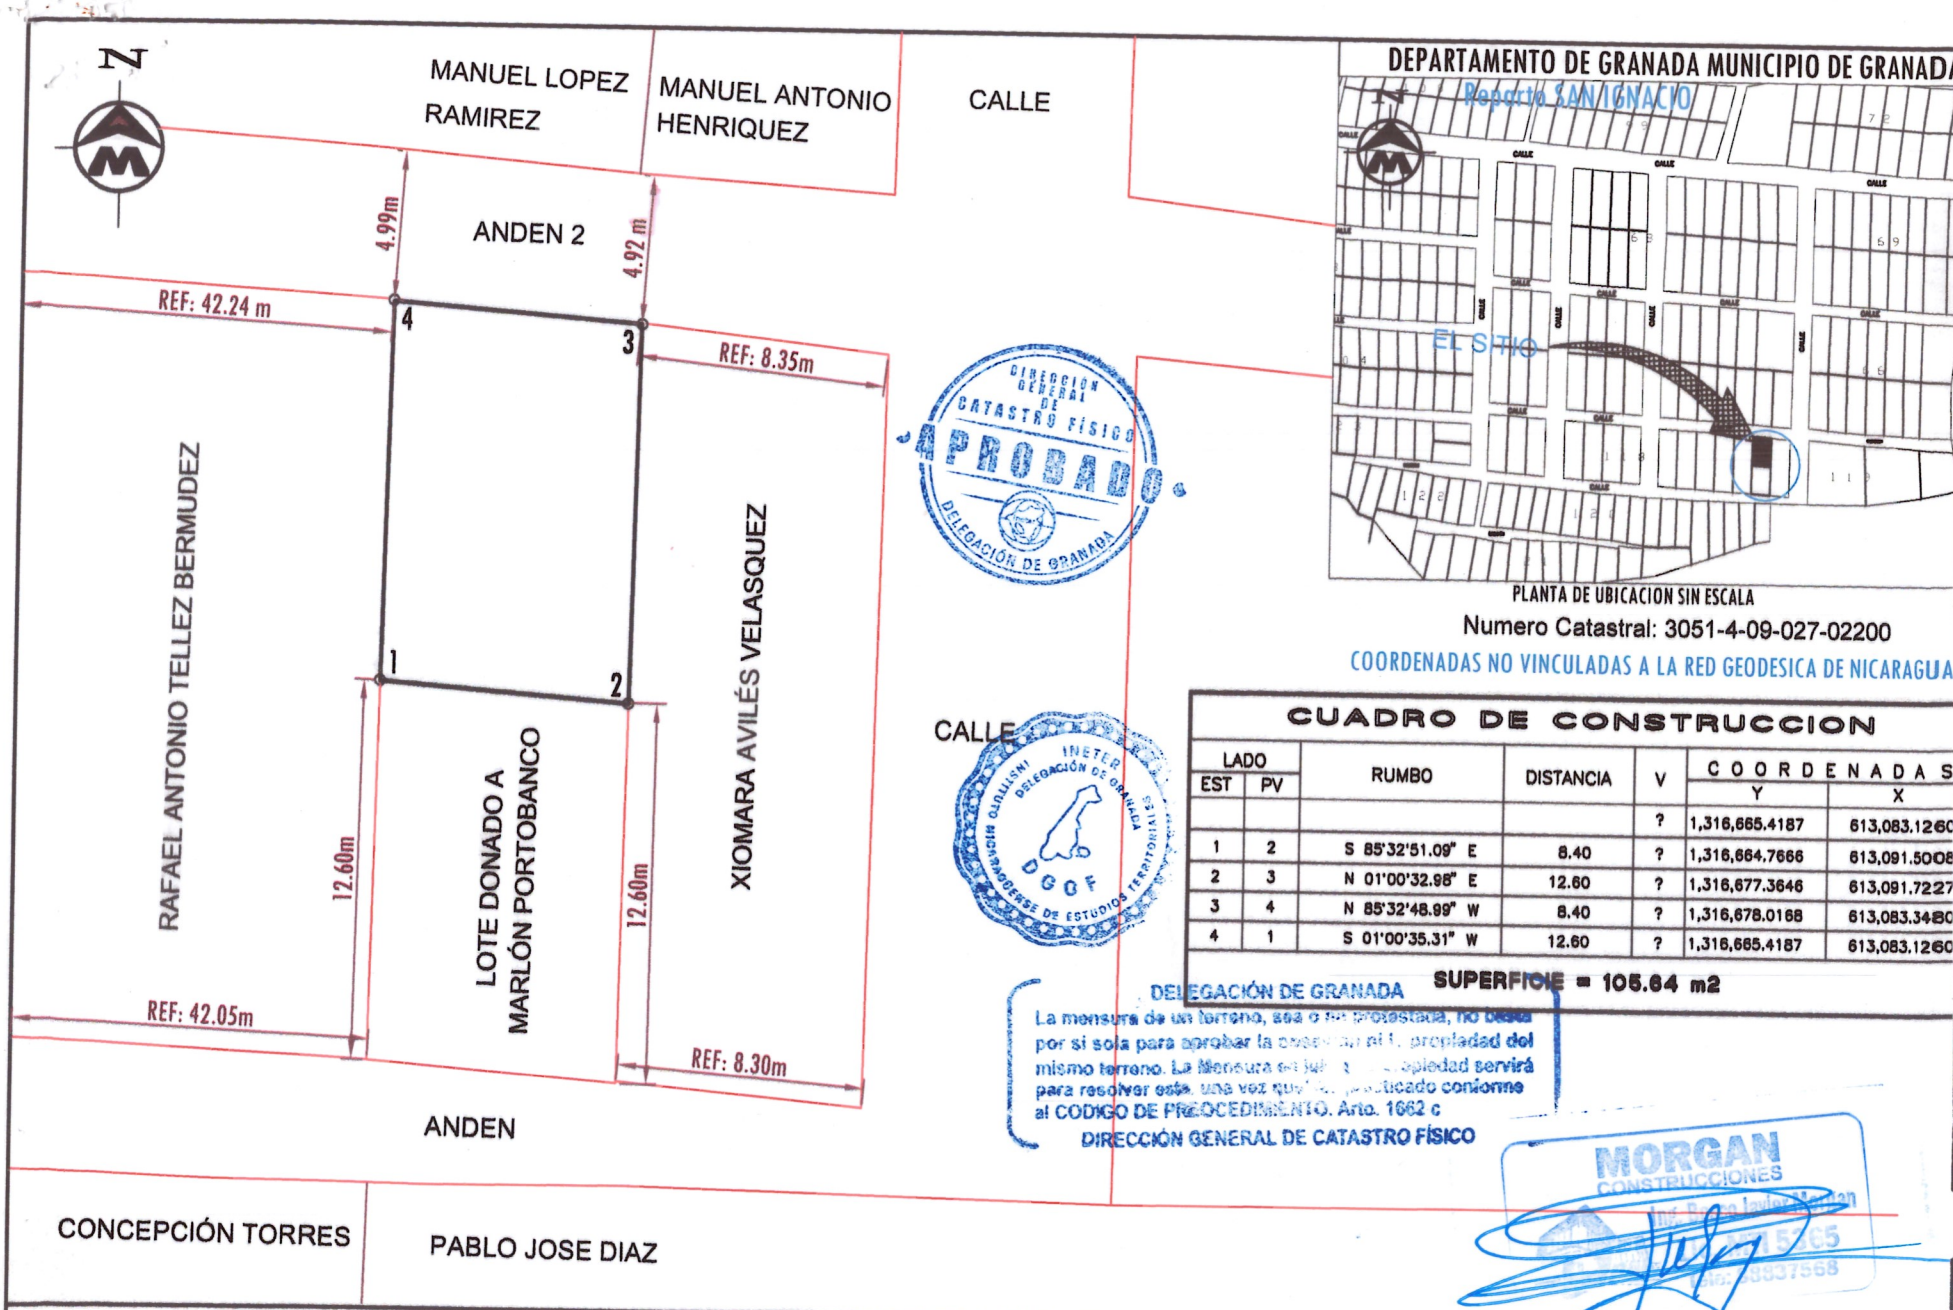

DEPARTAMENTO DE GRANADA MUNICIPIO DE GRANADA

PLANTA DE UBICACION SIN ESCALA

Numero Catastral: 3051-4-09-027-02200

COORDENADAS NO VINCULADAS A LA RED GEODESICA DE NICARAGUA

CUADRO DE CONSTRUCCION

LADO EST	LADO PV	RUMBO	DISTANCIA	V	COORDENADAS Y	COORDENADAS X
				?	1,316,665.4187	613,083.1260
1	2	S 85°32'51.09" E	8.40	?	1,316,664.7666	613,091.5008
2	3	N 01°00'32.98" E	12.60	?	1,316,677.3646	613,091.7227
3	4	N 85°32'48.99" W	8.40	?	1,316,678.0168	613,083.3480
4	1	S 01°00'35.31" W	12.60	?	1,316,665.4187	613,083.1260

SUPERFICIE = 105.64 m2

Transacción	T-3ZUN3J-001	Cudoc	0022178	Objeto Plano	TRASPASO TOTAL
Parcela Objeto	63113606860721-2	Área (m²)	105.65	Documento	W8BRTSI
No. Licencia:	BMM100426	Fecha Aprobación:	27/3/2024	Fecha Vencimiento:	27/3/2025 11:48:20

Objeto Lev: Donación de su Resto Indiviso	Numero Catastral: 3051-4-09-027-02200	FIRMA:	
Enajenante: Javier Arcángel Portobanco Martínez conocido como Javier Portobanco Martínez cédula: 201-230865-0003X	Ubicacion: Reparto San Ignacio del Centro de salud 2c al Oeste 2c al Sur Municipio de Granada. Dpto Granada.	Ejecuta: Ing.Bosco Javier Morgan Lic. Catastral: BMM100426 Cel: 8883-7568 Email: ingmorgan73@gmail.com www.morganconstrucciones.com	
Adquiriente: Johona del Carmen Corea Rodriguez cedula:201-070384-0007G	AREA= 105.64m² =149.854vrs2 vrs²	Escala: 1 /250	Fecha: 03 de Marzo del 2024

HOJA DE CALCULO

Ubicación: REPARTO SAN IGNACIO DEL CENTRO DE SALUD 4C AL OESTE 2C AL SUR. GRANADA Dueño: JAVIER ARCANGEL PORTOBANCO MARTINEZ Fecha: domingo, 03 marzo 2024

LADO	ANGULO	DIST.	RUMBO	LAT.	LONG.	LATC.	LONGC.	COORD X	COORD Y	X1 x Y2	Y1 x X2
1	184°27'08"	8.40	S85°32'52"E	-0.6521	8.3748	-0.6521	8.3748	1316665.4187	613083.1260	807236377602.2430	807224951001.1880
2	86°33'25"	12.60	N01°00'33"E	12.5980	0.2219	12.5980	0.2219	1316664.7666	613091.5008	807236269973.1880	807243701532.0030
3	93°26'38"	8.40	N85°32'49"W	0.6522	-8.3747	0.6522	-8.3747	1316677.3646	613091.7227	807232966924.7850	807244393561.1320
4	86°33'23"	12.60	S01°00'34"W	-12.5981	-0.2220	-12.5981	-0.2220	1316678.0168	613083.3480	807233074475.2250	807225643092.4180
5	88°59'26"	0.00	N90°00'00"E	0.0000	0.0000	0.0000	0.0000	1316665.4187	613083.1260	807225350792.6950	807225350792.6950
	540°00'00"	42.00		0.0000	0.0000	Error = 0.00					

Prec.= 1/10000 Área mts² = 105.6497 Área Mz: 0.0150 = 149.8551 Vrs²

MORGAN
CONSTRUCCIONES
Ing. Bosco Javier Morgan
Lic. MTI 5365
Tele: 88937568