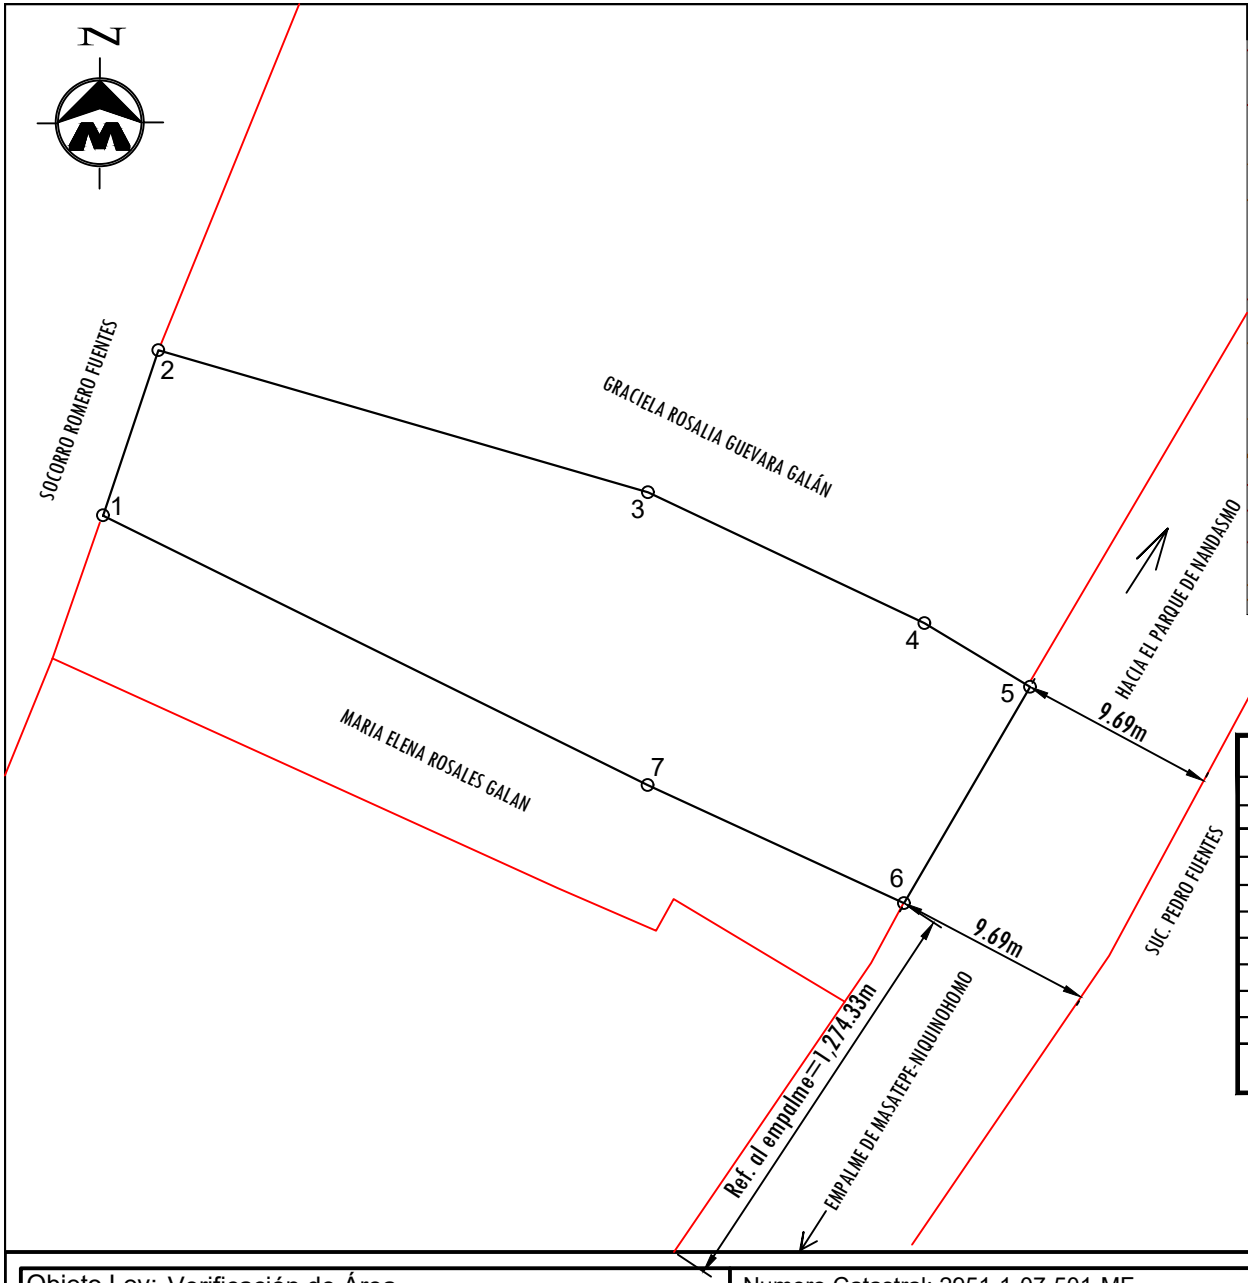

DEPARTAMENTO DE MASAYA MUNICIPIO DE NANDASMO

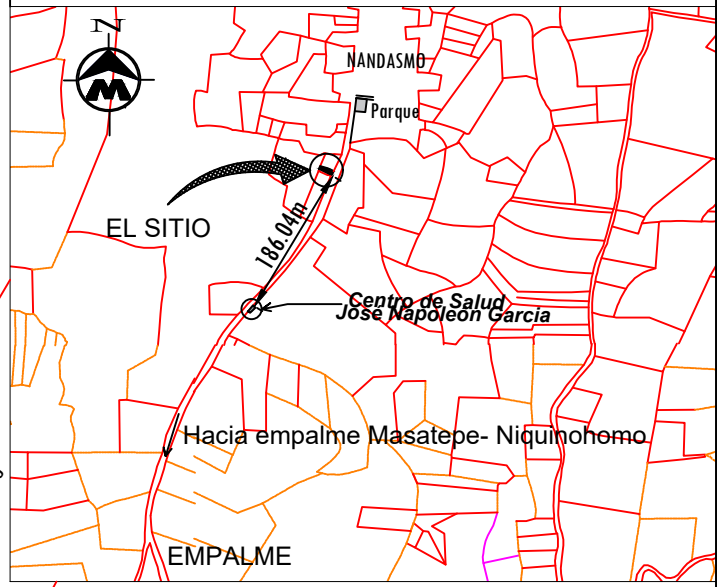

PLANTA DE UBICACION SIN ESCALA

Numero Catastral: 2951-1-07-501-MF

COORDENADAS NO VINCULADAS A LA RED GEODÉSICA DE NICARAGUA

CUADRO DE CONSTRUCCION

LADO EST	LADO PV	RUMBO	DISTANCIA	V	COORDENADAS Y	COORDENADAS X
				1	1,318,079.3870	595,630.4950
1	2	N 18°28'22.93" E	7.14	2	1,318,086.1550	595,632.7560
2	3	S 73°48'52.02" E	20.88	3	1,318,080.3360	595,652.8040
3	4	S 64°40'43.85" E	12.53	4	1,318,074.9790	595,664.1260
4	5	S 58°51'46.26" E	5.04	5	1,318,072.3710	595,668.4430
5	6	S 30°12'56.83" W	10.25	6	1,318,063.5160	595,663.2860
6	7	N 65°15'56.69" W	11.55	7	1,318,068.3480	595,652.7970
7	1	N 63°39'56.16" W	24.88	1	1,318,079.3870	595,630.4950

SUPERFICIE = 364.00 m2

Objeto Lev: Verificación de Área	Numero Catastral: 2951-1-07-501-MF	FIRMA:
Propietaria: Maria Elena Rosales Galan cédula: 407-180253-0000S	Ubicacion: Del Centro de Salud Jose Napoleon Garcia 186.04m al Noreste. Municipio de Nandasmo. Departamento de Masaya	Ejecuta: Ing.Bosco Javier Morgan Lic. Catastral: BMM100426 Cel: 8883-7568 Email: ingmorgan73@gmail.com www.morganconstrucciones.com
DATOS REGISTRALES: Finca:278 Tomo:667 Folio: 35 Asiento: 4	ÁREA= 364.00 m² = 516.31 vrs² — Escala: 1 /300	Fecha: 05 de Abril del 2024