


## DEPARTAMENTO DE GRANADA MUNICIPIO DE GRANADA

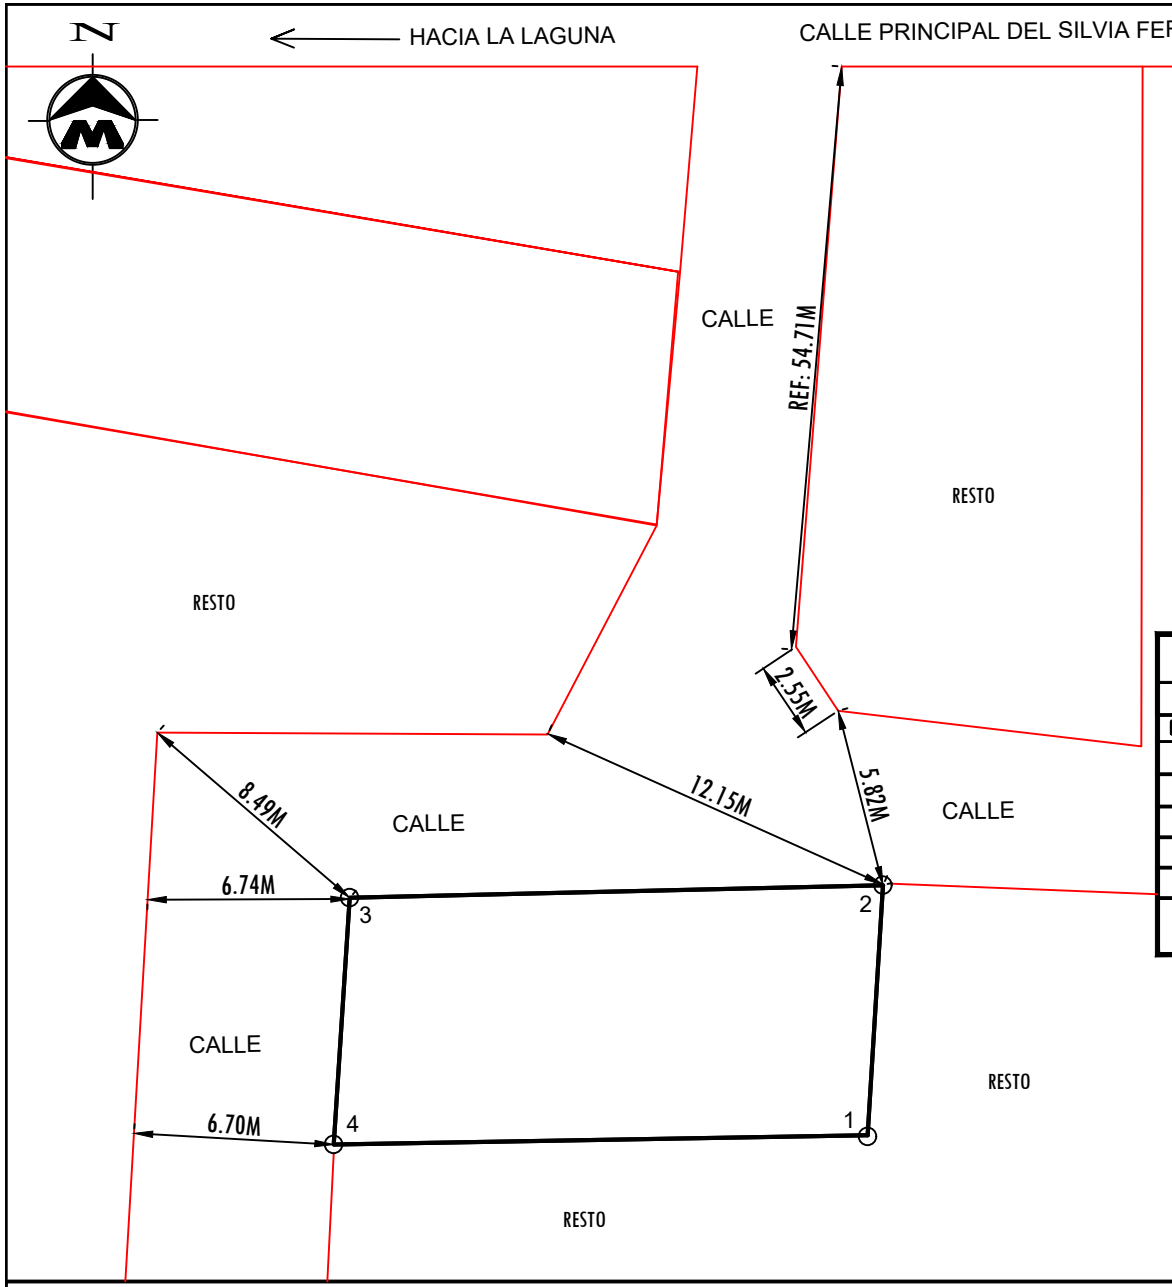


PLANTA DE UBICACION SIN ESCALA

Numero Catastral: 3051-4-05-000-08620

COORDENADAS NO VINCULADAS AL SISTEMA NACIONAL DE COORDENADAS

## CUADRO DE CONSTRUCCION
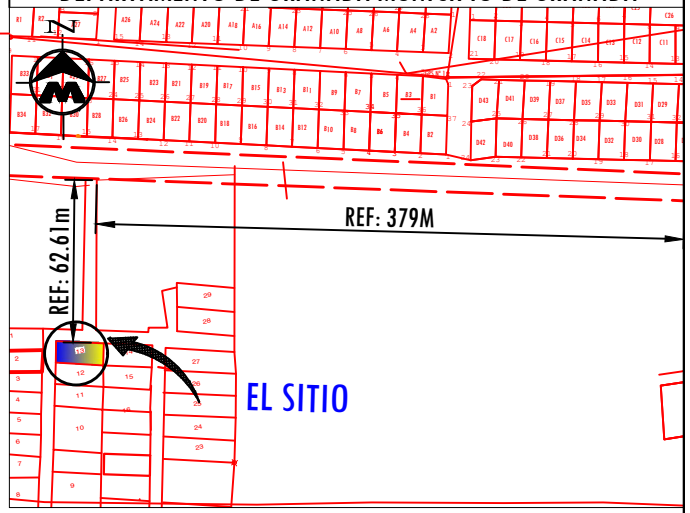
| LADO EST | LADO PV | RUMBO | DISTANCIA | V | COORDENADAS Y | COORDENADAS X |
|---|---|---|---|---|---|---|
| | | | | 1 | 1,319,046.6300 | 611,622.4900 |
| 1 | 2 | N 03°30'12.71" E | 8.35 | 2 | 1,319,054.9600 | 611,623.0000 |
| 2 | 3 | S 88°38'43.03" W | 17.76 | 3 | 1,319,054.5400 | 611,605.2400 |
| 3 | 4 | S 03°45'30.80" W | 8.24 | 4 | 1,319,046.3200 | 611,604.7000 |
| 4 | 1 | N 89°00'06.09" E | 17.79 | 1 | 1,319,046.6300 | 611,622.4900 |

**SUPERFICIE = 146.89 m2**

| | | |
|---|---|---|
| Objeto Lev: Venta Parcial de una Parte Indivisa | Numero Catastral: 3051-4-05-000-08620 | FIRMA: |
| Enajenante: Augusto Cesar Marenco Balladares<br>Cédula: 201-151237-0005L | UBICACION:<br>De la primera entrada al Reparto Silvia Ferrufino 379m al Oeste, 62.61m al Sur. Municipio de Granada. Departamento de Granada. | Ejecuta: Ing.Bosco Javier Morgan<br>Lic. Catastral: BMM100426<br>Cel: 8883-7568 Email: ingmorgan73@gmail.com<br>www.morganconstrucciones.com |
| Adquirientes: Eduardo Sebastián Marquez Gómez adquiere (Nuda propiedad). Partida: 169 Tomo: 10067 Folio: 169 Maria Argentina Gomez Sandoval ced: 201-080886-0006E (Usufructo) y actúa en representación del menor. | ÁREA= 146.89m²= 208.36vrs2 — Escala: 1 /250 | Fecha: 01 de Agosto del 2024 |