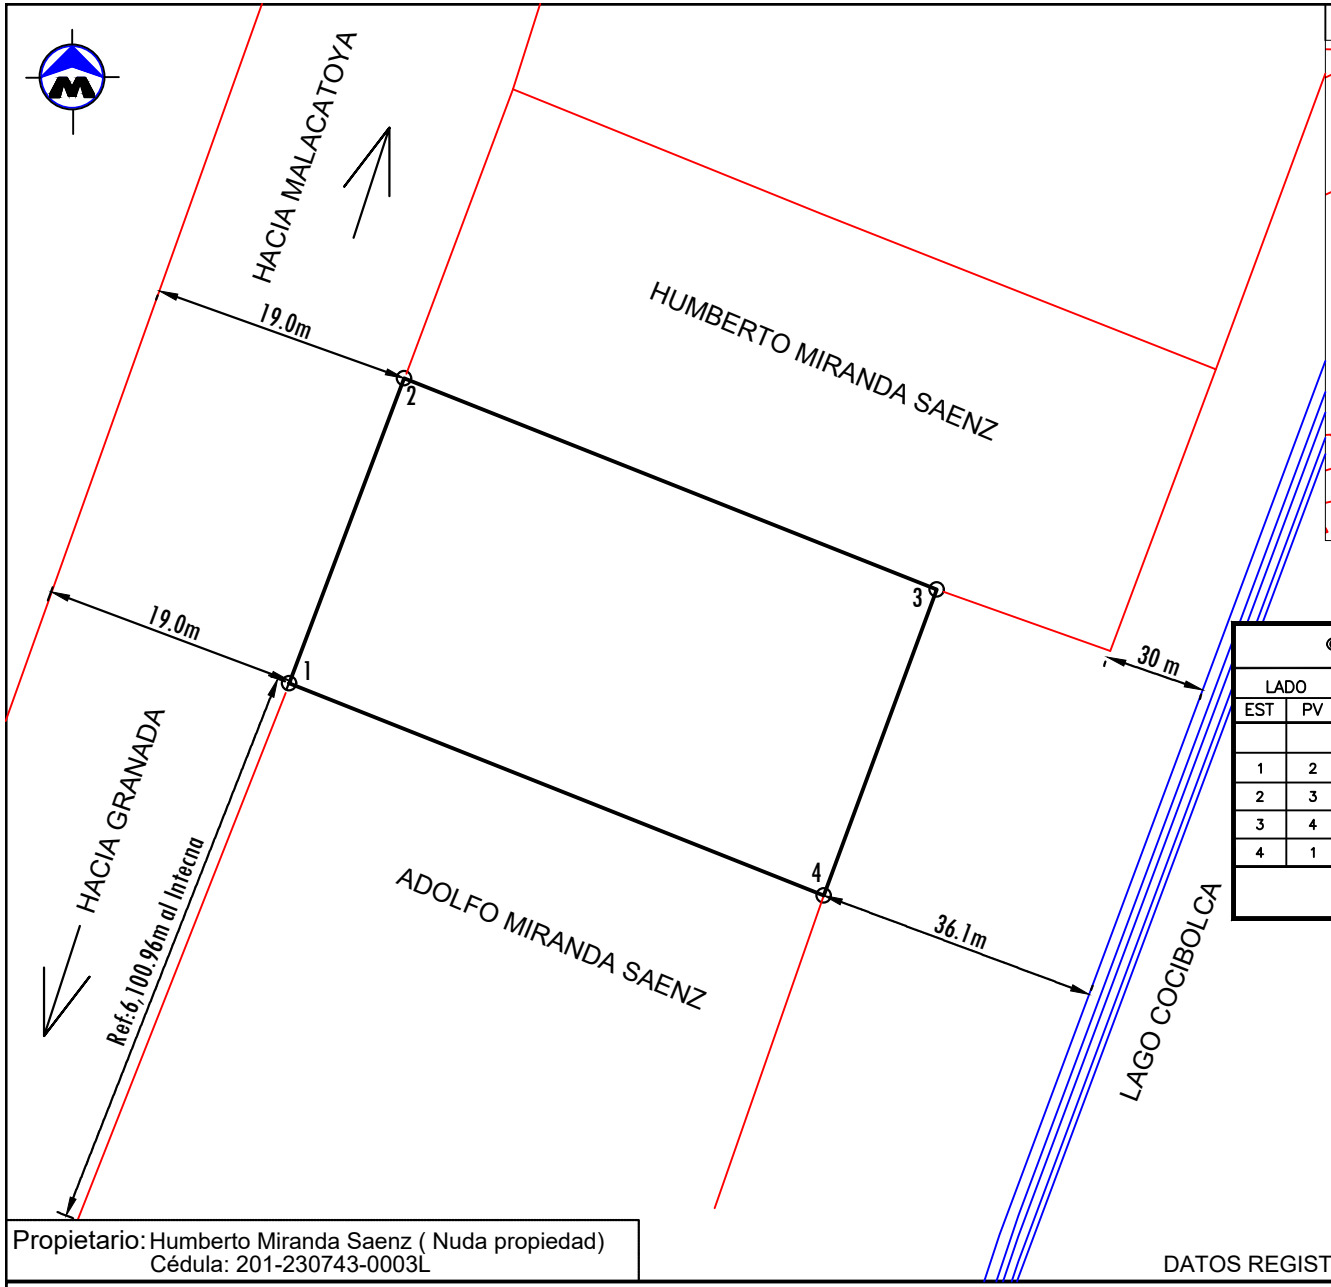

DEPARTAMENTO DE GRANADA MUNICIPIO DE GRANADA

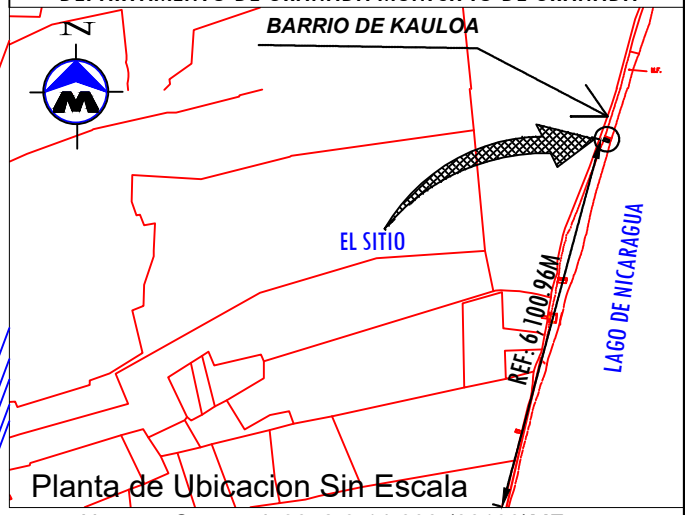

Planta de Ubicacion Sin Escala

Numero Catastral: 3052-3-14-000-(00100)MF

COORDENADAS NO VINCULADAS A LA RED GEODESICA DE NICARAGUA

CUADRO DE CONSTRUCCION

LADO EST	LADO PV	RUMBO	DISTANCIA	V	COORDENADAS Y	COORDENADAS X
				1	1,326,654.1200	615,838.1100
1	2	N 20°36'19.69" E	10.85	2	1,326,664.2800	615,841.9300
2	3	S 68°21'56.69" E	19.10	3	1,326,657.2400	615,859.6800
3	4	S 20°18'10.76" W	10.87	4	1,326,647.0500	615,855.9100
4	1	N 68°20'14.89" W	19.15	1	1,326,654.1200	615,838.1100

SUPERFICIE = 207.63 m2

Propietario: Humberto Miranda Saenz (Nuda propiedad)
Cédula: 201-230743-0003L

DATOS REGISTRALES FINCA: 32,180 TOMO: 498 FOLIO: 11-12 ASIENTO:1

Objeto Lev: Cancelación de Usufructo	Numero Catastral: 3052-3-14-000-(00100)MF	Fecha: 27 de agosto del 2024
Propietarios: Canuto Edmundo Miranda conocido registralmente como Edmundo Miranda Morales. (Usufructo) Defunción: Partida # 273, Tomo:0091, folio: 273 Ana Clemencia Saenz Vargas conocia registralmente como Anita Saenz de Miranda. (Usufructo) Defuncion: Partida # 051, Tomo:102, folio:051	Ubicacion: Del Instituto Pedro Arauz Palacios 6,100.96m al Noreste, Barrio de Kauloa, Lote A. Municipio de Granada. Depto de Granada.	Ejecuta: Ing..Bosco Javier Morgan Lic. Catastral: BMM100426 Cel: 8883-7568 Email: ingmorgan73@gmail.com www.morganconstrucciones.com
	Area: 207.63 m² = 294.50 vrs² — Escala: 1 / 250	FIRMA: