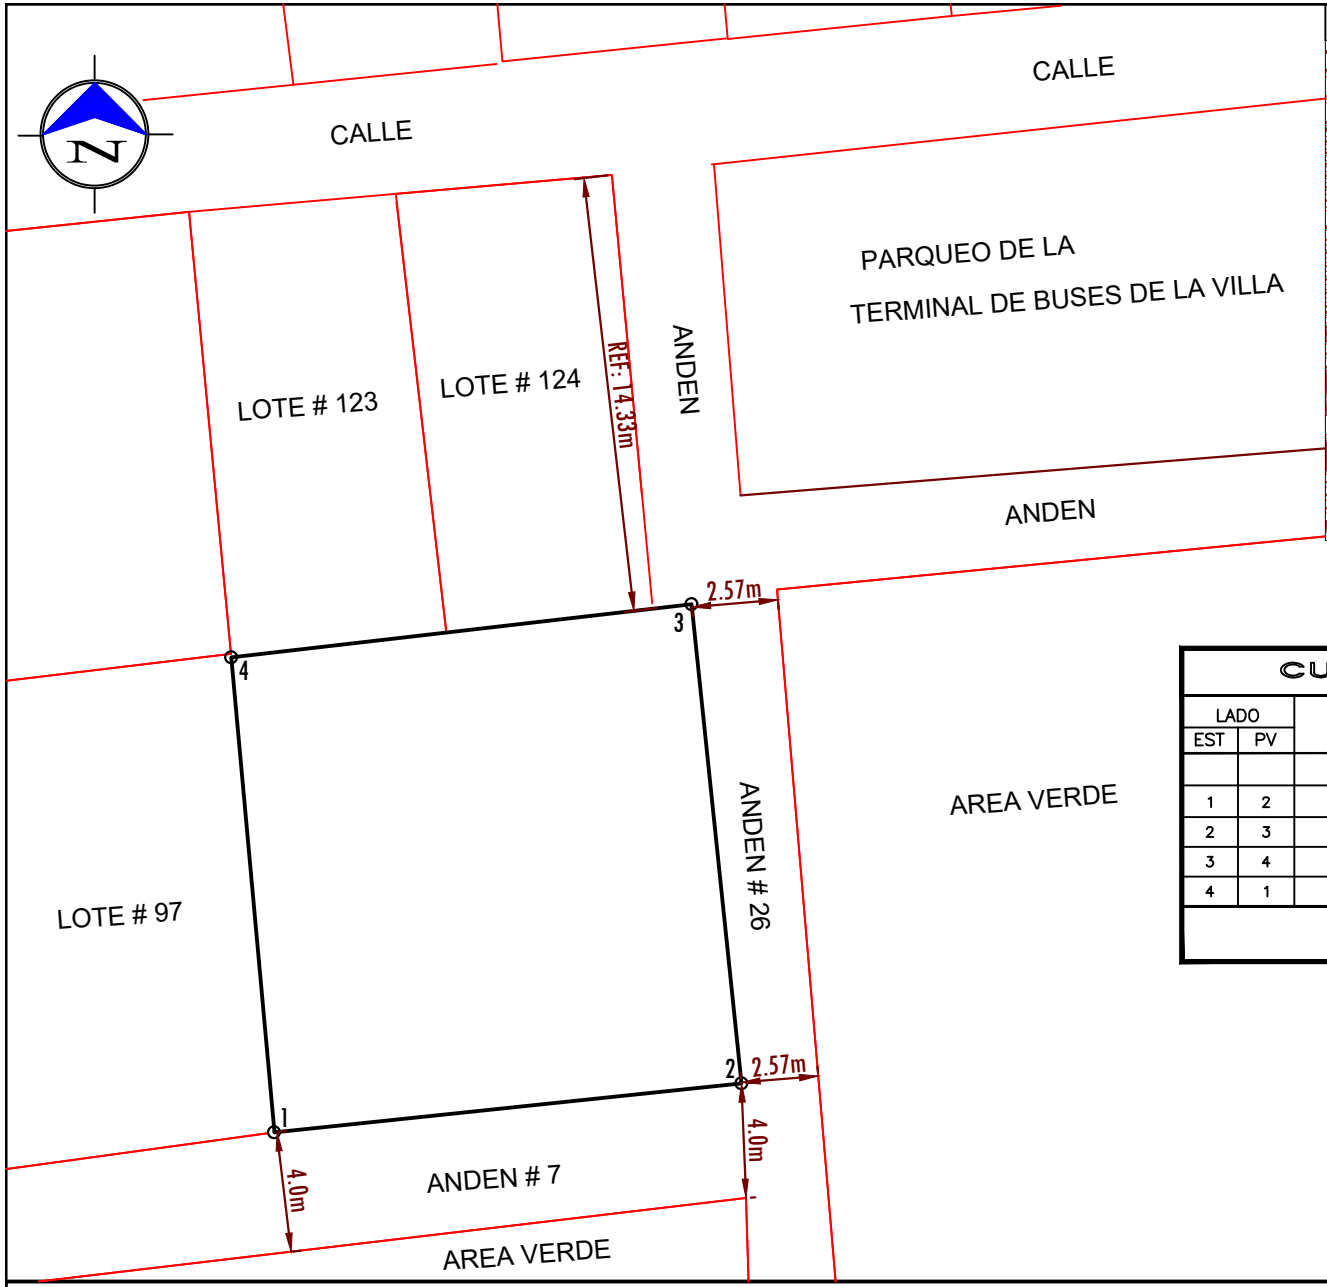

Numero Cat: 3051-4-05-039-18700

Planta de Ubicacion Sin Escala

COORDENADAS NO VINCULADAS A LA RED GEODESICA DE NICARAGUA

CUADRO DE CONSTRUCCION

LADO EST	LADO PV	RUMBO	DISTANCIA	V	COORDENADAS Y	COORDENADAS X
				1	1,320,681.6800	614,378.4500
1	2	N 83°58'59.98" E	15.65	2	1,320,683.3200	614,394.0100
2	3	N 05°56'16.74" W	16.05	3	1,320,699.2800	614,392.3500
3	4	S 83°25'05.00" W	15.44	4	1,320,697.5100	614,377.0100
4	1	S 05°11'51.69" E	15.90	1	1,320,681.6800	614,378.4500

SUPERFICIE = 248.22 m2

Objeto Lev: Compraventa - Total	Numero Cat: 3051-4-05-039-18700	FIRMA:
Enajenante: Julio Cesar Picasso Mora Ced: 201-141278-0007N Luis Alonzo Picasso Mora Ced: 201-030176-0003Y	Ubicacion: Villa Sandino, Grupo A lote # 95-96 ,del Benemérito Cuerpo de Bomberos de Villa Sandino, 61.85m al Oeste y 14.33 Sur Municipio de Granada, Departamento de Granada.	Ejecuta: Ing.Bosco Javier Morgan Lic. Catastral: BMM100426 Cel: 8883-7568 Email: ingmorgan73@gmail.com www.morganconstrucciones.com
Adquiriente: Fabiola del Socorro López Mora Cédula: 201-280885-0004B	Area:248.22 m2 = 352.07 vrs2 — Escala: 1/250	Fecha: 27 de agosto del 2024