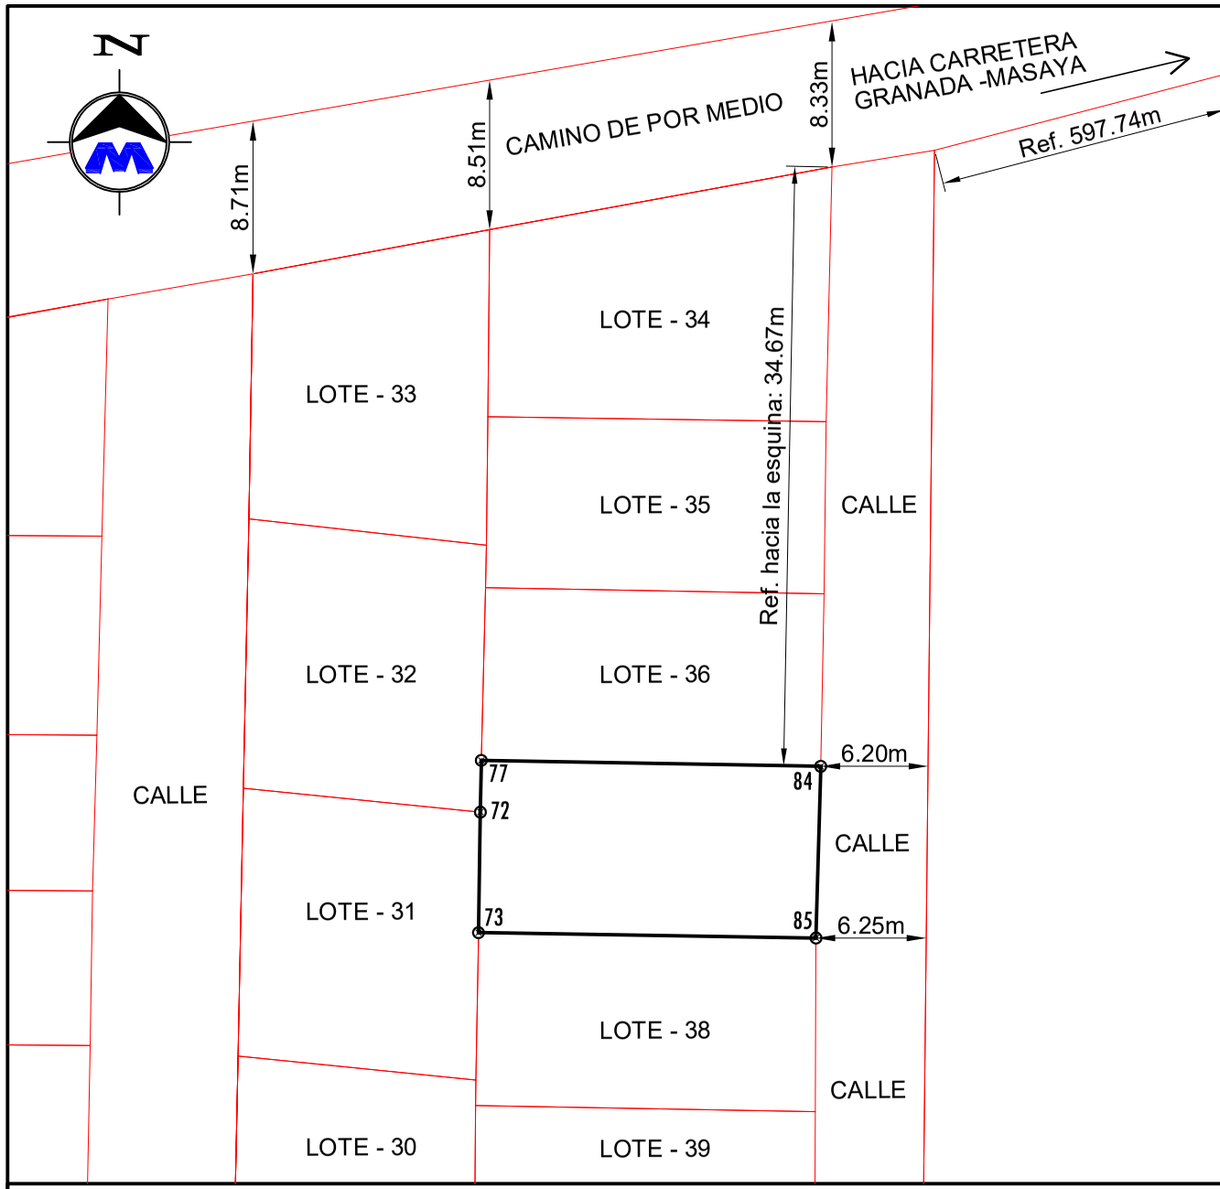

DEPARTAMENTO DE GRANADA MUNICIPIO DE GRANADA

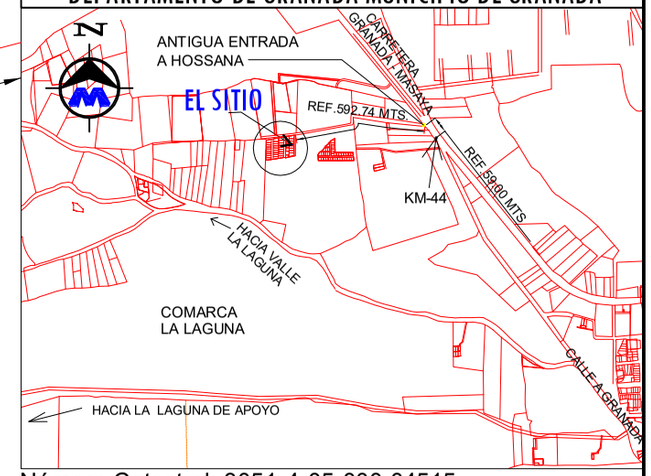

Número Catastral: 3051-4-05-000-04515
Planta de Ubicación Sin Escala

COORDENADAS NO VINCULADAS A LA RED GEODESICA DE NICARAGUA

CUADRO DE DERROTERO LOTE No.37

LADO EST	LADO PV	RUMBO	DIST.(M)	V	COORDENADAS Y	COORDENADAS X
				84	1,320,334.5513	610,634.2739
84	85	S 01°36'03.70" W	9.94	85	1,320,324.6168	610,633.9963
85	73	N 89°05'05.80" W	19.51	73	1,320,324.9284	610,614.4840
73	72	N 00°52'17.34" E	6.97	72	1,320,331.8988	610,614.5900
72	77	N 01°03'21.24" E	3.00	72	1,320,334.8939	610,614.6452
77	84	S 89°00'00.17" E	19.63	84	1,320,334.5513	610,634.2739

Área: 194.833 m2 = 276.354 vr2

Objeto Lev: Desmembración	Número Catastral: 3051-4-05-000-04515	FIRMA:
Enajenante: Francisco Javier Pedreira Pardo Cédula de Residencia: 22012008016	Ubicacion: De Km 44 Carretera Granada-Masaya, 59m al Noroeste, 592.74 m al Oeste y 34.67 m al Sur. Lote - 37. Cmca La Laguna. Municipio y Dpto. de Granada.	Ejecuta: Ing.Bosco Javier Morgan Lic. Catastral: BMM100426 Cel: 8883-7568 Email: ingmorgan73@gmail.com servicios topográficos
Adquiriente: Mery Ines Correa Masis Ced. Identidad: 201-040192-0009V	Área = 194.833 m2 = 276.354 vr2 — Escala: 1 / 250	Fecha: 29 de Mayo 2025

ESPACIO PARA ESQUELA