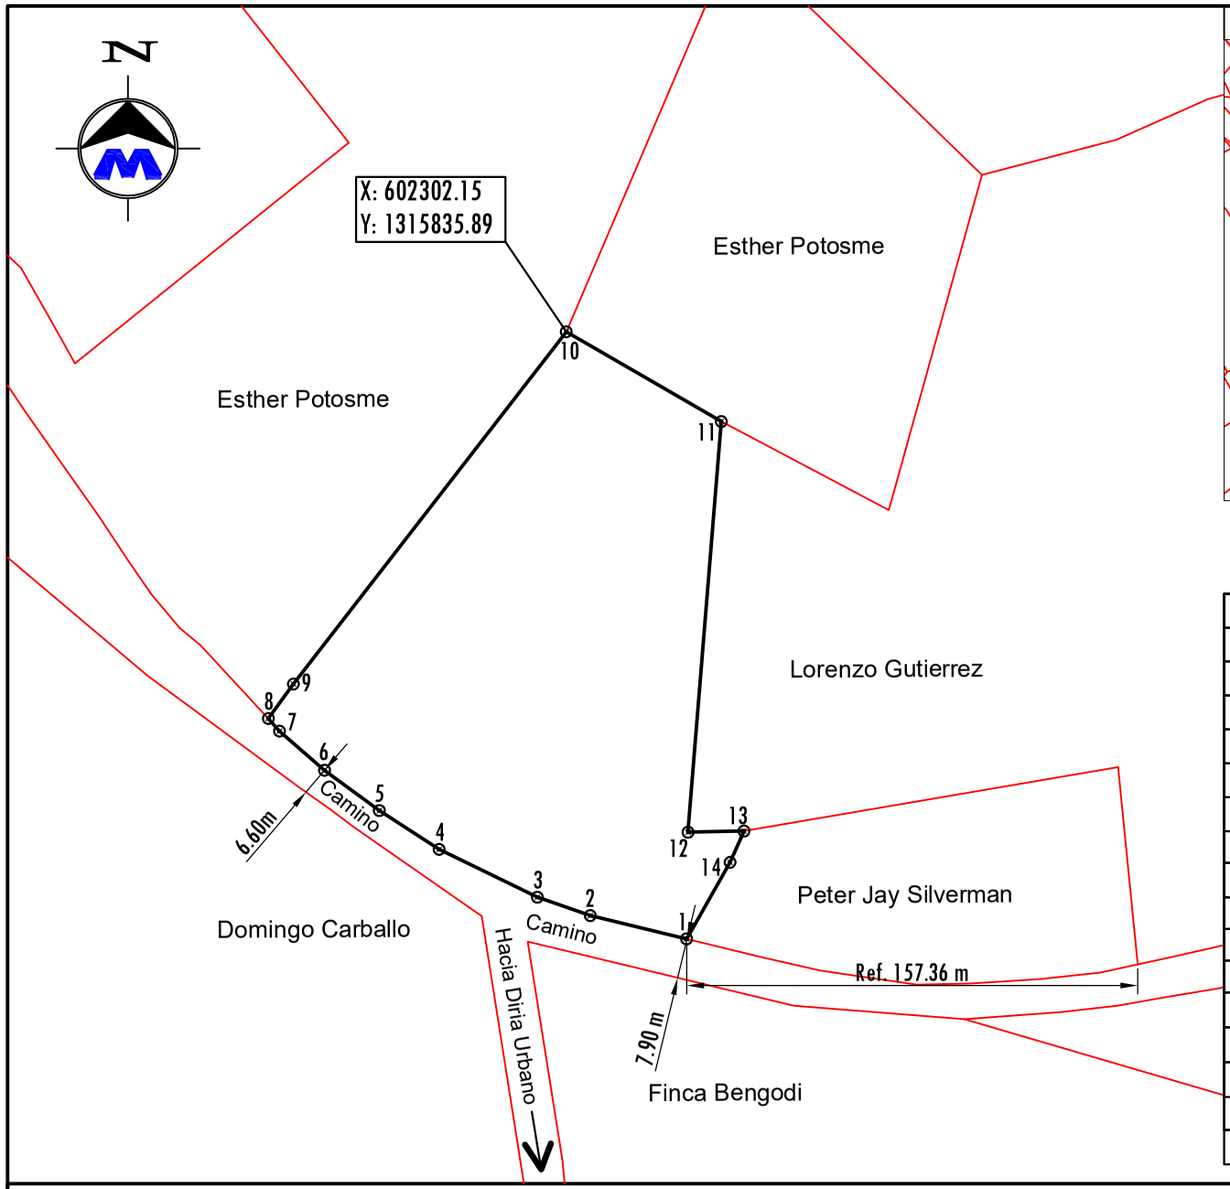

MUNICIPIO SAN JUAN DE ORIENTE DEPARTAMENTO DE MASAYA

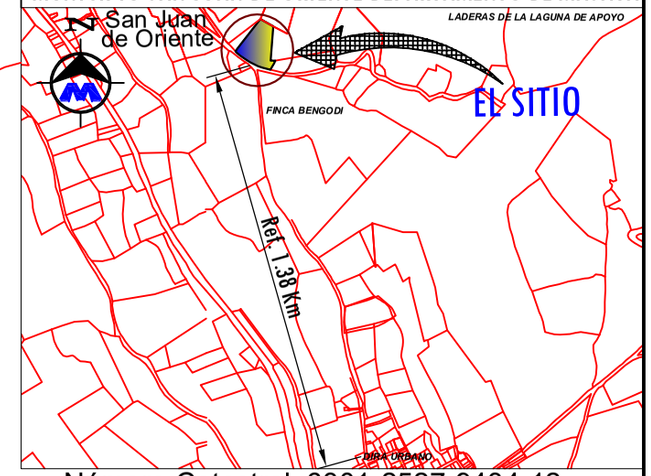

Número Catastral: 6301-2527-9434-12
Planta de Ubicacion Sin Escala

COORDENADAS NO VINCULADAS A LA RED GEODESICA DE NICARAGUA

DERROTERO			
LINEA	RUMBO	DIST	COORD UTM
1-2	N76°23'55"W	28.66	16P 602336.94, 1315660.29
2-3	N70°50'42"W	16.19	16P 602309.08, 1315667.03
3-4	N63°59'44"W	31.58	16P 602293.79, 1315672.34
4-5	N57°02'44"W	20.63	16P 602265.41, 1315686.19
5-6	N53°38'55"W	19.66	16P 602248.10, 1315697.41
6-7	N48°58'29"W	17.27	16P 602232.26, 1315709.06
7-8	N41°25'27"W	4.85	16P 602219.23, 1315720.40
8-9	N35°57'23"E	12.33	16P 602216.02, 1315724.04
9-10	N37°45'11"E	128.85	16P 602223.26, 1315734.02
10-11	S59°56'49"E	51.79	16P 602302.15, 1315835.89
11-12	S04°37'49"W	119.19	16P 602346.98, 1315809.96
12-13	N88°47'47"E	16.18	16P 602337.36, 1315691.16
13-14	S24°01'39"W	9.92	16P 602353.54, 1315691.50
14-1	S29°33'13"W	25.46	16P 602349.50, 1315682.44
Área: 14,099.98 m² = 19,999.62 Vrs²			

ESPACIO PARA ESQUELA

Objeto Lev: Venta Total	Número Catastral: 6301-2527-9434-12	FIRMA:
Enajenante: Peter Jay Silverman Pasaporte: 567486055	Ubicación: De final Diria Urbano 1.38 Km Norte. Municipio de San Juan de Oriente, Departamento de Masaya.	Ejecuta: Ing.Bosco Javier Morgan Lic. Catastral: BMM100426 Cel: 8883-7568 Email: ingmorgan73@gmail.com www.morganconstrucciones.com
Adquirientes: Larry Gene Rinkenberger JR Pasaporte: 681494296 Janet Elizabeth Rinkenberger Pasaporte: 681494297	Área: 14,099.98 m² = 19,999.62 Vrs² Escala:1 / 2000	Fecha:22 de mayo del 2025