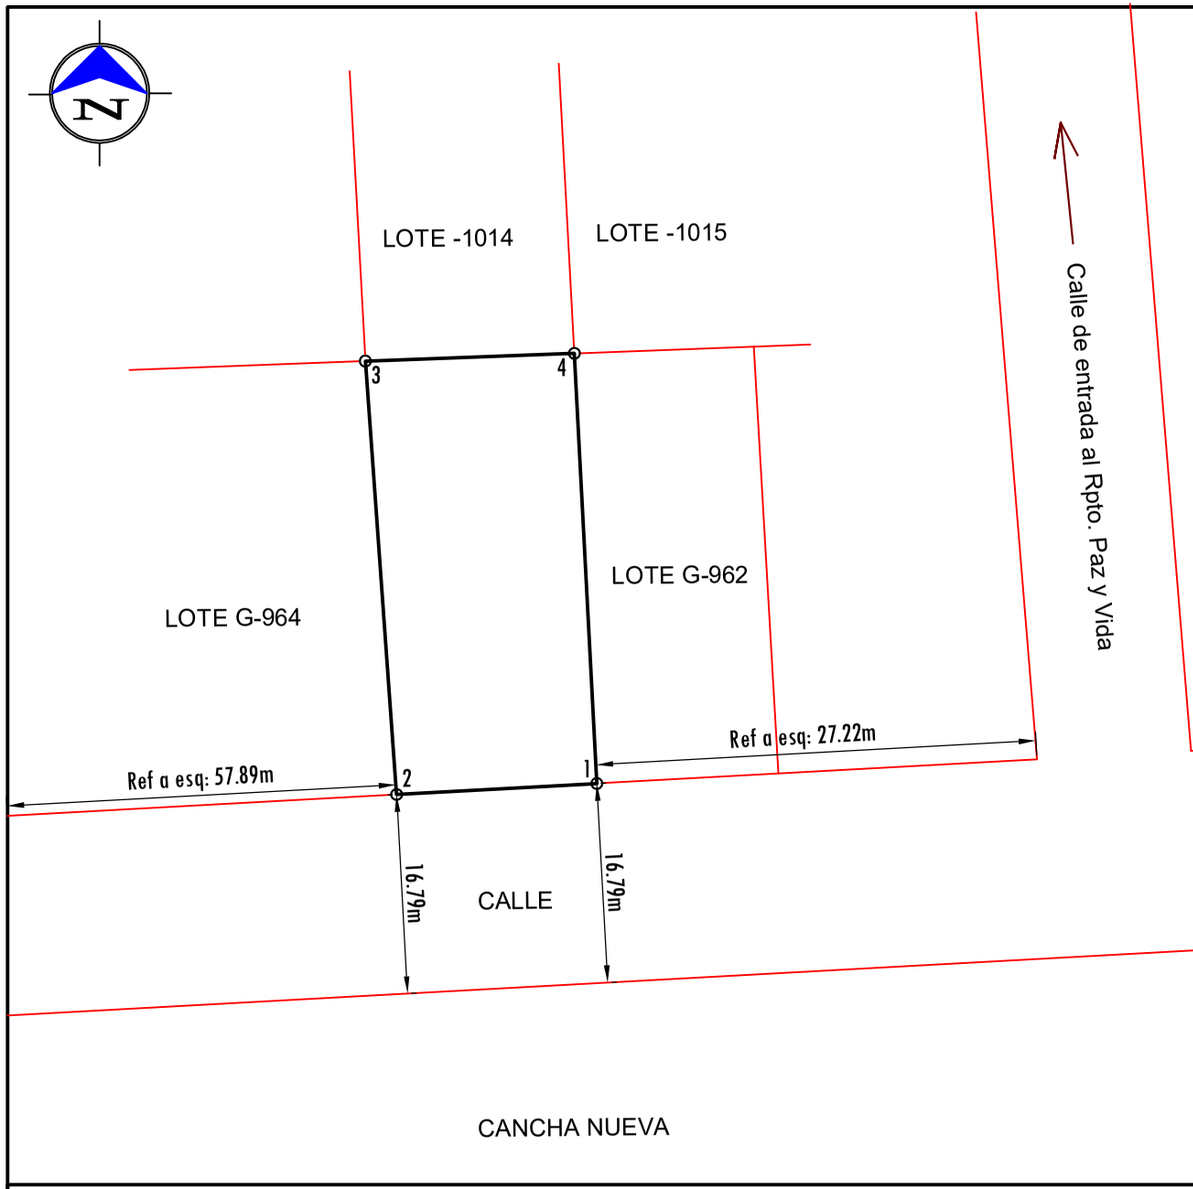

DEPARTAMENTO DE GRANADA MUNICIPIO DE GRANADA

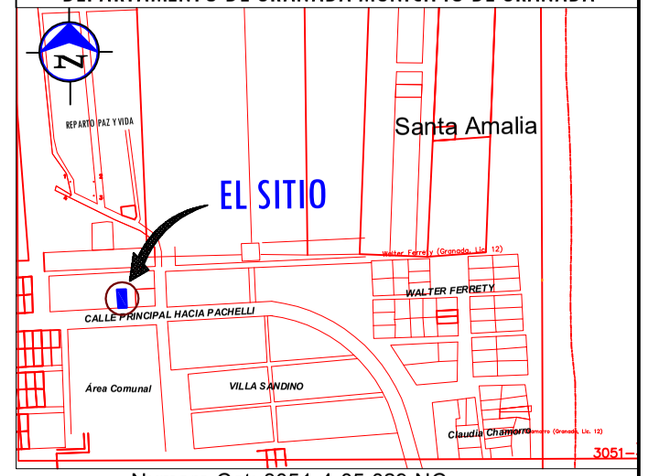

Numero Cat: 3051-4-05-029-NC

Planta de Ubicacion Sin Escala

COORDENADAS NO VINCULADAS A LA RED GEODESICA DE NICARAGUA

DERROTERO

LINEA	RUMBO	DIST	COORD UTM
1-2	S86°50'00"W	7.24	16P 614428.13, 1321032.64
2-3	N04°07'29"W	15.71	16P 614420.90, 1321032.24
3-4	N87°52'34"E	7.56	16P 614419.77, 1321047.91
4-1	S02°58'55"E	15.57	16P 614427.32, 1321048.19

Area: 115.688 m2 = 164.0936 vrs2

ESPACIO PARA ESQUELA

Objeto Lev: Donación total con Reserva de Usufructo	Numero Cat: 3051-4-05-029- NC	FIRMA:
Enajenante: Josefa Margarita Sequeira conocida como Josefa Margarita Sequeira Reyes Ced:121-230739-0002Q	Ubicacion: Villa Sandino Grupo G casa # 963. Municipio de Granada, Departamento de Granada.	Ejecuta: Ing.Bosco Javier Morgan Lic. Catastral: BMM100426 Cel: 8883-7568 Email: ingmorgan73@gmail.com servicios topograficos
Adquirientes: Vilma Rosa Altamirano Sequeira Ced:001-300467-0043R Samanta Xotchill Altamirano Ced: 201-180492-0003P	Area: 115.688 m2 = 164.0936 vrs2 — Escala: 1 / 250	Fecha: 13 de Mayo 2025