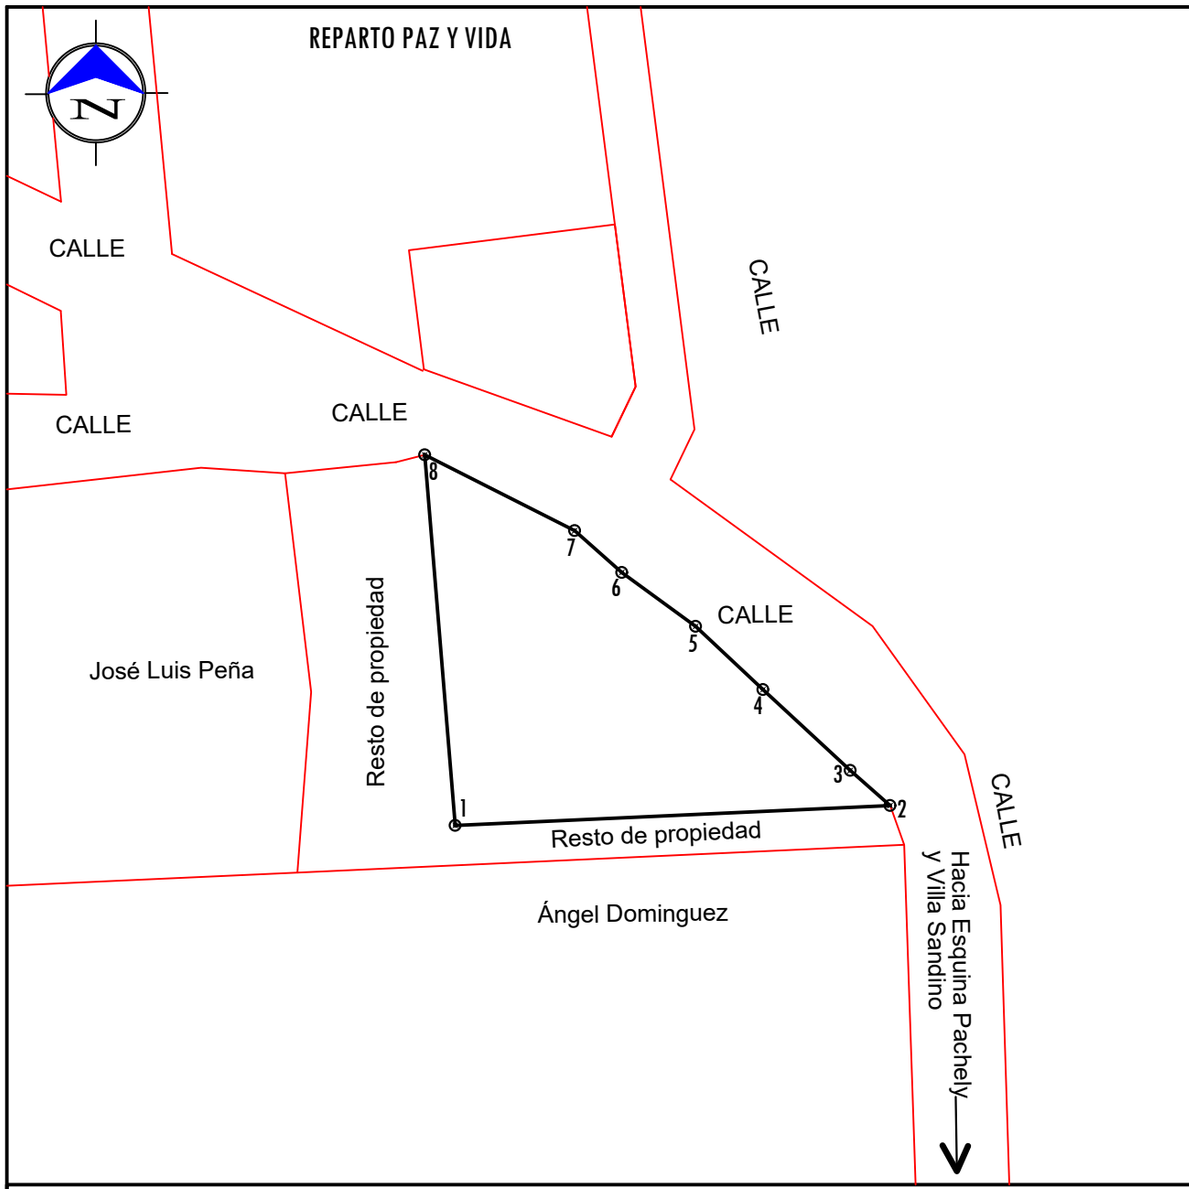

DEPARTAMENTO DE GRANADA MUNICIPIO DE GRANADA

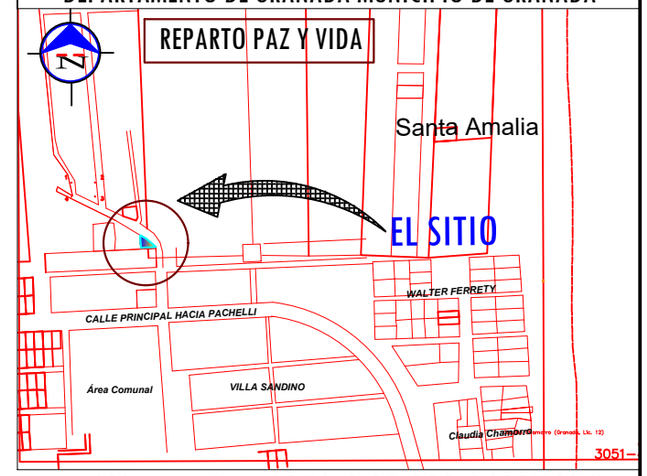

Número Cat: 3051-4-05-000-01627 N/C
Planta de Ubicacion Sin Escala

COORDENADAS NO VINCULADAS A LA RED GEODESICA DE NICARAGUA

DERROTERO			
LINEA	RUMBO	DIST	COORD UTM
1-2	N87°21'29"E	12.58	16P 614438.86, 1321084.28
2-3	N48°42'30"W	1.53	16P 614451.43, 1321084.86
3-4	N47°06'45"W	3.45	16P 614450.28, 1321085.87
4-5	N46°49'41"W	2.66	16P 614447.75, 1321088.22
5-6	N53°46'52"W	2.64	16P 614445.81, 1321090.04
6-7	N48°47'04"W	1.82	16P 614443.68, 1321091.60
7-8	N63°03'56"W	4.86	16P 614442.31, 1321092.80
8-1	S04°41'34"E	10.76	16P 614437.98, 1321095.00
Área: 75.7256 m² =107.4103 Vrs²			

ESPACIO PARA ESQUELA

Objeto Lev: Donación Parcial	Numero Cat: 3051-4-05-000-01627 N/C	FIRMA:
Enajenante: Rosa Idalia Dominguez Narvaez Ced:403-250681-0001N	Ubicacion: Reparto Paz y Vida de la entrada principal 1c norte 11.30m Oeste ,Municipio de Granada, Departamento de Granada.	Ejecuta: Ing.Bosco Javier Morgan Lic. Catastral: BMM100426 Cel: 8883-7568 Email: ingmorgan73@gmail.com www.morganconstrucciones.com
Adquiriente: Aminta del Socorro Dominguez Narvaez Ced:403-180583-0000E	Área: 75.7256 m² =107.4103 Vrs² Escala: 1 / 200	Fecha: 23 de abril del 2025