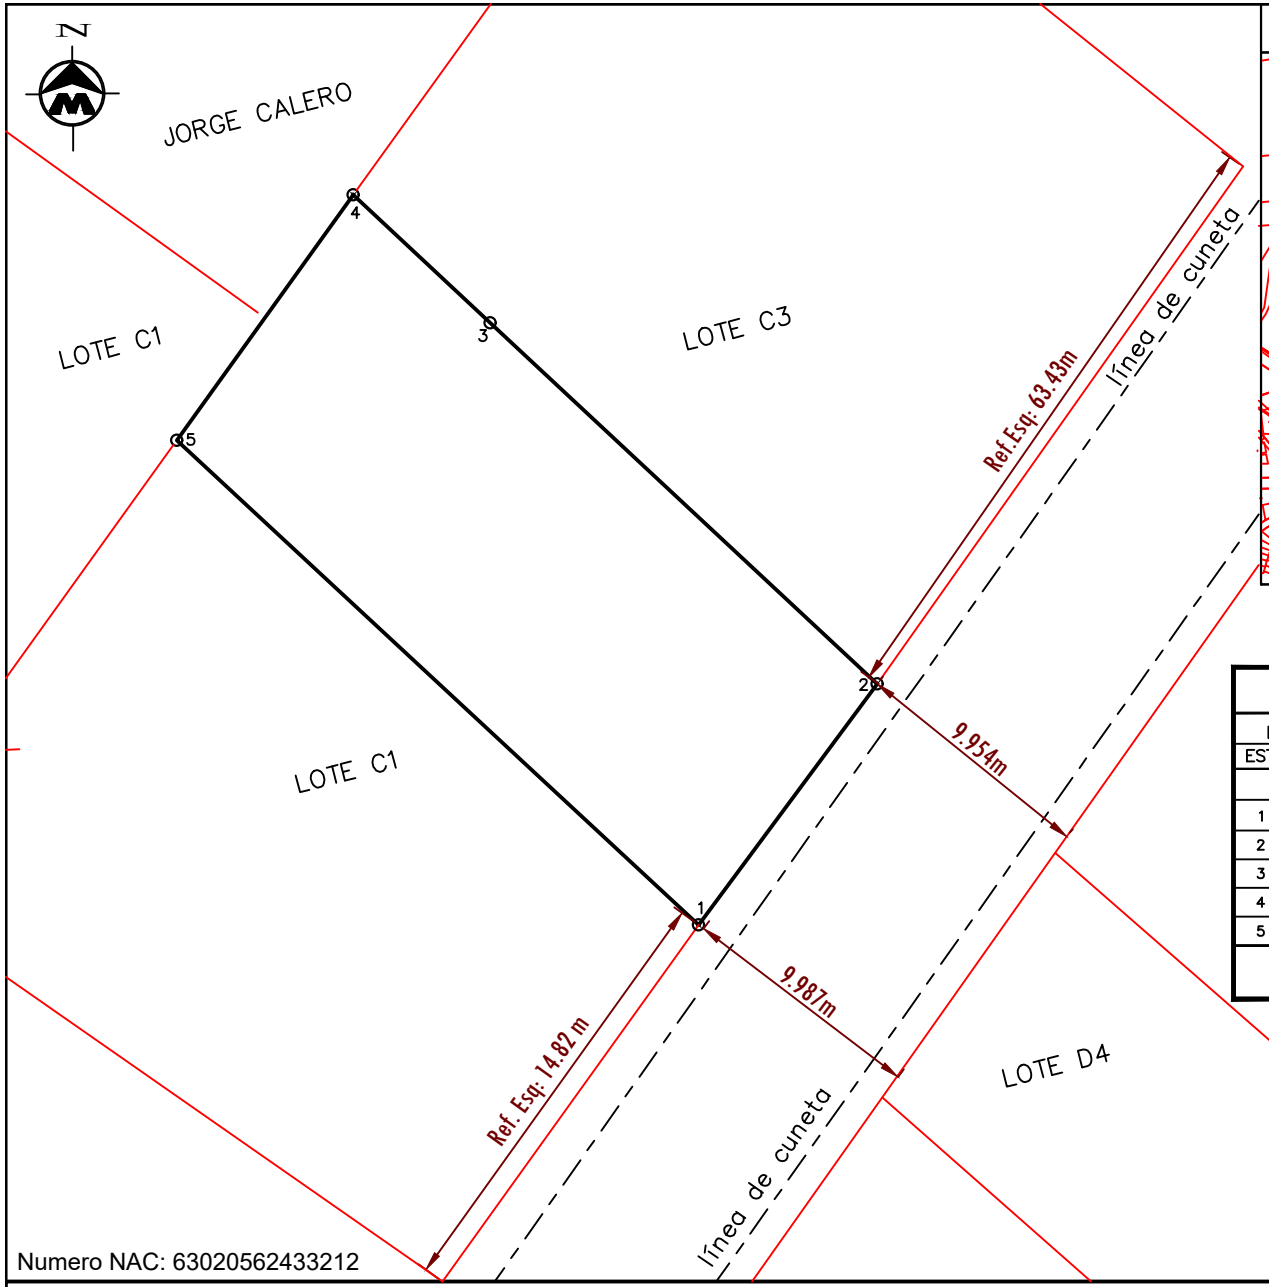

Numero NAC: 63020562433212

DEPARTAMENTO DE MASAYA, MUNICIPIO DE MASAYA

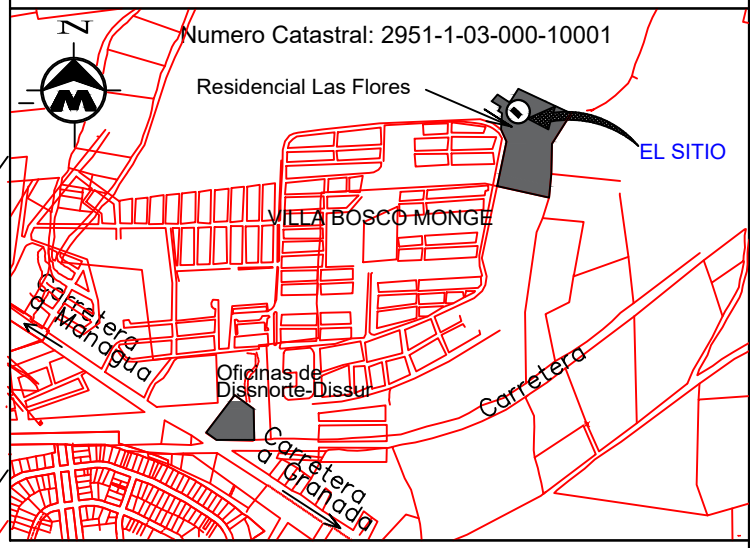

PLANTA DE UBICACION SIN ESCALA

COORDENADAS NO VINCULADAS A LA RED GEODESICA DE NICARAGUA

CUADRO DE CONSTRUCCION

LADO EST	LADO PV	RUMBO	DISTANCIA	V	COORDENADAS Y	COORDENADAS X
				1	1,325,219.8443	600,649.0628
1	2	N 36°31'38.35" E	9.99	2	1,325,227.8759	600,655.0118
2	3	N 46°59'35.32" W	17.64	3	1,325,239.9045	600,642.1158
3	4	N 46°56'15.64" W	6.24	4	1,325,244.1625	600,637.5596
4	5	S 35°43'37.09" W	10.07	5	1,325,235.9901	600,631.6813
5	1	S 47°06'38.77" E	23.72	1	1,325,219.8443	600,649.0628

SUPERFICIE = 236.96 m2

Objeto Lev: Venta Total	Numero Catastral: 2951-1-03-000-10001	FIRMA:
Enajenante: Alfonso Ramon Vega Cuadra Ced: 042-020762-0001U	Ubicacion: Residencial Las Flores, al norte de Villa Bosco Monge lote C-2. Municipio de Masaya, Dpto. de Masaya	Ejecuta: Ing.Bosco Javier Morgan Lic. Catastral: BMM100426 Cel: 8883-7568 Email: ingmorgan73@gmail.com SERVICIOS TOPOGRAFICOS
Adquiriente: Francisca Castillo Picado Ced: 365-041061-0000Q	Area: 236.96 m2= 336.100 vrs2 — Escala: 1/ 200	Fecha: 11 de octubre del 2024