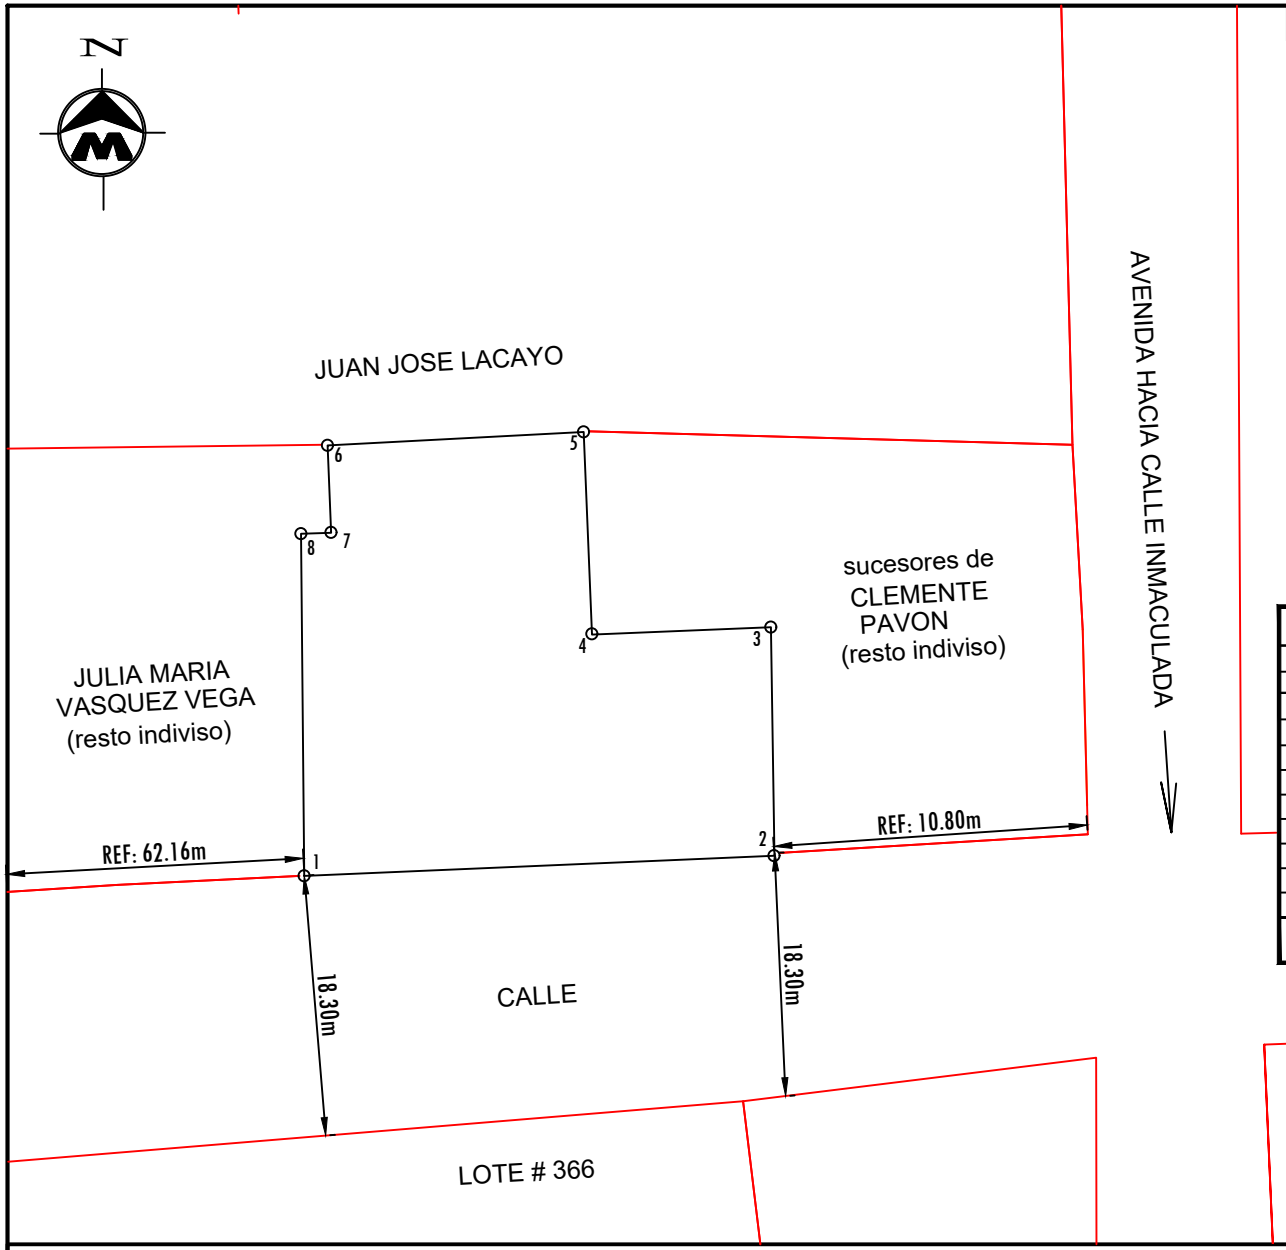

DEPARTAMENTO DE GRANADA MUNICIPIO DE GRANADA

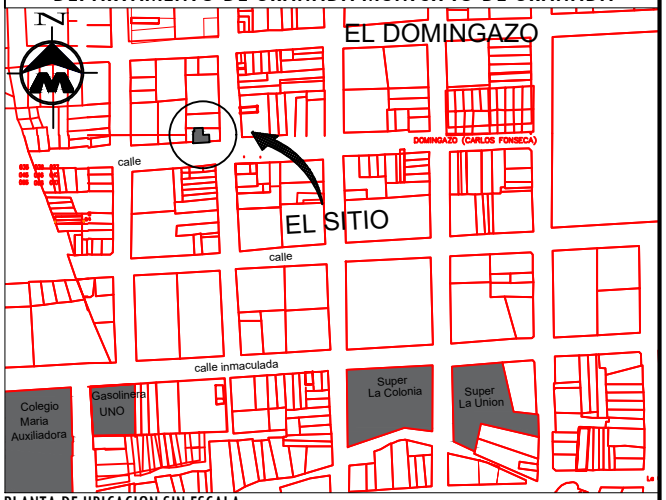

PLANTA DE UBICACION SIN ESCALA

Numero Catastral: 3051-4-05-047-08631

COORDENADAS NO VINCULADAS A LA RED GEODESICA DE NICARAGUA

CUADRO DE CONSTRUCCION

LADO EST	LADO PV	RUMBO	DISTANCIA	V	COORDENADAS Y	COORDENADAS X
				1	1,319,967.6111	613,083.4100
1	2	N 87°32'26.80" E	16.18	2	1,319,968.3052	613,099.5712
2	3	N 00°57'11.47" W	7.85	3	1,319,976.1563	613,099.4406
3	4	S 87°36'36.28" W	6.15	4	1,319,975.9000	613,093.3000
4	5	N 02°22'57.09" W	6.98	5	1,319,982.8700	613,093.0100
5	6	S 87°00'27.78" W	8.81	6	1,319,982.4100	613,084.2100
6	7	S 02°23'02.33" E	3.01	7	1,319,979.4068	613,084.3350
7	8	S 88°00'08.30" W	1.04	8	1,319,979.3706	613,083.2963
8	1	S 00°33'14.85" E	11.76	1	1,319,967.6111	613,083.4100

SUPERFICIE = 192.25 m2

CALLE

Objeto Lev: Venta de Parte Indivisa	Numero Catastral: 3051-4-05-047-08631		FIRMA:
Enajenante: Rubén Enrique Ramírez conocido como Ruben E, Ramirez Maria Isabel Rebolledo de Ramírez c.c. Maria Isabel Ramírez	Ubicacion: Barrio El Domingazo de La Gasolinera Uno Guapinol 2c norte 1/2c Este. Municipio de Granada. Departamento de Granada.		Ejecuta: Ing.Bosco Javier Morgan Lic. Catastral: BMM100426 Cel: 8883-7568 SERVICIOS TOPOGRÁFICOS
Adquiriente: Jury Roblero Ramírez Cedula: 202-240961-0003V	ÁREA= 192.25 m² = 272.69 vrs²	Escala: 1 /250	Fecha: 09 de octubre del 2024