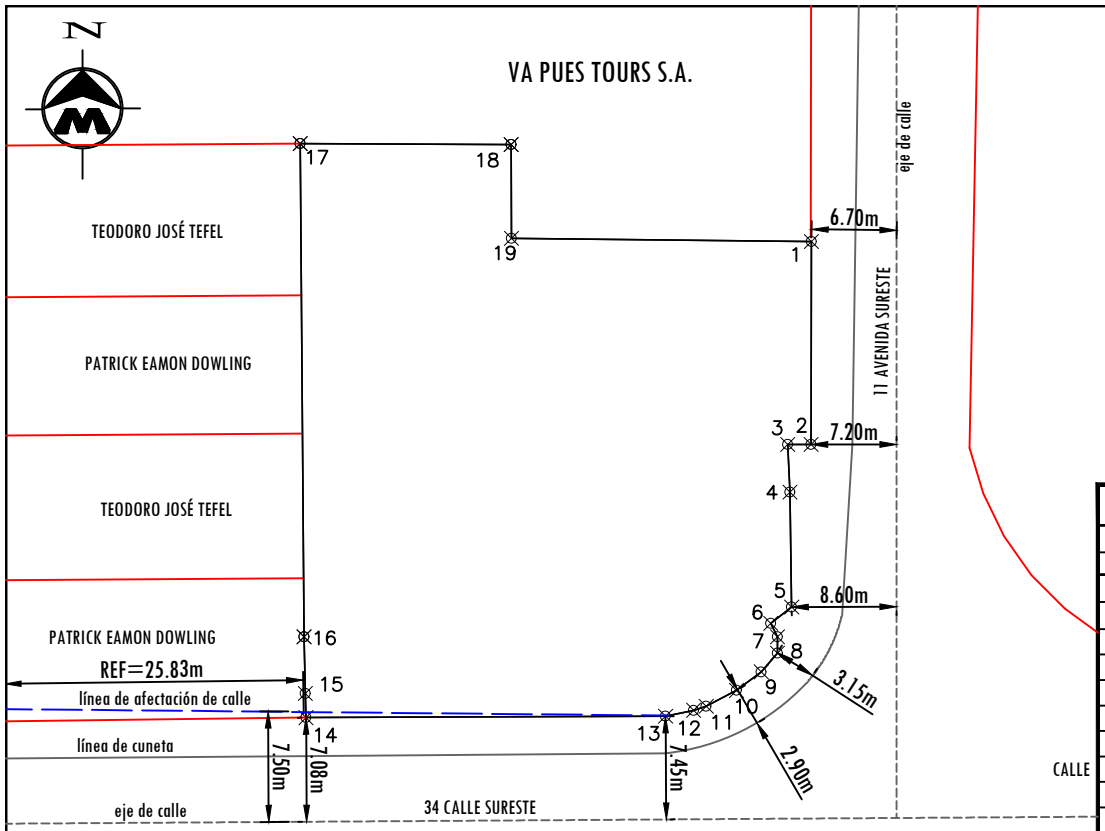

DEPARTAMENTO DE MANAGUA MUNICIPIO DE MANAGUA

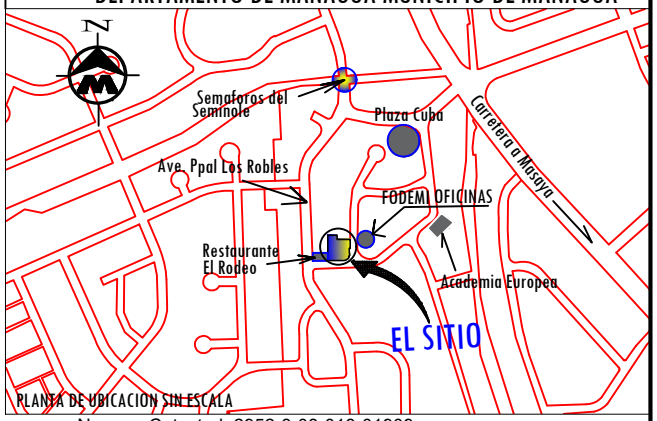

Numero Catastral: 2952-3-08-018-01909

COORDENADAS NO VINCULADAS AL SISTEMA NACIONAL DE COORDENADAS

CUADRO DE CONSTRUCCION

LADO EST	LADO PV	RUMBO	DISTANCIA	V	COORDENADAS Y	COORDENADAS X
				1	1,340,012.7200	579,896.9900
1	2	S 00°04'30.87" W	15.23	2	1,339,997.4900	579,896.9700
2	3	N 90°00'00" W	1.76	3	1,339,997.4900	579,895.2100
3	4	S 02°33'32.41" E	3.58	4	1,339,993.9100	579,895.3700
4	5	S 00°55'49.71" E	8.62	5	1,339,985.2900	579,895.5100
5	6	S 52°09'01.04" W	1.99	6	1,339,984.0700	579,893.9400
6	7	S 26°47'29.46" E	1.13	7	1,339,983.0600	579,894.4500
7	8	S 00°00'00" E	1.22	8	1,339,981.8400	579,894.4500
8	9	S 40°52'04.58" W	1.86	9	1,339,980.4300	579,893.2300
9	10	S 53°22'33.62" W	2.33	10	1,339,979.0400	579,891.3600
10	11	S 62°13'51.64" W	2.55	11	1,339,977.8500	579,889.1000
11	12	S 72°17'58.46" W	0.99	12	1,339,977.5500	579,888.1600
12	13	S 78°13'15.12" W	2.16	13	1,339,977.1100	579,886.0500
13	14	S 89°45'58.73" W	26.97	14	1,339,977.0000	579,859.0800
14	15	N 01°34'56.47" W	1.81	15	1,339,978.8100	579,859.0300
15	16	N 01°28'57.43" W	4.25	16	1,339,983.0600	579,858.9200
16	17	N 00°25'05.15" W	37.00	17	1,340,020.0600	579,858.6500
17	18	S 89°46'57.71" E	15.82	18	1,340,020.0000	579,874.4700
18	19	S 00°09'45.98" E	7.04	19	1,340,012.9600	579,874.4900
19	1	S 89°23'19.93" E	22.50	1	1,340,012.7200	579,896.9900

SUPERFICIE = 1,423.97 m2

Objeto Lev: Mensura Judicial	Numero Catastral: 2952-3-08-018-01909		Fecha: 22 de agosto del 2024
Propietario: Agropecuaria Los Lirios S.A.	Ubicacion: Avenida Principal Los Robles, de los semaforos de Siminole 350m al Sur 60m al Este. Colonia Los Robles, lote # 46. Municipio de Managua. Dpto Managua.		Ejecuta: Ing.Bosco Javier Morgan Lic. Catastral: BMM100426 cel:8883-7568
Factor de Escala: 1.418415	ÁREA= 1,423.97 m² = 2,019.78 vrs²	Escala: 1 /500	FIRMA:

ESPACIO PARA ESQUELA