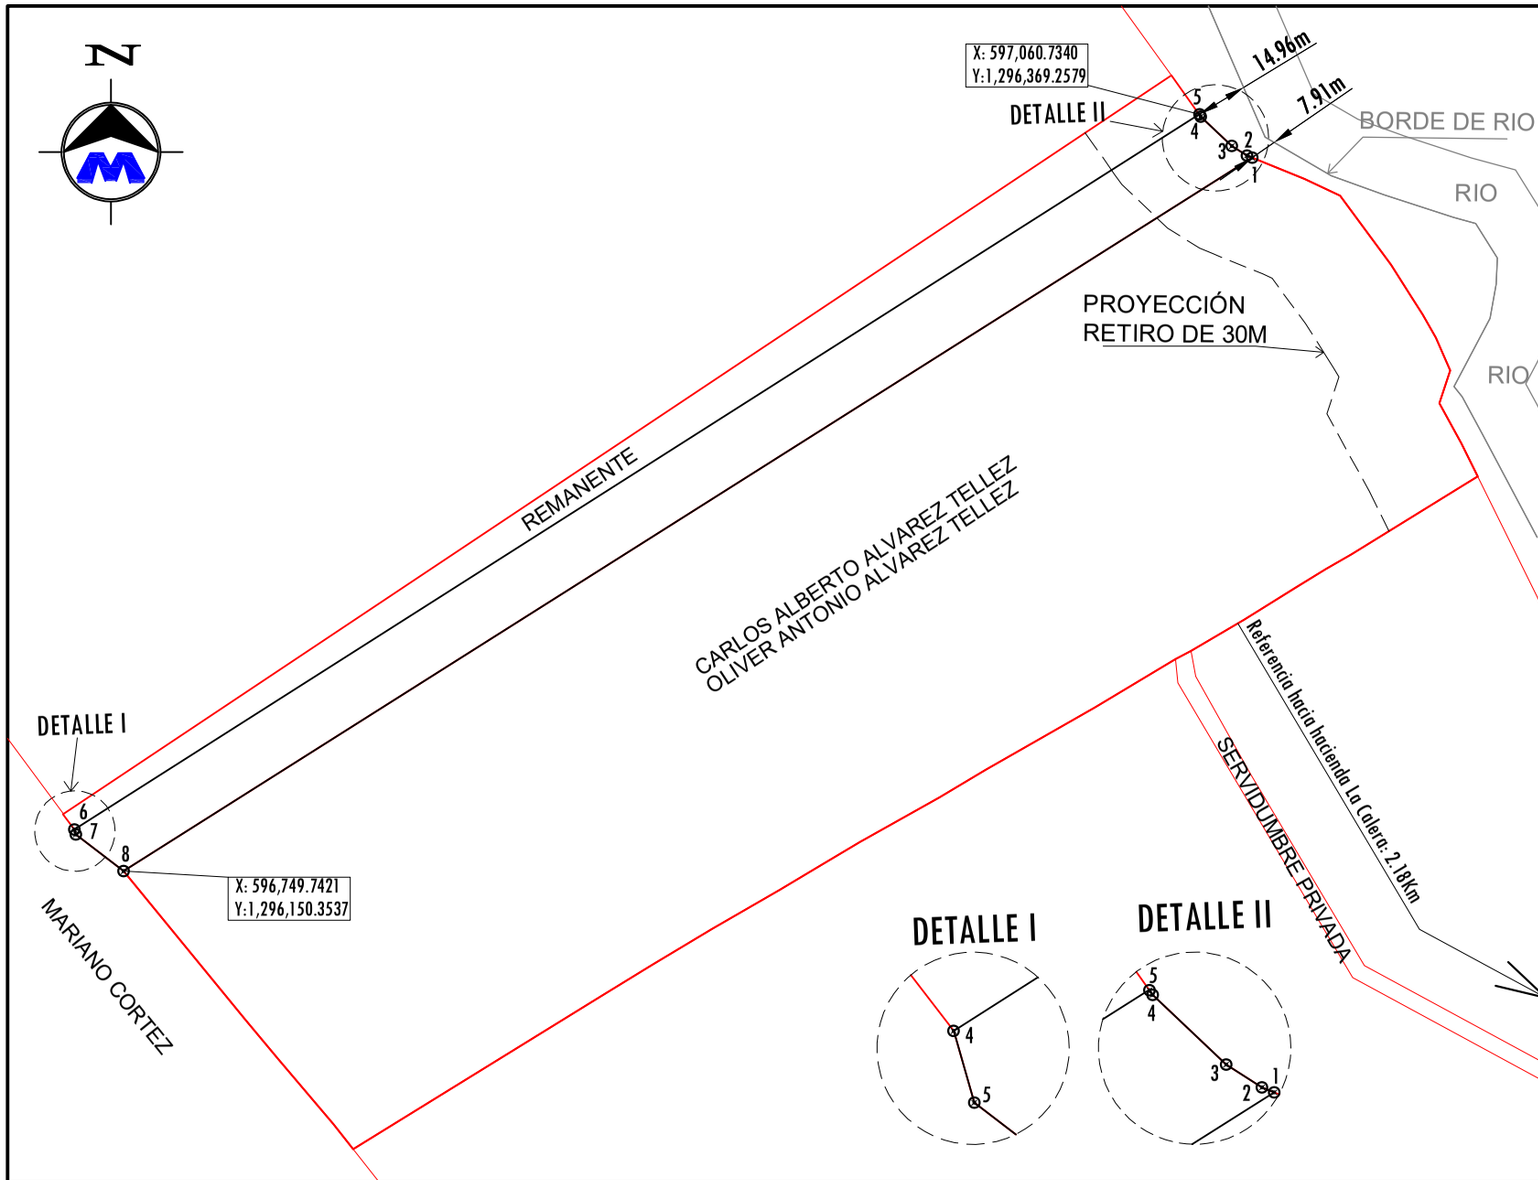

DEPARTAMENTO DE CARAZO MUNICIPIO DE SANTA TEREZA

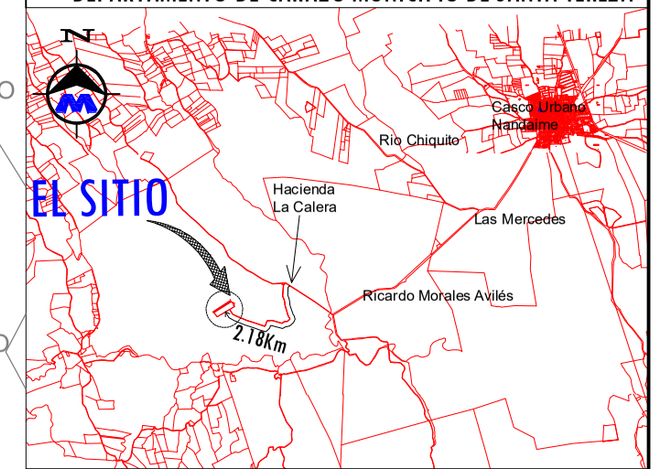

Planta de Ubicacion Sin Escala
Número Catastral:2951-2-11-000-(00200)

COORDENADAS NO VINCULADAS A LA RED GEODESICA DE NICARAGUA

CUADRO DE CONSTRUCCION

LADO EST	LADO PV	RUMBO	DISTANCIA	V	COORDENADAS Y	COORDENADAS X
				1	1,296,356.7414	597,076.0056
1	2	N 67°51'30.87" W	1.615	2	1,296,357.3500	597,074.5099
2	3	N 57°46'38.57" W	5.194	3	1,296,360.1194	597,070.1161
3	4	N 46°21'54.52" W	12.377	4	1,296,368.6599	597,061.1586
4	5	N 35°22'28.62" W	0.733	5	1,296,369.2579	597,060.7340
5	6	S 57°32'48.42" W	385.437	6	1,296,162.4284	596,735.4910
6	7	S 16°02'39.48" E	1.479	7	1,296,161.0066	596,735.8999
7	8	S 52°25'05.33" E	17.467	8	1,296,150.3537	596,749.7421
8	1	N 57°41'00.15" E	386.062	1	1,296,356.7414	597,076.0056

SUPERFICIE = 7,050.143 m2 = 0.71 Hectareas = 1.01 Mnz

Objeto Lev: Venta Parcial-Desmembracion	Número Catastral: 2951-2-11-000-(00200)	Fecha: 16 de Enero del 2025	FIRMA:
Enajenantes: Carlos Alberto Alvarez Tellez, Ced: 001-030297-0006R Oliver Antonio Alvarez Tellez, Ced: 001-300998-0018P	Ubicación: Cmca La Calera, de la hacienda La Calera 2.18 Km sobre acceso Suroeste. Municipio de Santa Tereza. Departamento de Carazo.	Ejecuta: Ing.Bosco Javier Morgan Lic. Catastral: BMM100426 Cel: 8883-7568 Email: ingmorgan73@gmail.com servicios topograficos	
Adquiere: Ana Julia Sandoval Flores, Ced: 321-260794-0006F Armando Josue Traña, Ced: 044-220100-1000G	Area: 7,050.143 m2 = 0.71 Hectareas = 1.01 Mnz	Escala: 1 / 2,000	