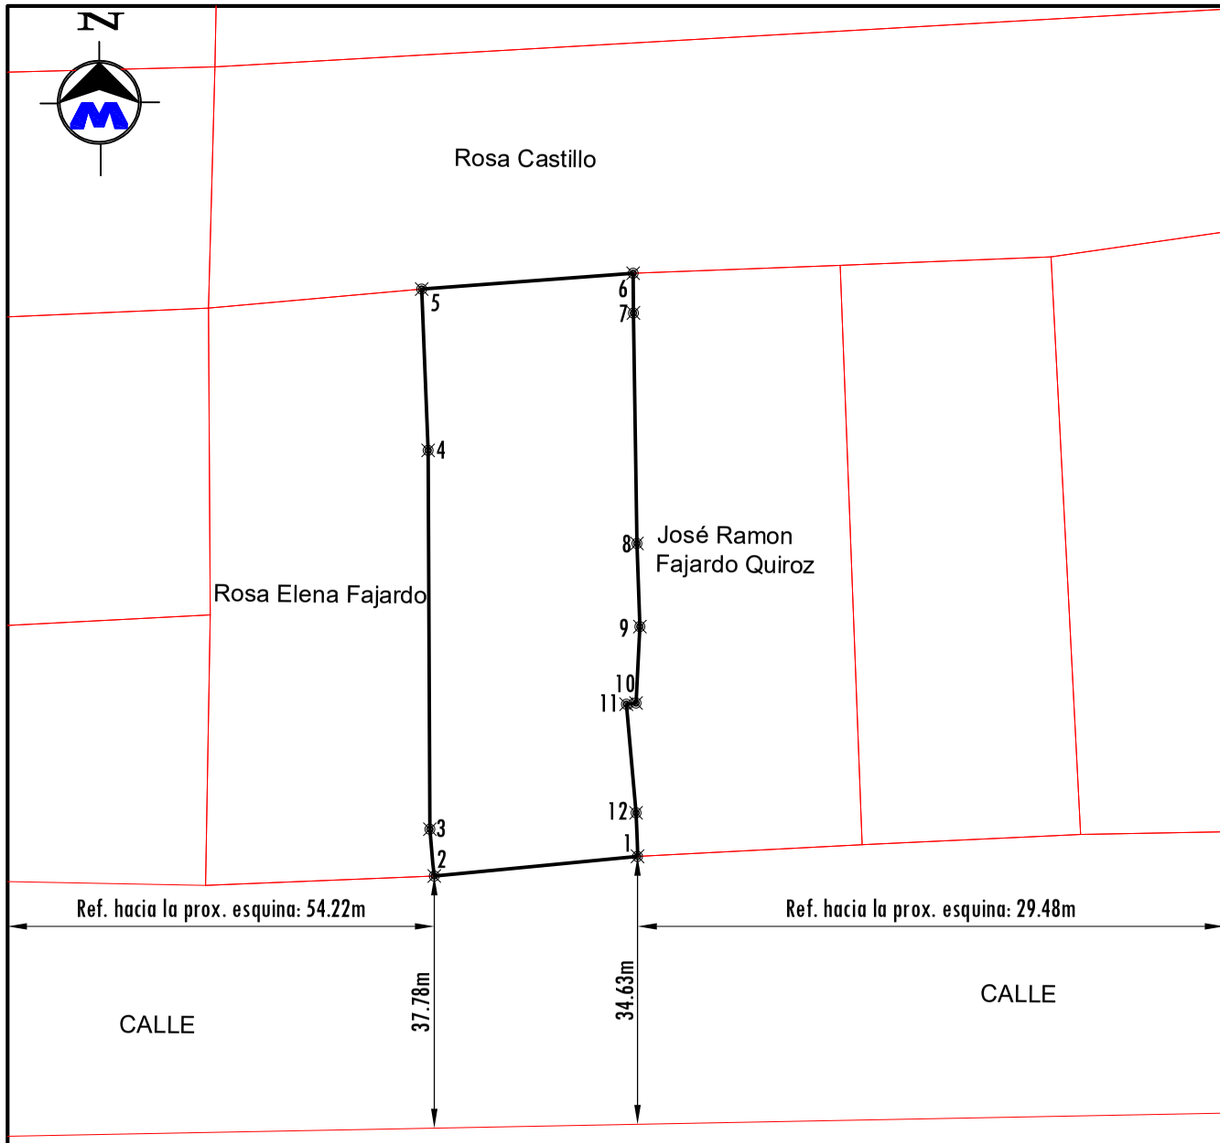

MUNICIPIO DE GRANADA. DEPARTAMENTO DE GRANADA

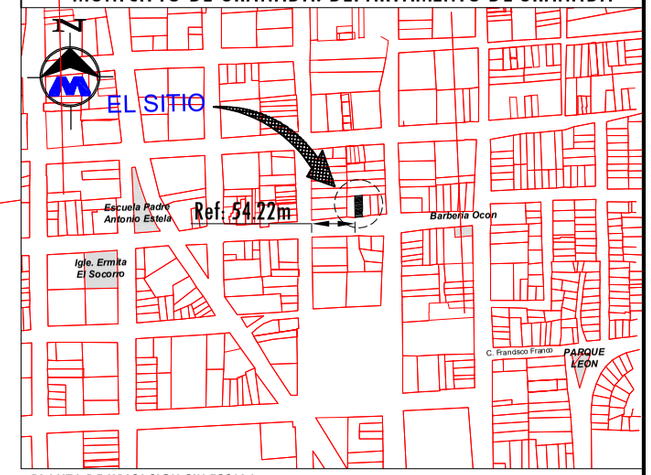

PLANTA DE UBICACION SIN ESCALA

Numero Catastral: 6312-3073-0208-11

COORDENADAS NO VINCULADAS A LA RED GEODESICA DE NICARAGUA

CUADRO DE CONSTRUCCION

LADO EST	LADO PV	RUMBO	DISTANCIA	V	COORDENADAS Y	COORDENADAS X
				1	1,320,325.8400	613,709.1900
1	2	S 84°25'51.39" W	8.862	2	1,320,324.9800	613,700.3700
2	3	N 05°19'15.68" W	2.049	3	1,320,327.0200	613,700.1800
3	4	N 00°16'44.32" W	16.430	4	1,320,343.4500	613,700.1000
4	5	N 02°12'31.99" W	7.005	5	1,320,350.4500	613,699.8300
5	6	N 85°41'48.72" E	9.196	6	1,320,351.1400	613,709.0000
6	7	S 00°19'59.20" E	1.720	7	1,320,349.4200	613,709.0100
7	8	S 00°51'30.65" E	10.011	8	1,320,339.4100	613,709.1600
8	9	S 02°03'44.61" E	3.612	9	1,320,335.8000	613,709.2900
9	10	S 02°46'02.75" W	3.314	10	1,320,332.4900	613,709.1300
10	11	S 83°22'02.95" W	0.433	11	1,320,332.4400	613,708.7000
11	12	S 05°05'05.86" E	4.739	12	1,320,327.7200	613,709.1200
12	1	S 02°07'56.53" E	1.881	1	1,320,325.8400	613,709.1900

SUPERFICIE = 228.38 m2= 323.94 Vrs2

Objeto: Compraventa Total	Número Catastral: 6312-3073-0208-11		FIRMA:
Enajenante: Norma Isabel Morales Fajardo Ced: 001-291261-0046C	Ubicación: Bo. El Domingazo, de Iglesia Ermita El Socorro 2 ½ C.E. Municipio de Granada, Departamento de Granada.		Ejecuta: Ing.Bosco Javier Morgan Lic. Catastral: BMM100426 Cel: 8883-7568 Email: ingmorgan73@gmail.com www.morganconstrucciones.com
Adquiriente: Jason Antonio Corea Bravo Ced: 201-060996-0004A	Área = 228.38 m2= 323.94 Vrs2	Escala: 1: 300	Fecha: 6 de Enero del 2026

ESPACIO PARA ESQUELA