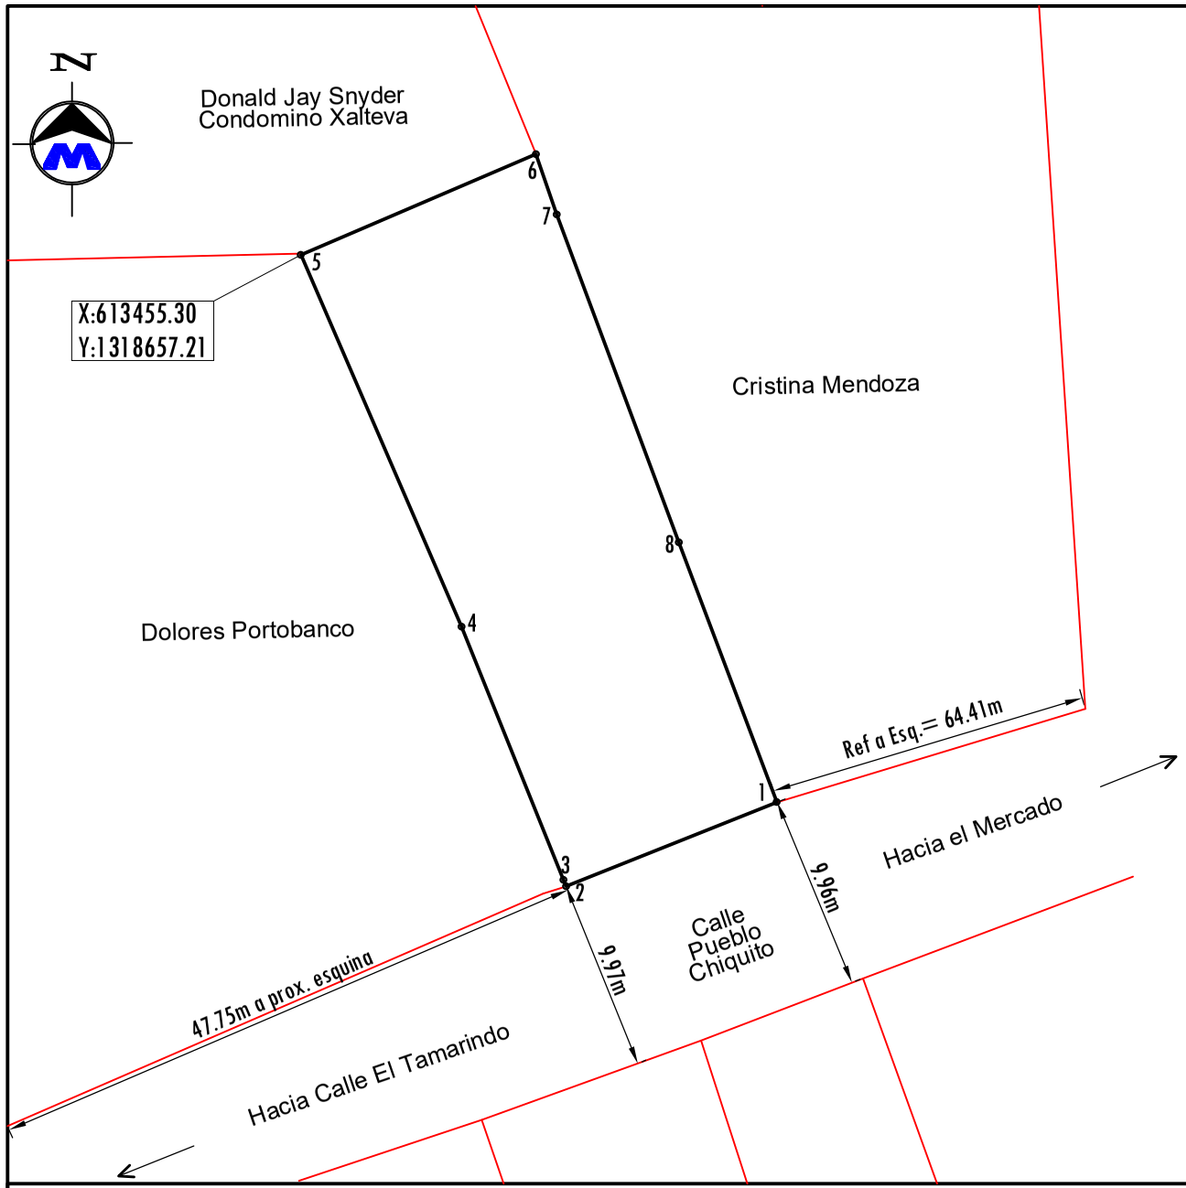

DEPARTAMENTO DE GRANADA MUNICIPIO DE GRANADA

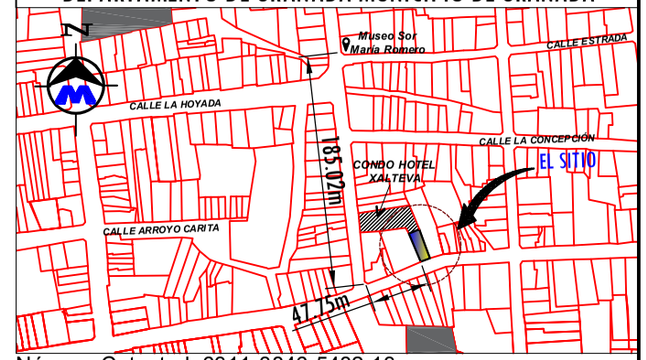

Número Catastral: 6311-3846-5482-13
Planta de Ubicación Sin Escala

COORDENADAS NO VINCULADAS A LA RED GEODESICA DE NICARAGUA

CUADRO DE CONSTRUCCION

LADO EST	LADO PV	RUMBO	DISTANCIA	V	COORDENADAS Y	COORDENADAS X
				1	1,318,637.4050	613,472.5020
1	2	S 68°17'26.09" W	8.200	2	1,318,634.3717	613,464.8833
2	3	N 21°54'00.30" W	0.248	3	1,318,634.6018	613,464.7908
3	4	N 21°53'52.68" W	9.873	4	1,318,643.7625	613,461.1086
4	5	N 23°22'08.03" W	14.644	5	1,318,657.2054	613,455.3000
5	6	N 66°48'47.56" E	9.244	6	1,318,660.8449	613,463.7970
6	7	S 18°52'46.31" E	2.307	7	1,318,658.6623	613,464.5434
7	8	S 20°25'24.12" E	12.651	8	1,318,646.8066	613,468.9580
8	1	S 20°39'15.45" E	10.047	1	1,318,637.4050	613,472.5020

SUPERFICIE = 214.031 m2 = 303.58 Vrs2

Objeto Lev: Venta Total	Numero Catastral: 6311-3846-5482-13	FIRMA:
Enajenante: Donald Jay Snyder Pasaporte USA: A28963085	Ubicacion: Casa Museo Sor María Romero 185.02 m SE, 47.75 m al Este, Condominio Hotel Xalteva, M/I. Municipio de Granada, Departamento de Granada.	Ejecuta: Ing.Bosco Javier Morgan Lic. Catastral: BMM100426 Cel: 8883-7568 Email: ingmorgan73@gmail.com
Adquiriente: Ramak Jaafar-Nejad Pasaporte: AA334424	Área: 214.031 m2 = 303.58 Vrs2 — Escala: 1 / 250	Fecha: 8 de Enero del 2026

ESPACIO PARA ESQUELA