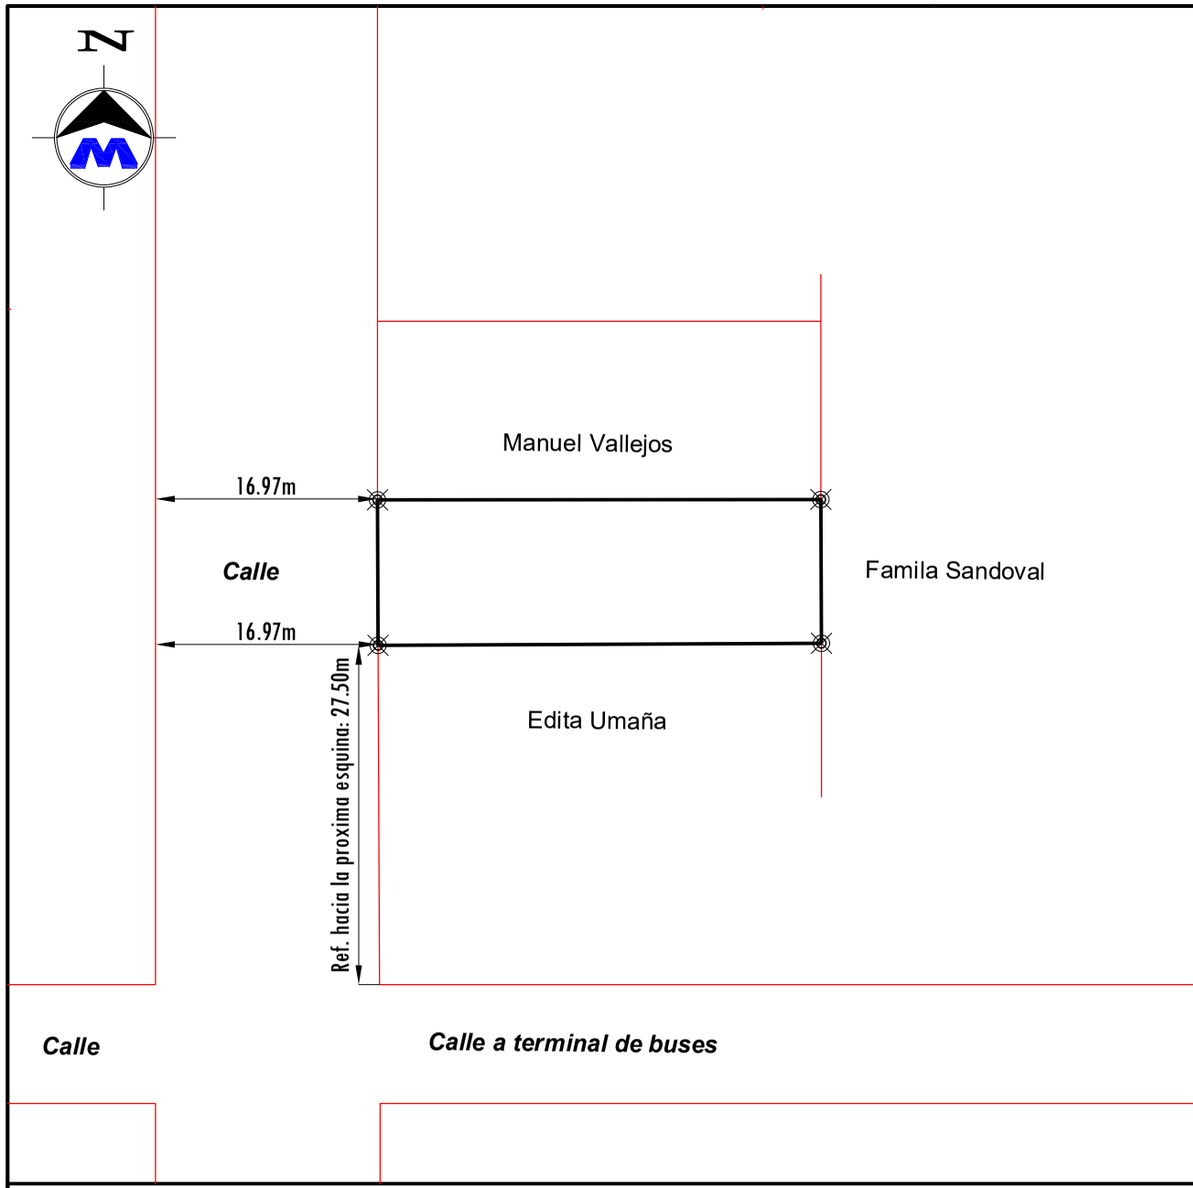

MUNICIPIO DE GRANADA. DEPARTAMENTO DE GRANADA.

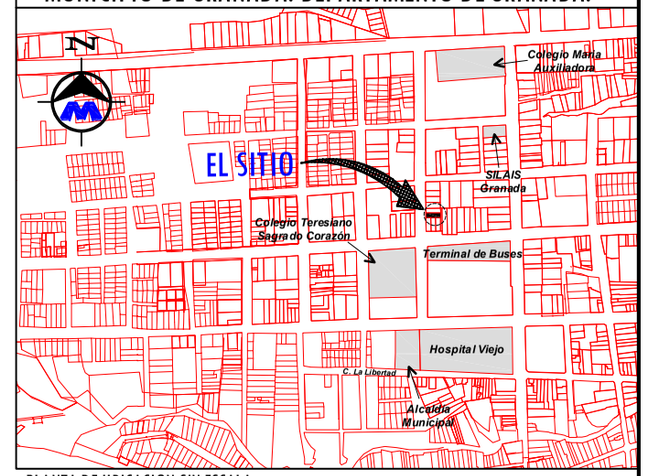

PLANTA DE UBICACION SIN ESCALA

Numero Catastral: 6311-2984-2172-16

COORDENADAS NO VINCULADAS A LA RED GEODESICA DE NICARAGUA

CUADRO DE CONSTRUCCION

LADO EST	LADO PV	RUMBO	DISTANCIA	V	COORDENADAS Y	COORDENADAS X
				1	1,319,414.9045	612,821.1600
1	2	N 00°15'29.12" W	8.417	2	1,319,423.3211	612,821.1221
2	3	N 89°56'07.64" E	25.638	3	1,319,423.3500	612,846.7600
3	4	S 00°16'30.46" E	8.330	4	1,319,415.0200	612,846.8000
4	1	S 89°44'30.88" W	25.640	1	1,319,414.9045	612,821.1600

SUPERFICIE = 214.686 m2 = 304.51 Vrs2

Solicitantes:

Margarita Isabel Berrios Aleman; Ced: 201-141264-0003K

Maria Lydia Berrios Aleman; Ced: 201-020957-0002B

Objeto: Verificación de área	Número Catastral: 6311-2984-2172-16	FIRMA:	SELLO
Propietario: Eufemia de Jesus Aleman Leon Certificado de defunción Tomo: 10017, Folio: 90 c.c. Lydia Aleman de Berrios y tambien como Eufemia de Jesus Alemán Leon de Berrios	Ubicación: Campo de Aterrizaje, del terminal de Buses a Managua 1c al Oeste y 27.50 m al Norte. Municipio de Granada. Departamento de Granada.	Ejecuta: Ing.Bosco Javier Morgan Lic. Catastral: BMM100426 Cel: 8883-7568 Email: ingmorgan73@gmail.com www.morganconstrucciones.com	
Solicitantes: Indicado	Área: 214.686 m2 = 304.51 Vrs2 / Escala: 1: 400	Fecha: 16 de Febrero del 2026	

ESPACIO PARA ESQUELA