REPÚBLICA DE NICARAGUA
CONSEJO SUPREMO ELECTORAL
CÉDULA DE IDENTIDAD
281-140247-0002C
Nombres
JOSE RAMON
Apellidos
CASTILLO MALESPIN
Fecha de Nacimiento
Lugar de Nacimiento
14-02-1947
LEON
Sexo
M
Director General
Emision 29-07-2019
Expiracion 29-07-2029

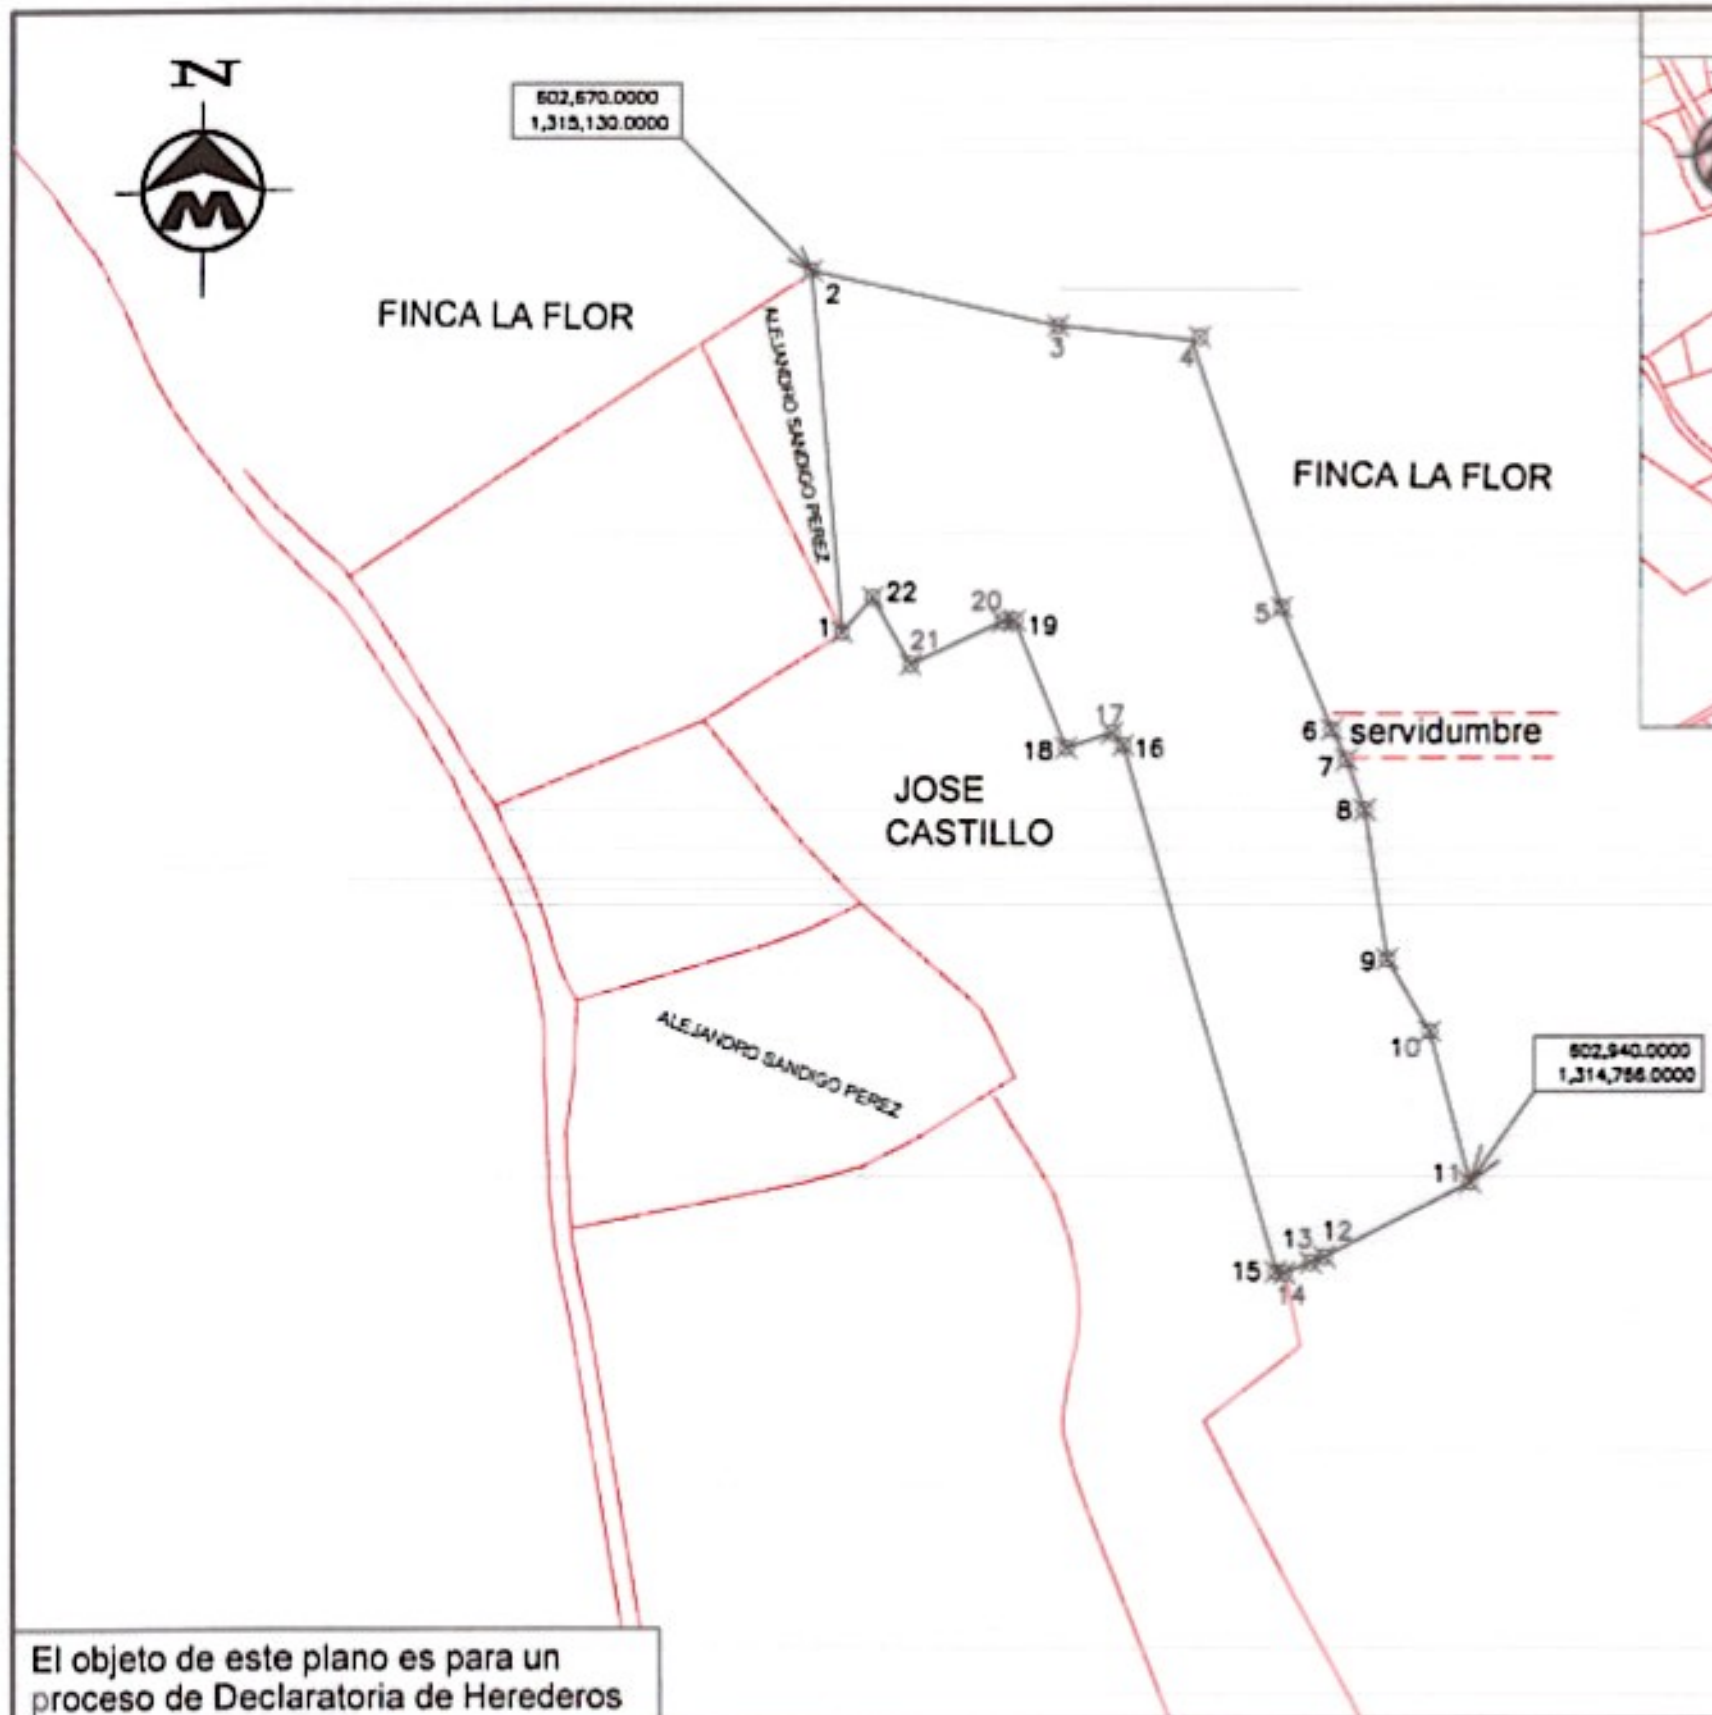

Numero Catastral: 2951-1-12-000-03800

COORDENADAS NO VINCULADAS AL SISTEMA NACIONAL DE COORDENADAS

CUADRO DE CONSTRUCCION

LADO EST	LADO PV	RUMBO	DISTANCIA	V	COORDENADAS Y	COORDENADAS X
				1	1,314,981.6666	602,685.9693
1	2	N 04°56'51.74" W	144.549	2	1,315,125.6966	602,673.5025
2	3	S 77°22'00.60" E	101.438	3	1,315,103.5135	602,772.4849
3	4	S 83°39'52.71" E	54.042	4	1,315,097.4877	602,826.1897
4	5	S 18°53'30.52" E	112.425	5	1,314,991.1184	602,862.5811
5	6	S 22°36'58.86" E	52.577	6	1,314,942.5649	602,882.8099
6	7	S 23°47'21.16" E	13.455	7	1,314,930.4704	602,888.6634
7	8	S 20°17'56.71" E	21.144	8	1,314,910.8393	602,895.9988
8	9	S 08°37'56.67" E	60.065	9	1,314,851.2545	602,905.0143
9	10	S 29°47'50.92" E	33.419	10	1,314,822.3540	602,921.6213
10	11	S 14°49'04.88" E	61.880	11	1,314,762.4321	602,937.4470
11	12	S 62°53'13.74" W	65.261	12	1,314,732.6898	602,879.3676
12	13	S 68°16'42.98" W	5.773	13	1,314,730.5534	602,873.0949
13	14	S 68°09'20.34" W	11.640	14	1,314,726.2222	602,863.1903
14	15	N 77°49'44.01" W	2.987	15	1,314,726.8520	602,860.2701
15	16	N 16°23'12.17" W	218.484	16	1,314,936.4610	602,798.6317
16	17	N 42°17'22.91" W	8.615	17	1,314,941.3544	602,794.1806
17	18	S 72°14'41.37" W	19.423	18	1,314,935.4314	602,775.6831
18	19	N 21°56'31.94" W	54.877	19	1,314,986.3330	602,755.1773
19	20	S 80°26'55.46" W	4.894	20	1,314,985.9608	602,750.4984
20	21	S 64°50'31.04" W	40.733	21	1,314,968.6444	602,713.6297
21	22	N 29°38'47.94" W	30.834	22	1,314,995.4424	602,698.3774
22	1	S 42°03'19.72" W	18.524	1	1,314,981.6666	602,685.9693
SUPERFICIE = 42,733.468 m2						

El objeto de este plano es para un proceso de Declaratoria de Herederos

Objeto Lev: Verificacion de Area	Numero Catastral: 2951-1-12-000-03800	FIRMA:	SELLO
Propietario: Lilliam del Carmen Pérez Lopez conocida registralmente como Liliam del Carmen Pérez de Sandigo Defuncion: Tomo:10000 Folio:146 Partida:146	UBICACION: Costado norte del parque del Diria 895.21m al N-E y 168.67m al N-E. Municipio del Diria. Departamento de Granada.	Ejecuta: Ing.Bosco Javier Morgan Lic. Catastral: BMM100426 Cel: 8883-7568 Email: ingmorgan73@gmail.com	
Solicitante: Carmen Vanecia Sandigo Perez cedula : 204-160769-0000D	ÁREA= 43,581.50m²= 61,816.65 vrs2= 6.18 Mnz — Escala: 1 /1,000	Fecha: 09 de enero del 2026	

ESPACIO PARA ESQUELA

0,313,682

-.T E S T I M O N I O.-

"ESCRITURA CIENTO SESENTA Y SIETE. PROTOCOLO TRECE.-COMPRA-VENTA DE INMUEBLE.- En la ciudad de Granada, a las once de la mañana del dia veintiocho de Agosto de mil novecientos ochenta.-Ante mí, MARIO CASTILLO IBARGUEN, Abogado y Notario Público, de este domicilio y residencia, autorizado por la Corte Suprema de Justicia para cartular en el quinquenio que vence el nueve de Marzo de mil novecientos ochenta y tres; y en presencia de los testigos instrumentales, idóneos, de mi conocimiento personal de lo cual doy fe y que al final nominaré, comparecen los señores HERNALDO ALVAREZ ALEMAN, casado, Mecánico, del domicilio de Masaya, de tránsito por esta ciudad y JOSE RAMON CASTILLO MONTIEL, casado, carpintero, de este domicilio, los dos mayores de edad, a quienes doy fe de conocer personalmente, de que tienen la cppacidad legal necesaria para obligarse y contratar y actuando el segundo en su propio nombre y representacion y el primero en nombre y representacion de su hermana IRMA ALVAREZ DE PACHECO, quien es mayor de edad, viuda, de oficios domesticos y con domicilio en San Francisco, Estado de California de los Estados Unidos de Norteámerica; Personería que acredita el Señor Alvarez Aleman con el Poder Generalisimo, que yo, el Notario, doy fe de tener a la vista y que literalmente dice; "Testimonio" Escritura Número Ochenta.-PODER GENERALISIMO.- En la ciudad de San Francisco, California, Estados Unidos de Norte América, a la una de la tarde del dia veinticinco de Junio de mil novecientos ochenta.-Ante mí, AURA L. BETETA, Consul General de la Republica de Nicaragua en esta ciudad, con domicilio y residencia en la misma, actuando en el Protocolo que lleva este Consulado General a mi cargo, con funciones de Notario Público que me otorgan las Leyes de Nicaragua y ante los testigos instrumentales, idóneos y de mi conocimiento personal que a la conclusión de esta escritura nominaré; Comparece la Señora IRMA PACHECO, mayor de edad, viuda, costurera, nicaraguense, con