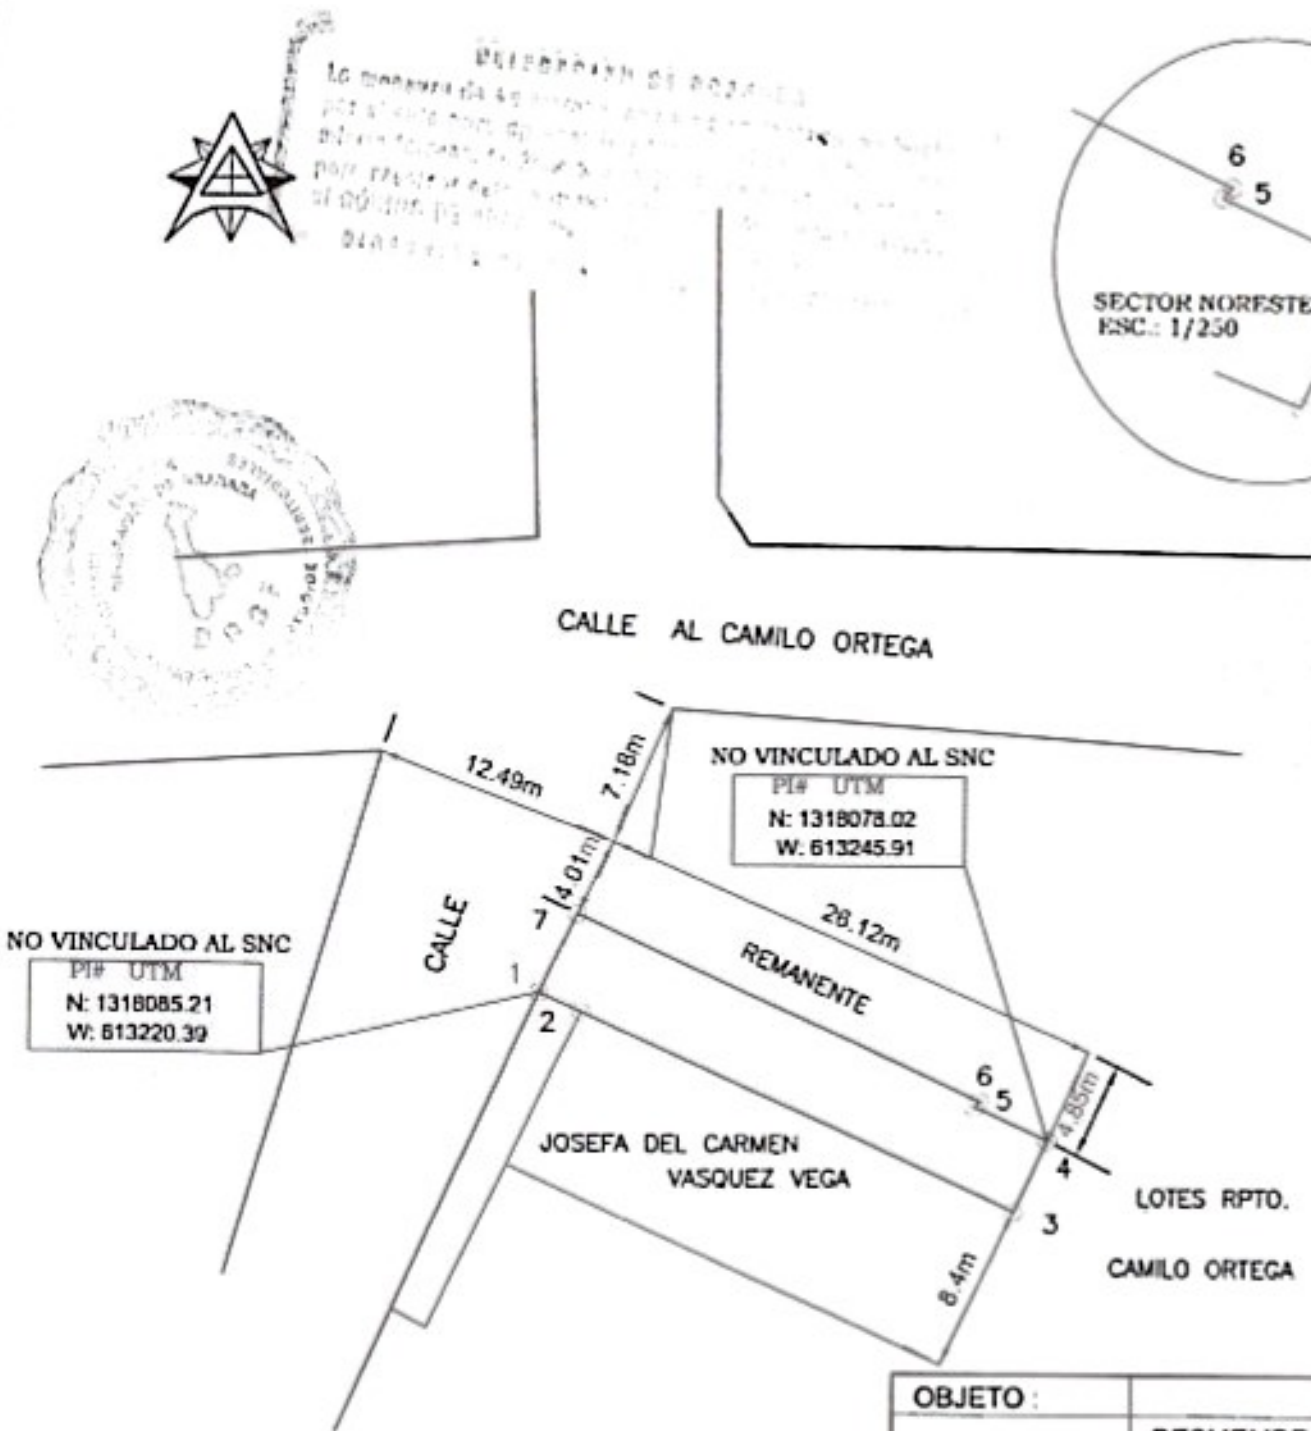

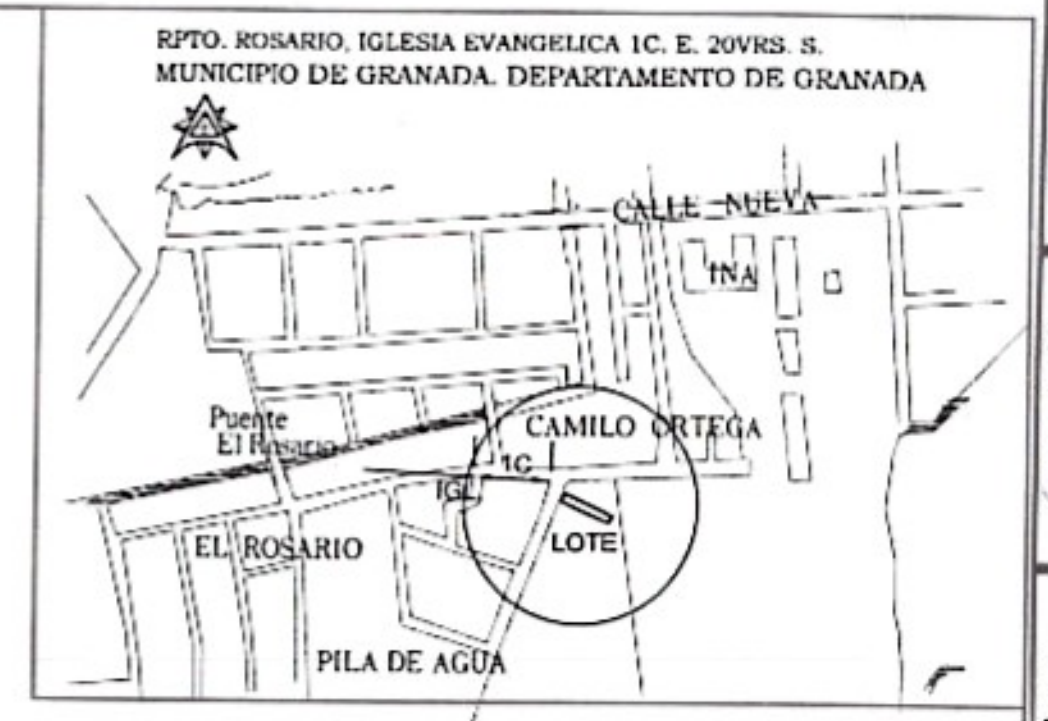

LADO EST	LADO PV	RUMBO	DISTANCIA	V	COORDENADAS Y	COORDENADAS X
				1	1,318,085.21	613,220.39
1	2	S 65°47'10" E	2.31	2	1,318,084.26	613,222.50
2	3	S 65°47'10" E	23.82	3	1,318,074.49	613,244.22
3	4	N 25°38'37" E	3.91	4	1,318,078.02	613,245.91
4	5	N 66°16'26" W	4.06	5	1,318,079.65	613,242.20
5	6	N 44°15'30" E	0.36	6	1,318,079.91	613,242.45
6	7	N 65°27'49" W	22.17	7	1,318,089.11	613,222.28
7	1	S 25°49'31" W	4.34	1	1,318,085.21	613,220.39

SUPERFICIE = 110.08 m2

OBJETO :	DESMEMBRACION	DATOS REGISTRALES		ESC. 1/ 500
ENAJENANTE:	JACQUELINE AUXILIADORA VASQUEZ CED.: 201-210672-0006V	FINCA:	22,735	14-ene-22
	CC JACKELINE AUXILIADORA VASQUEZ VEGA	TOMO:		TOPOGRAFO AUTORIZADO:
	RPTO. ROSARIO, IGLESIA EVANGELICA 1C. E. 20VRS. S.		338	ROBERTO JOSE ACEVEDO RODRIGUEZ
ADQUIRENTE:	JOSEFA DEL CARMEN VASQUEZ VEGA CED.: 203-180457-0000L	FOLIO :		Licencia Catastral RAR100710
	RPTO. ROSARIO, IGLESIA EVANGELICA 1C. E. 20VRS. S.		109	Cedula. 201-081051-0004F
N° . CATASTRAL:	3051-4-05-097-NC	ASIENTO:		Avenida 14 de Septiembre.
DIRECCION DE INMUEBLE:	RPTO. ROSARIO, IGLESIA EVANGELICA 1C. E. 20VRS. S.		1	E.Chamorro 1 al Sur
GRANADA	MUNICIPIO DE GRANADA DEPARTAMENTO DE GRANADA			acv2just1@gmail.com
				TEL: 881-1174 GRANADA

Transacción	Cudoc	Objeto Plano	Área (m²)	No. Lote
T-3NA1LU-001	0006247	DESMEMBRACION	110.08	
Parcela Objeto	63113820272417		Documento	W8BJZT3
No. Licencia: RAR100710	Fecha Aprobación: 1/2/2022		Fecha Vencimiento: 1/2/2023	

CUADRO DE CONSTRUCCION DEL POLIGONO FISICO

LADO	RUMBO	DISTANCIA	AZIMUT	VERT.	ANG.INT.	Y	X	COLINDANTE
1-2	S 65°47'10" E	2.31	114°12'50"	1	88°23'19"	1,318,085.21	613,220.39	X
2-3	S 65°47'10" E	23.82	114°12'50"	2	180°0'0"	1,318,084.26	613,222.50	X
3-4	N 25°38'37" E	3.91	25°38'37"	3	91°25'47"	1,318,074.49	613,244.22	X
4-5	N 66°16'26" W	4.06	293°43'34"	4	88°4'56"	1,318,078.02	613,245.91	X
5-6	N 44°15'30" E	0.36	44°15'30"	5	290°31'56"	1,318,079.65	613,242.20	X
6-7	N 65°27'49" W	22.17	294°32'11"	6	70°16'41"	1,318,079.91	613,242.45	X
7-1	S 25°49'31" W	4.34	205°49'31"	7	91°17'20"	1,318,089.11	613,222.28	X

SUPERFICIE = 110.08 m2

OBJETO :		DATOS REGISTRALES		ESC. 1/ 500
	DESMEMBRACION	FINCA:		14-ene-22
ENAJENANTE:	JACQUELINE AUXILIADORA VASQUEZ CED.: 201-210672-0006V		22,735	TOPOGRAFO AUTORIZADO.
	CC JACKELINE AUXILIADORA VASQUEZ VEGA	TOMO:		ROBERTO JOSE ACEVEDO RODRIGUEZ
	RPTO. ROSARIO, IGLESIA EVANGELICA 1C. E. 20VRS. S.		338	Licencia Catastral RAR100710 Cedula: 201-081051-0004F Avenida 14 de Septiembre E.Chamorro 1 al Sur acv2just1@gmail.com TEL. 887-11741 GRANADA
ADQUIRENTE:	JOSEFA DEL CARMEN VASQUEZ VEGA CED.: 203-180457-0000L	FOLIO :		
	RPTO. ROSARIO, IGLESIA EVANGELICA 1C. E. 20VRS. S.		109	
N°. CATASTRAL:	3051-4-05-097-NC	ASIENTO:		
DIRECCION DE INMUEBLE	RPTO. ROSARIO, IGLESIA EVANGELICA 1C. E. 20VRS. S.		1	
GRANADA	MUNICIPIO DE GRANADA DEPARTAMENTO DE GRANADA.			

SERIE "H"

No 9596754

DIECISIETE CÓRDOBAS

TESTIMONIO. -

ESCRITURA PÚBLICA NÚMERO VEINTE (20).- PROTOCOLO NÚMERO SEIS (06).- RECTIFICACIÓN DE ASIENTO REGISTRAL.- En la ciudad de Granada, a las ocho de la mañana del día tres de Julio del año dos mil veintidós.- **ANTE MI: FELIX ANTONIO CARRILLO MOLINA**, Abogado y Notario Público de la República de Nicaragua, de este domicilio y residencia, debidamente autorizado por la Excelentísima Corte Suprema de Justicia para ejercer el Notariado en un quinquenio que finalizara el día veintisiete de Julio del año dos mil veintidós, comparece la señora **JACQUELINE AUXILIADORA VÁSQUEZ conocida Registralmente como JACKELINE AUXILIADORA VASQUEZ VEGA**, mayor de edad, soltera, ama de casa, de este domicilio, identificada con cedula de identidad número: dos, cero, uno, guion, dos, uno, cero, seis, siete, dos, guion, cero, cero, cero, seis, letra "V" (201-210672-0006V). Doy fe de conocer personalmente a la compareciente y de haber tenido a la vista el documento de identidad relacionado, así como de que a mi juicio la compareciente tiene la capacidad legal civil, necesaria para obligarse y contratar y en especial la requerida para este acto, en el que actúa en su propio nombre e interés. En tal carácter expresa la señora **JACQUELINE AUXILIADORA VÁSQUEZ conocida Registralmente como JACKELINE AUXILIADORA VASQUEZ VEGA**, y dice: **PRIMERA: (RELACIÓN DE DOMINIO):** Que es dueña en dominio y posesión según Titulo de Dominio número 4.13.01-0327 y escritura pública número doscientos cincuenta y ocho (258), Protocolo número veinte (20), denominada Aceptación, autorizada en la ciudad de Granada a las dos de la tarde del día catorce de junio del año mil cuatro, ante los oficios notariales del Licenciado **Rafael Antonio Gutiérrez Figueroa**, de un bien inmueble de naturaleza urbana, ubicada en el Reparto El Rosario, de esta ciudad de Granada, siendo el Lote número cuarenta y siete (47), bloque P, con un área de **doscientos veintidós punto setenta y cuatro Metros Cuadrados (222.74 Mts²)** equivalentes a **trescientos dieciocho punto setenta y cuatro varas cuadradas (318.74 vrs²)**, comprendido dentro de los siguientes linderos y medidas particulares: **NORTE:** Lote número 48-P, con veinticinco punto noventa metros (25.90 mts), **SUR:** Lote número 46-P, con veinticinco punto noventa metros (25.90 mts), **ESTE:** Reparto Camilo Ortega, con ocho punto cuarenta y cinco metros (8.45 mts) y **OESTE:** calle, con ocho punto setenta y cinco metros (8.75 mts); la que se encuentra debidamente inscrita con el **Número de finca:** veintidós mil setecientos treinta y cinco (22,735), **Tomo:** trescientos treinta y ocho (338), **Folios:** ciento nueve y ciento diez (109-110) **Asientos:** primero y segundo (1°-2°), Columna de inscripciones, Sección de Derechos Reales, Libro de

ENTREGADO 22 JUL 2022 2:50 pm

102988 7/7/22 289201

VALE DIECISIETE CÓRDOBAS

SERIE "H"
No9596755

adjunto al presente trámite cedulas de identidad.- C) **SEÑORA REGISTRADORA PÚBLICA DE LA PROPIEDAD INMUEBLE Y MERCANTIL DE ESTE DEPARTAMENTO DE GRANADA**, habiendo cumplido con los requisitos que solicita la Ley para poder rectificar el asiento registral, le **SOLICITO** a su autoridad sus buenos oficios a fin de que **PROCEDA A RECTIFICAR EL ASIENTO REGISTRAL** detallado en la cláusula primera del presente documento y se tenga a nombre legal como **JACQUELINE AUXILIADORA VÁSQUEZ**, a como aparece en mi cedula de identidad ciudadana y demás documentos que adjunto a la presente Escritura Pública.- Continua hablando la señora **JACQUELINE AUXILIADORA VÁSQUEZ conocida Registralmente como JACKELINE AUXILIADORA VASQUEZ VEGA** y dice: **TERCERA: (ACEPTACIÓN):** Que en los términos anteriormente relacionados y en el carácter en la que comparece **ACEPTA** dicha Rectificación de Asiento Registral y solicita a la señora Registradora Pública de la Propiedad Inmueble y Mercantil de este Departamento de Granada, haga inscribir la presente Escritura Pública y proceda a rectificar el nombre y apellido en el asiento anteriormente señalado.- Así se expresó la compareciente bien instruida por mí, el Notario, acerca del objeto, valor y trascendencias legales de este acto; de las cláusulas generales que aseguran su validez, de las especiales que contiene y de las que envuelven renuncias y estipulaciones implícitas y explícitas y la necesidad de su inscripción de este instrumento en el Registro competente.- Y leída que fue por mí, el Notario, integramente la presente escritura a los comparecientes estos la encuentran conforme, aprueban, ratifican y firman junto conmigo, el Notario, que doy fe de todo lo relacionado.- (f). Legible. Jacqueline Vásquez.- (f). Ilegible. José Erasmo Ríos.- (f). legible. José R. Talavera.- (f). Ilegible. Félix Antonio Carrillo Molina, Notario Público.- ==========

PASO ANTE MI: Del Reverso del folio número trece al reverso del folio número catorce, de mi **PROTOCOLO NÚMERO SEIS, SERIE "I", números "623629" "743179"**, que llevó en el presente año, y a solicitud de la señora **JACQUELINE AUXILIADORA VÁSQUEZ**, Libro este Primer **TESTIMONIO, SERIE "H", números "9596754" "9596755"**, en dos hojas útiles de Papel Sellado de Ley, las que firmo, rubrico y sello, todo en la ciudad de Granada, a las nueve de la mañana del día tres de Julio del año dos mil veintidós.-

LIC. FELIX ANTONIO CARRILLO MOLINA

ABOGADO Y NOTARIO PÚBLICO