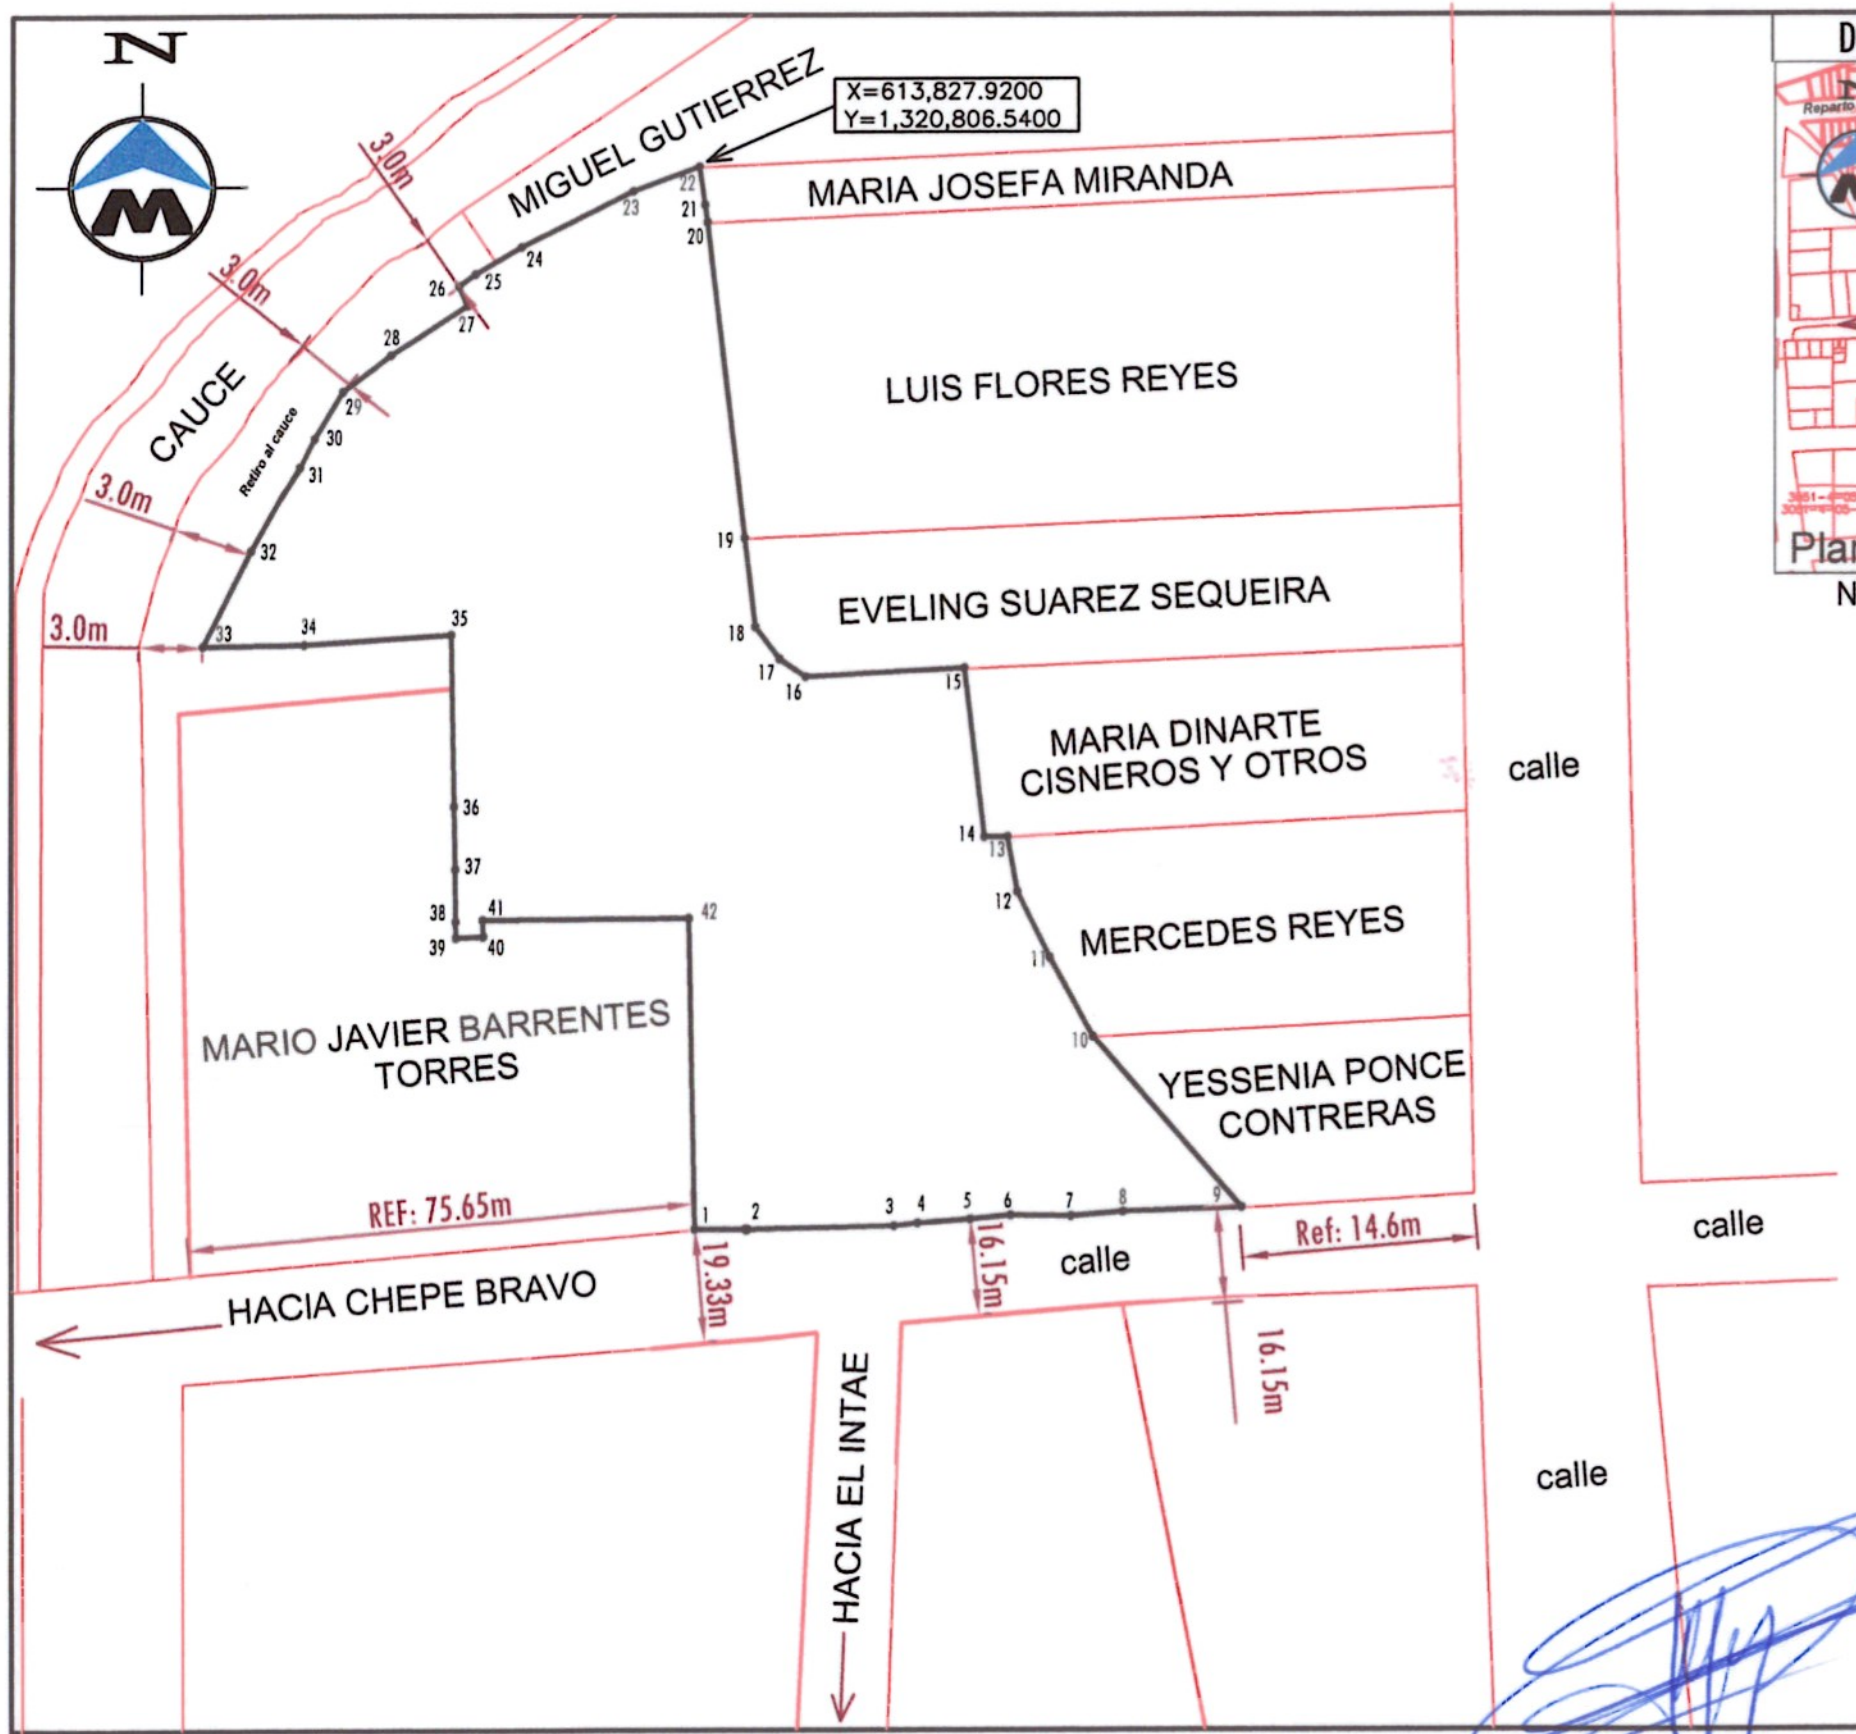

DEPARTAMENTO DE GRANADA MUNICIPIO DE GRANADA

Planta de Ubicacion Sin Escala

Numero NAC:63123076988124 / 63123087061514

COORDENADAS NO VINCULADAS A LA RED GEODESICA DE NICARAGUA

CUADRO DE CONSTRUCCION

LADO EST	LADO PV	RUMBO	DISTANCIA	V	COORDENADAS Y	COORDENADAS X
				1	1,320,648.2500	613,827.1200
1	2	N 90°00'00" E	7.810	2	1,320,648.2500	613,834.9300
2	3	N 88°40'36.56" E	22.086	3	1,320,648.7600	613,857.0100
3	4	N 84°17'21.86" E	3.517	4	1,320,649.1100	613,860.5100
4	5	N 85°07'17.80" E	7.879	5	1,320,649.7800	613,868.3800
5	6	N 84°51'52.79" E	6.145	6	1,320,650.3300	613,874.4800
6	7	S 89°15'06.81" E	9.191	7	1,320,650.2100	613,883.6700
7	8	N 85°20'20.62" E	7.876	8	1,320,650.8500	613,891.5200
8	9	N 87°59'54.13" E	17.751	9	1,320,651.4700	613,909.2600
9	10	N 40°57'56.41" W	33.770	10	1,320,676.9700	613,887.1200
10	11	N 29°28'15.85" W	13.496	11	1,320,688.7200	613,880.4800
11	12	N 26°39'32.05" W	10.921	12	1,320,698.4800	613,875.5800
12	13	N 10°01'40.47" W	8.327	13	1,320,706.6800	613,874.1300
13	14	S 89°20'15.54" W	3.460	14	1,320,706.6400	613,870.6700
14	15	N 06°46'51.52" W	25.406	15	1,320,731.6700	613,867.6700
15	16	S 86°51'37.22" W	23.736	16	1,320,730.5700	613,843.9700
16	17	N 55°12'20.35" W	4.749	17	1,320,733.2800	613,840.0700
17	18	N 38°11'59.67" W	6.032	18	1,320,738.0200	613,836.3400
18	19	N 06°40'55.90" W	13.320	19	1,320,751.2500	613,834.7900
19	20	N 06°53'49.35" W	47.383	20	1,320,798.2900	613,829.1000
20	21	N 08°11'27.10" W	2.667	21	1,320,800.9300	613,828.7200
21	22	N 08°06'56.89" W	5.667	22	1,320,806.5400	613,827.9200
22	23	S 70°17'44.81" W	10.707	23	1,320,802.9300	613,817.8400
23	24	S 63°54'00.33" W	18.730	24	1,320,794.6900	613,801.0200
24	25	S 59°57'04.02" W	7.946	25	1,320,790.7100	613,794.1400
25	26	S 53°14'33.07" W	3.058	26	1,320,788.8800	613,791.6900
26	27	S 22°33'53.52" E	3.205	27	1,320,785.9200	613,792.9200
27	28	S 57°24'56.02" W	13.648	28	1,320,778.5700	613,781.4200
28	29	S 52°55'36.94" W	9.024	29	1,320,773.1300	613,774.2200
29	30	S 31°48'47.31" W	8.214	30	1,320,766.1500	613,769.8900
30	31	S 28°40'41.26" W	4.730	31	1,320,762.0000	613,767.6200
31	32	S 29°25'45.24" W	14.409	32	1,320,749.4500	613,760.5400
32	33	S 26°44'34.58" W	15.845	33	1,320,735.3000	613,753.4100
33	34	N 89°18'23.31" E	14.871	34	1,320,735.4800	613,768.2800
34	35	N 86°13'24.56" E	22.318	35	1,320,736.9500	613,790.5500
35	36	S 01°01'48.82" E	25.564	36	1,320,711.3700	613,791.0100
36	37	S 01°05'49.27" E	9.402	37	1,320,701.9700	613,791.1900
37	38	S 00°43'57.51" E	7.821	38	1,320,694.1500	613,791.2900
38	39	S 00°56'21.09" E	2.440	39	1,320,691.7100	613,791.3300
39	40	N 86°30'38.43" E	4.108	40	1,320,691.9600	613,795.4300
40	41	N 01°52'12.79" W	2.451	41	1,320,694.4100	613,795.3500
41	42	N 89°38'56.22" E	31.011	42	1,320,694.6000	613,826.3600
42	1	S 00°56'21.82" E	46.356	1	1,320,648.2500	613,827.1200

SUPERFICIE = 9,878.211 m2

Objeto Lev: FUSION	Numero NAC:63123076988124 / 63123087061514		Firma:
Propietarios: Juan Maria Osorto Villatoro Pasaporte # :B01969338	Ubicacion: Reparto Bartolome # 2 del INTAE 5c al norte Municipio de Granada, Departamento de Granada.		Ejecuta: Ing.Bosco Javier Morgan Lic. Catastral: BMM100426 Cel: 8883-7568 Email: ingmorgan73@gmail.com SERVICIOS TOPOGRAFICOS
Factor de Escala: 1.418415	Area: 9,878.211 m2 = 14,011.4vrs2	Escala: 1 / 1,500	Fecha: 08 de febrero del 2026

ESPACIO PARA ESQUELA

MORGAN
Servicios Topograficos
Ing Bosco Javier Morgan
Lic Catastral: BMM100426
Cel: 8883 7568 T

COORDENADAS NO VINCULADAS A LA RED GEODESICA DE NICARAGUA

CUADRO DE CONSTRUCCION						
LADO		RUMBO	DISTANCIA	V	COORDENADAS	
EST	PV				Y	X
				1	1,320,648.2500	613,827.1200
1	2	N 90°00'00" E	7.810	2	1,320,648.2500	613,834.9300
2	3	N 88°40'36.58" E	22.086	3	1,320,648.7600	613,857.0100
3	4	N 84°17'21.86" E	3.517	4	1,320,649.1100	613,860.5100
4	5	N 85°07'17.80" E	7.879	5	1,320,649.7800	613,868.3600
5	6	N 84°51'52.79" E	6.145	6	1,320,650.3300	613,874.4800
6	7	S 89°15'06.81" E	9.191	7	1,320,650.2100	613,883.6700
7	8	N 85°20'20.62" E	7.876	8	1,320,650.8500	613,891.5200
8	9	N 87°59'54.13" E	17.751	9	1,320,651.4700	613,909.2600
9	10	N 40°57'56.41" W	33.770	10	1,320,676.9700	613,887.1200
10	11	N 29°28'15.85" W	13.496	11	1,320,688.7200	613,880.4800
11	12	N 26°39'32.05" W	10.921	12	1,320,698.4800	613,875.5800
12	13	N 10°01'40.47" W	8.327	13	1,320,706.6800	613,874.1300
13	14	S 89°20'15.54" W	3.460	14	1,320,706.6400	613,870.6700
14	15	N 06°46'51.52" W	25.408	15	1,320,731.8700	613,867.6700
15	16	S 86°51'37.22" W	23.736	16	1,320,730.5700	613,843.9700
16	17	N 55°12'20.35" W	4.749	17	1,320,733.2800	613,840.0700
17	18	N 38°11'59.67" W	6.032	18	1,320,738.0200	613,836.3400
18	19	N 06°40'55.90" W	13.320	19	1,320,751.2500	613,834.7900
19	20	N 06°53'49.35" W	47.383	20	1,320,798.2900	613,829.1000
20	21	N 08°11'27.10" W	2.667	21	1,320,800.9300	613,828.7200
21	22	N 08°06'56.89" W	5.667	22	1,320,806.5400	613,827.9200
22	23	S 70°17'44.81" W	10.707	23	1,320,802.9300	613,817.8400
23	24	S 63°54'00.33" W	18.730	24	1,320,794.6900	613,801.0200
24	25	S 59°57'04.02" W	7.948	25	1,320,790.7100	613,794.1400
25	26	S 53°14'33.07" W	3.058	26	1,320,788.8800	613,791.6900
26	27	S 22°33'53.52" E	3.205	27	1,320,785.9200	613,792.9200
27	28	S 57°24'58.02" W	13.648	28	1,320,778.5700	613,781.4200
28	29	S 52°55'36.94" W	9.024	29	1,320,773.1300	613,774.2200
29	30	S 31°48'47.31" W	8.214	30	1,320,766.1500	613,769.8900
30	31	S 28°40'41.26" W	4.730	31	1,320,762.0000	613,767.6200
31	32	S 29°25'45.24" W	14.409	32	1,320,749.4500	613,760.5400
32	33	S 26°44'34.58" W	15.845	33	1,320,735.3000	613,753.4100
33	34	N 89°18'23.31" E	14.871	34	1,320,735.4800	613,768.2800
34	35	N 86°13'24.58" E	22.318	35	1,320,736.9500	613,790.5500
35	36	S 01°01'48.82" E	25.584	36	1,320,711.3700	613,791.0100
36	37	S 01°05'49.27" E	9.402	37	1,320,701.9700	613,791.1900
37	38	S 00°43'57.51" E	7.821	38	1,320,694.1500	613,791.2900
38	39	S 00°56'21.09" E	2.440	39	1,320,691.7100	613,791.3300
39	40	N 86°30'38.43" E	4.108	40	1,320,691.9600	613,795.4300
40	41	N 01°52'12.79" W	2.451	41	1,320,694.4100	613,795.3500
41	42	N 89°38'56.22" E	31.011	42	1,320,694.6000	613,826.3600
42	1	S 00°56'21.82" E	46.356	1	1,320,648.2500	613,827.1200
SUPERFICIE = 9,878.211 m2						

Firma:

Ejecuta: Ing.Bosco Javier Morgan
Lic. Catastral: BMM100426
Cel: 8883-7568 Email: ingmorgan73@gmail.com
SERVICIOS TOPOGRAFICOS

MORGAN
Servicios Topograficos
Ing Bosco Javier Morgan
Lic Catastral: BMM100426
Cel: 8883 7568