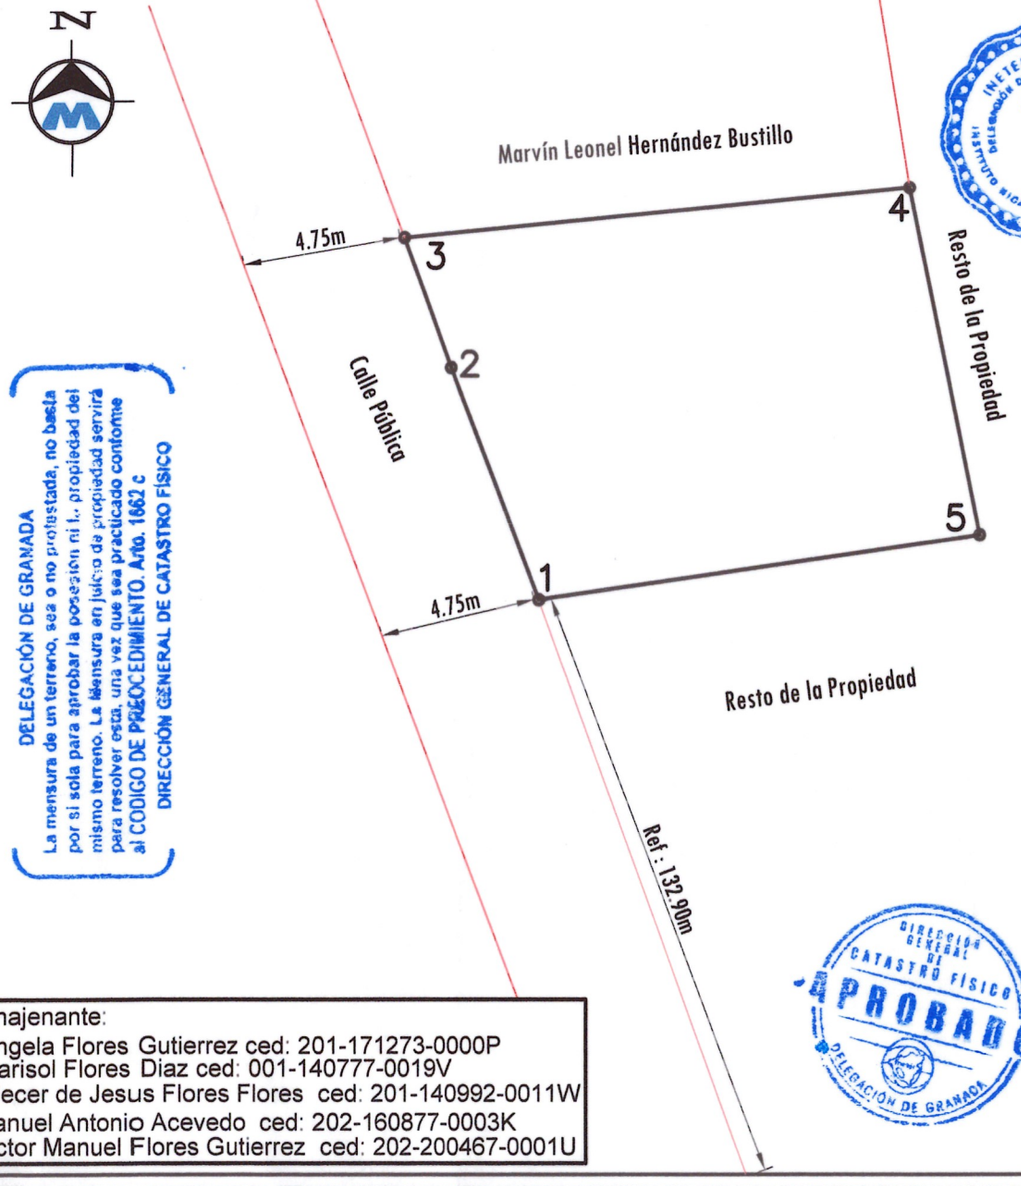

DELEGACIÓN DE GRANADA
La mensura de un terreno, sea o no protestada, no basta por si sola para aprobar la posesión ni la propiedad del mismo terreno. La mensura en juicio de propiedad servirá para resolver esta, una vez que sea practicado conforme al CODIGO DE PROCEDIMIENTO. Arto. 1662 c
DIRECCIÓN GENERAL DE CATASTRO FÍSICO

INETER DELEGACIÓN DE GRANADA DGCF INSTITUTO NICARAGÜENSE DE ESTUDIOS TERRITORIALES

DIRECCIÓN GENERAL DE CATASTRO FÍSICO APROBADO DELEGACIÓN DE GRANADA

MUNICIPIO DE NANDAIME. DEPARTAMENTO DE GRANADA

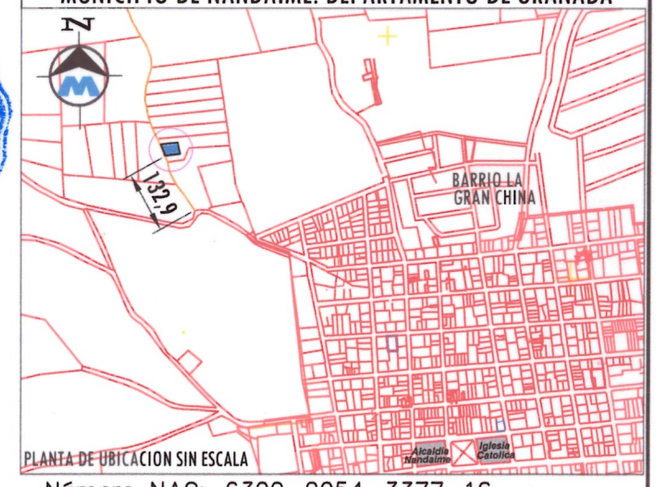

Número NAC: 6300–2054–3377–16

COORDENADAS NO VINCULADAS A LA RED GEODESICA DE NICARAGUA

CUADRO DE CONSTRUCCION

LADO EST	LADO PV	RUMBO	DISTANCIA	V	COORDENADAS Y	COORDENADAS X
				1	1,300,417.3750	602,484.7964
1	2	N 20°59'44.30" W	17.798	2	1,300,433.9912	602,478.4195
2	3	N 20°21'08.95" W	9.907	3	1,300,443.2793	602,474.9740
3	4	N 84°28'09.49" E	36.832	4	1,300,446.8291	602,511.6342
4	5	S 11°41'58.24" E	25.350	5	1,300,422.0055	602,516.7747
5	1	S 81°45'38.45" W	32.312	1	1,300,417.3750	602,484.7964

SUPERFICIE = 902.063 m2

Enajenante:
Angela Flores Gutierrez ced: 201-171273-0000P
Clarisol Flores Diaz ced: 001-140777-0019V
Eliecer de Jesus Flores Flores ced: 201-140992-0011W
Manuel Antonio Acevedo ced: 202-160877-0003K
Victor Manuel Flores Gutierrez ced: 202-200467-0001U

Objeto: Cesacion de Comunidad	Número NAC: 6300–2054–3377–16		FIRMA:
Enajenante: Arriba reflejados	Dirección: Cmca. Monte Grande Occidental, Escuela Carmela Noguera, 1/2C. Oeste y 270 m Norte. Municipio de Nandaime, Departamento de Granada.		Ejecuta: Ing.Bosco Javier Morgan Lic. Catastral: BMM100426 Cel: 8883-7568 Email: ingmorgan73@gmail.com www.morganconstrucciones.com
Adquiriente: Carmen Cecilia Flores Gutierrez Ced: 081-050272-0000R	Área = 902.063 m2 = 1,279.49 Vrs2	Escala: 1: 500	Fecha: 13 de febrero del 2026

sello MORG Servicios Top Ing Bosco J Lic Catast Cel: 8883 7568

Transacción	Cudoc	Objeto Plano	Área (m²)	No. Lote
T-4CI3L3-001	0042344	DESMEMBRACIÓN	902.06	
Parcela Objeto	6300204483141 7		Documento	W8BZY6Q
No. Licencia: BMM100426	Fecha Aprobación: 2/3/2026		Fecha Vencimiento: 2/3/2027	

COORDENADAS NO VINCULADAS A LA RED GEODESICA DE NICARAGUA

CUADRO DE CONSTRUCCION

LADO		RUMBO	DISTANCIA	V	COORDENADAS	
EST	PV				Y	X
				1	1,300,417.3750	602,484.7964
1	2	N 20°59'44.30" W	17.798	2	1,300,433.9912	602,478.4195
2	3	N 20°21'08.95" W	9.907	3	1,300,443.2793	602,474.9740
3	4	N 84°28'09.49" E	36.832	4	1,300,446.8291	602,511.6342
4	5	S 11°41'58.24" E	25.350	5	1,300,422.0055	602,516.7747
5	1	S 81°45'38.45" W	32.312	1	1,300,417.3750	602,484.7964

SUPERFICIE = 902.063 m2

FIRMA:

Ejecuta: Ing.Bosco Javier Morgan
Lic. Catastral: BMM100426
Cel: 8883-7568 Email: ingmorgan73@gmail.com
www.morganconstrucciones.com

MORGAN
Servicios Topograficos
Ing Bosco Javier Morgan
Lic Catastral: BMM100426
Cel: 8883 7568 T