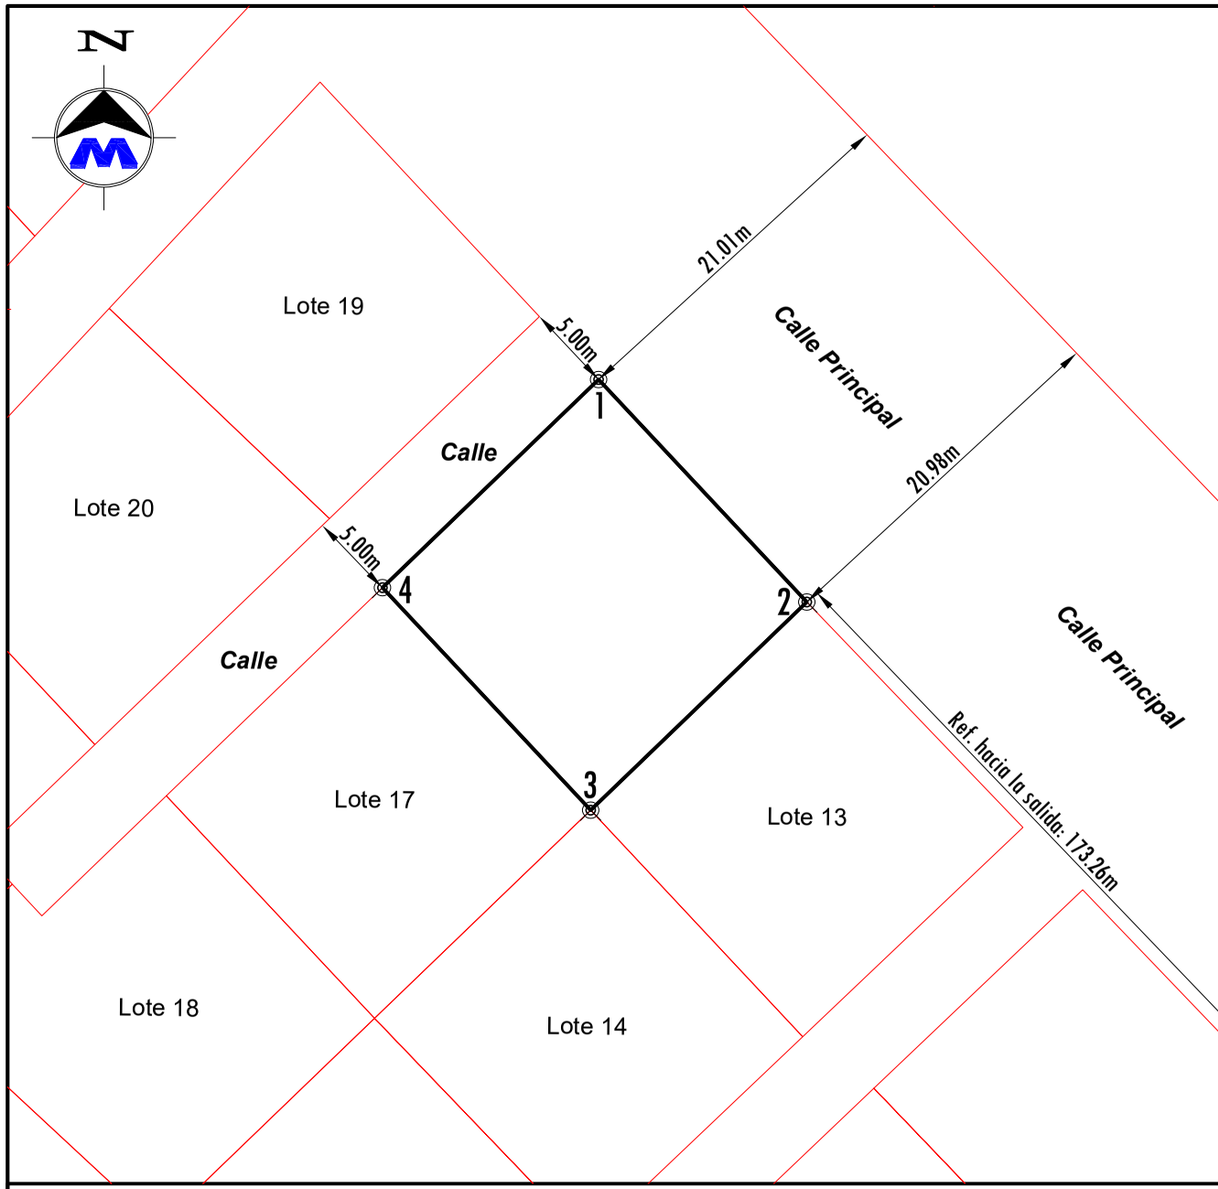

MUNICIPIO DE DIRIOMO. DEPARTAMENTO DE GRANADA.

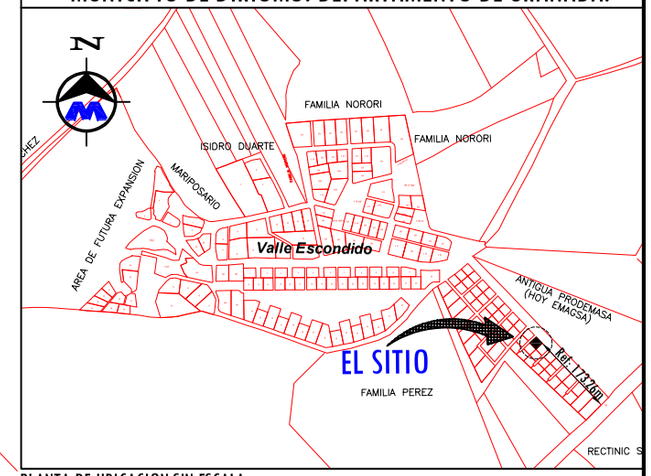

PLANTA DE UBICACION SIN ESCALA

Numero Catastral: 6311-0628-4241-14 (Matriz)

COORDENADAS NO VINCULADAS A LA RED GEODESICA DE NICARAGUA

CUADRO DE CONSTRUCCION

LADO EST	LADO PV	RUMBO	DISTANCIA	V	COORDENADAS Y	COORDENADAS X
				1	1,316,639.4759	610,829.7775
1	2	S 43°05'32.01" E	17.625	2	1,316,626.6050	610,841.8186
2	3	S 46°04'08.92" W	17.360	3	1,316,614.5606	610,829.3161
3	4	N 43°05'32.01" W	17.625	4	1,316,627.4315	610,817.2750
4	1	N 46°04'08.92" E	17.360	1	1,316,639.4759	610,829.7775

SUPERFICIE = 305.946 m2 = 433.958 Vrs

Objeto: Venta Parcial	Número Catastral: 6311-0628-4241-14 (Matriz)	FIRMA:	SELLO
Enajenante: INVERSIONES VALLE ESCONDIDO S.A.	Ubicación: Valle Escondido, Sector Guanacaste, Lote n°16 Municipio de Granada. Departamento de Granada.	Ejecuta: Ing.Bosco Javier Morgan Lic. Catastral: BMM100426 Cel: 8883-7568 Email: ingmorgan73@gmail.com www.morganconstrucciones.com	
Adquirientes: Cindy Auxiliadora Tapia Silva, Ced: 001-251195-0001D Frederick Marcelo Alguera Perez, Ced: 201-151193-0004Y	Área: 305.946 m2 = 433.958Vrs2 — Escala: 1: 400	Fecha: 27 de Noviembre del 2025	

ESPACIO PARA ESQUELA