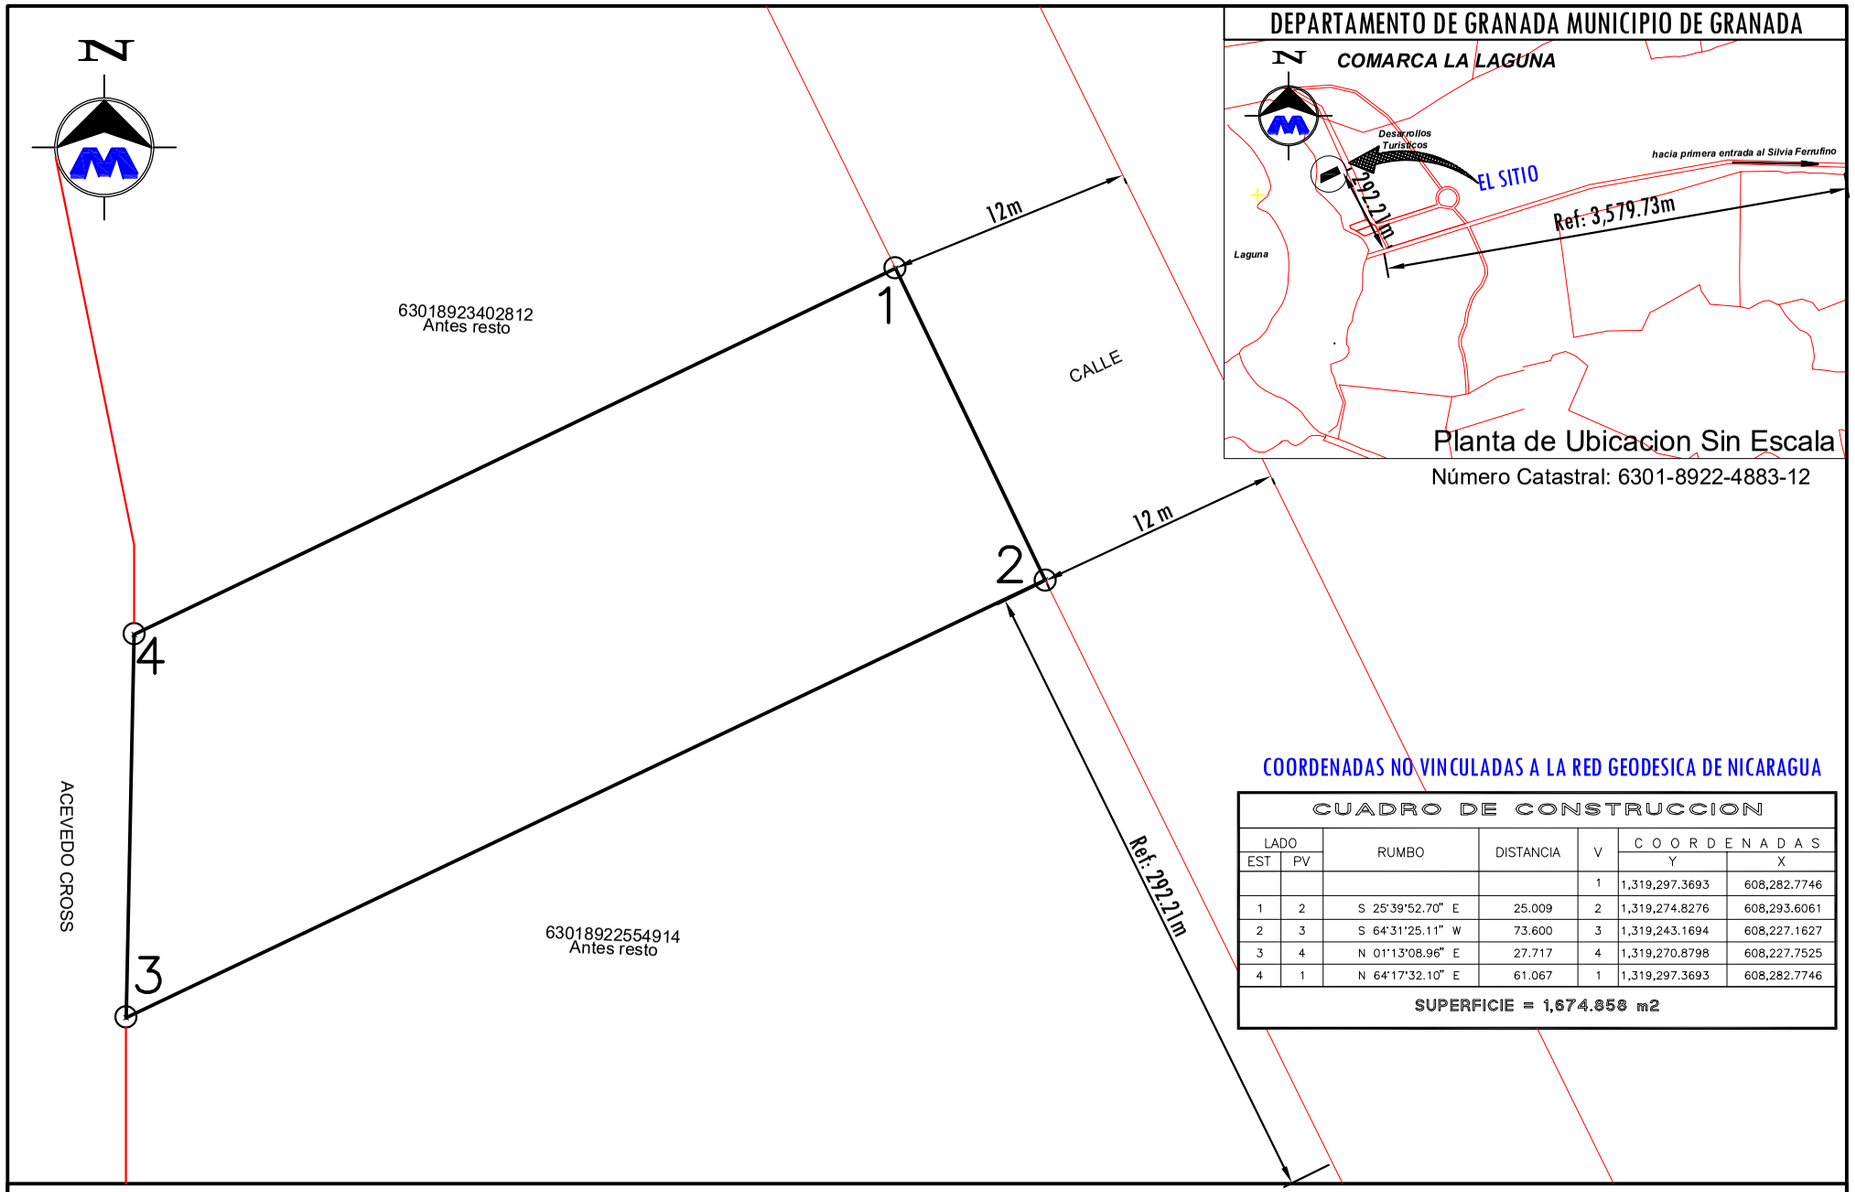

DEPARTAMENTO DE GRANADA MUNICIPIO DE GRANADA

Planta de Ubicacion Sin Escala

Número Catastral: 6301-8922-4883-12

COORDENADAS NO VINCULADAS A LA RED GEODESICA DE NICARAGUA

CUADRO DE CONSTRUCCION

LADO EST	LADO PV	RUMBO	DISTANCIA	V	COORDENADAS Y	COORDENADAS X
				1	1,319,297.3693	608,282.7746
1	2	S 25°39'52.70" E	25.009	2	1,319,274.8276	608,293.6061
2	3	S 64°31'25.11" W	73.600	3	1,319,243.1694	608,227.1627
3	4	N 01°13'08.96" E	27.717	4	1,319,270.8798	608,227.7525
4	1	N 64°17'32.10" E	61.067	1	1,319,297.3693	608,282.7746

SUPERFICIE = 1,674.858 m2

Objeto Lev: VENTA TOTAL	Número Catastral: 6301-8922-4883-12	FIRMA:	SELLO
Enajenante: Brian Edbrooke Davis Pasaporte # 641338019 Nancy Finn Davis conocida como Nancy Finn Chally Pasaporte # 655073411	Ubicación: Comarca La Laguna de la primera entrada del Reparto Silvia Ferrufino 3,579.73m al Oeste y 292.21m al Noroeste. Vistalagos. Municipio de Granada. Depto de Granada.	Ejecuta: Ing.Bosco Javier Morgan Lic. Catastral: BMM100426 Cel: 8883-7568 Email: ingmorgan73@gmail.com servicios topograficos	
Adquiriente: Benjamin Matthias Michael Hass Pasaporte # C74NHC6CV Tilmann Mathias Bohme Pasaporte # C3JCPZNCY	Área: 1,674.858 m2= 2,375.64vrs2 — Escala: 1 / 500	Fecha: 3 de Febrero del 2026	

ESPACIO PARA ESQUELA