## DERROTERO

| LINEA | RUMBO | DIST | Coord. no vinculadas al Sistema Nacional de Coord. |
|---|---|---|---|
| 1-2 | S28°04'51"E | 15.12 | 16P 602893.51, 1313957.62 |
| 2-3 | S63°58'18"W | 37.80 | 16P 602900.63, 1313944.28 |
| 3-4 | N28°04'50"W | 15.12 | 16P 602866.67, 1313927.69 |
| 4-1 | N63°57'53"E | 37.80 | 16P 602859.55, 1313941.03 |

Plano de Ubicación- Scale To Fit

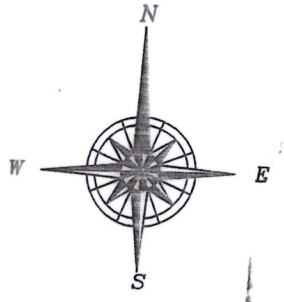


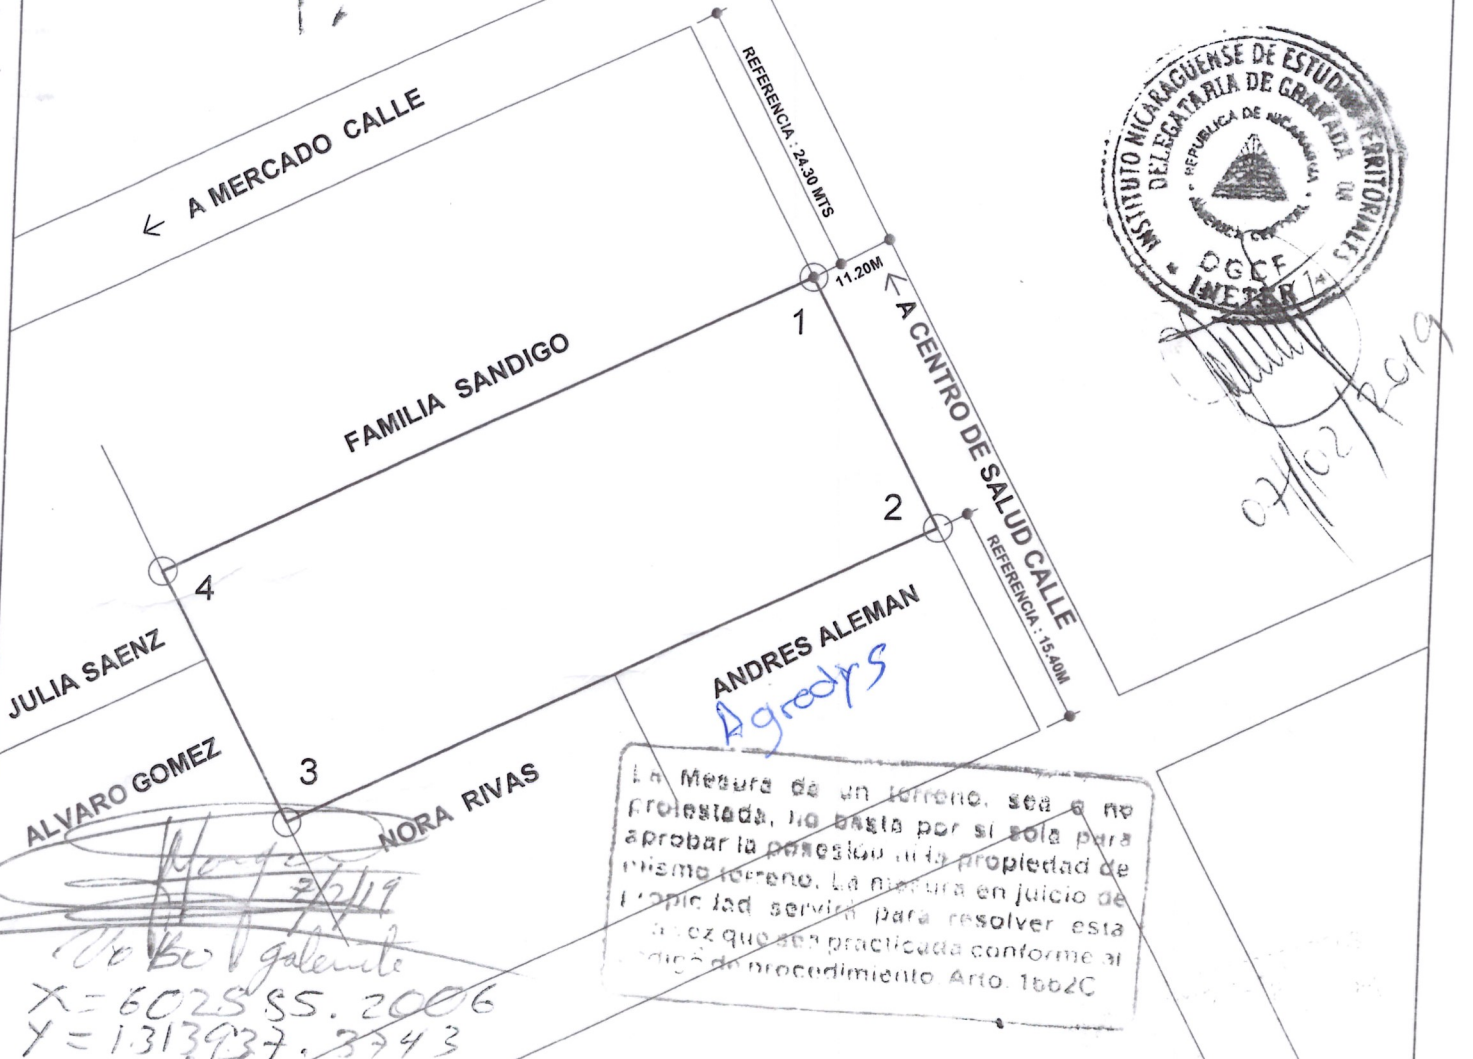


La Medida de un terreno, sea o no protestada, no basta por sí sola para aprobar la posesión de la propiedad de mismo terreno. La medida en juicio de propiedad servirá para resolver esta vez que sea practicada conforme al código de procedimiento Arto. 1662C

INSTITUTO NICARAGÜENSE DE ESTUDIOS TERRITORIALES DELEGATARIA DE GRANADA REPUBLICA DE NICARAGUA DGCF INETER

07/02/2019

Agredys

7/2/19

Vo Bo galente

X = 602855.2006
Y = 1313937.3743

Granada 2951-1-12-082-00800

| | | | |
|---|---|---|---|
| Nº Catastral: 2951-1-12-082-00800 | | | Firma: |
| Levantó: TOP. MARLON POMARES | Calculó: TOP. MARLON POMARES | Revisó: ING. CLARENCE REYES | Lic. Catastral: CRP101115 |
| Objeto: VENTA TOTAL | Área del lote: 0.08 Mz : 571.25 m² = 810.27 v² | | Escala: 1 : 400 |
| Adquiere: VICTOR MANUEL UBILLA | | Dibujó: ING. CLARENCE REYES reyes_clarence@hotmail.com Cell : 8383-3963 | Fecha: 09 DE NOVIEMBRE DEL 2019 |
| Enajena: ANGELITA DEL SOCORRO ORTEGA SANTAMARIA | | Ubicación: DIRIA DE CENTRO DE SALUD 2 ½ C AL SUR, GRANADA-NICARAGUA | |

# HOJA DE CALCULO

Ubicación: DIRIA Dueño: VICTOR MANUEL UBILLA Fecha: miércoles, 09 enero 2019

| LADO | ANGULO | DIST. | RUMBO | LAT. | LONG. | LATC. | LONGC. | COORD X | COORD Y | X1 x Y2 | Y1 x X2 |
|---|---|---|---|---|---|---|---|---|---|---|---|
| 1 | 267°57'16" | 15.12 | S28°04'51"E | -13.3442 | 7.1194 | -13.3442 | 7.1194 | 1313957.6196 | 602893.5120 | 792185878489.6810 | 792168478768.2010 |
| 2 | 272°03'09" | 37.80 | S63°58'18"W | -16.5873 | -33.9662 | -16.5873 | -33.9662 | 1313944.2754 | 602900.6314 | 792133203569.0280 | 792167832769.4320 |
| 3 | 267°56'52" | 15.12 | N28°04'50"W | 13.3402 | -7.1172 | 13.3402 | -7.1172 | 1313927.6881 | 602866.6652 | 792113852152.6510 | 792131246000.6800 |
| 4 | 272°02'43" | 37.80 | N63°57'53"E | 16.5913 | 33.9640 | 16.5913 | 33.9640 | 1313941.0283 | 602859.5480 | 792166521112.6780 | 792131896643.2120 |
| | 1080°00'00" | 105.84 | | 0.0000 | 0.0000 | Error = 0.00 | Prec.= 1/10000 | Área mts² = 571.2566 | Área Mz: | 0.0810 = 810.2789 Vrs² | |

INSTITUTO NICARAGÜENSE DE ESTUDIOS TERRITORIALES (INETER)

Managua, Nicaragua

# DIRECCION GENERAL DE CATASTRO FISICO
## NICARAGUA, C.A
APARTADO POSTAL 2110

13D1902210018

## CERTIFICADO CATASTRAL

No: 13-00899

Amparado en la solicitud #: **13D1902200026**

Solicitado por: **GIOVANNY ANTONIO DIAZ**

La propiedad objeto de certificacion esta catastrada: **Si**

Se extiende el certificado para efectuar: **Venta Total**

**Enajenante(s)**

| Nombre: | Direccion: |
|---|---|
| ANGELITA DEL SOCORRO ORTEGA SANTAMARIA | BO. EL CALVARIO , CHINANDEGA |

**Datos Registrales**

| Finca | Tomo | Folio | Asiento |
|---|---|---|---|
| 15887 | 531 | 28 | 2 |

**Inmueble Matriz**

| Numero Catastral: | Catastrada: | Area m²: | Ubicación: |
|---|---|---|---|
| 2951112082-00800 | S | 571 25 | DE CENTRO SALUD 2 1/2 C S DIRIA - GRANADA |

**Adquiriente(s)**

| Nombre: | Direccion: |
|---|---|
| VICTOR MANUEL UBILLA | BO. SANTA ANA , SUPERMERCADO PALI 1/2 C S CHINANDEGA |

**Inmueble Nuevo**

| Numero Catastral: | Catastrada: | Area m²: | Ubicacion: |
|---|---|---|---|
| 2951112082-00800 | S | 571 | DE CENTRO SALUD 2 1/2 S.C.S. DIRIA GRANADA |

**Observaciones:**

Extendido en: GRANADA el dia: 21 de Febrero del: 2019 a las: 04:26:48 p.m.

Nota: Este Certificado Catastral, es válido por 60 días de conformidad al Arto. 42 de la Ley No. 509, Ley General de Catastro Nacional

Ing. Justo Javier Gutierrez
Delegado de Catastro Fisico - Granada

**A llenarse en el Registro Público:**

Inscrito en la Finca N°: Tomo N°: Folio N°: Asiento N°:

Fecha de Adquisición: Fecha de Inscripción:

Nota: Este Documento no es válido si presenta borrones o enmendaduras

Registro Público