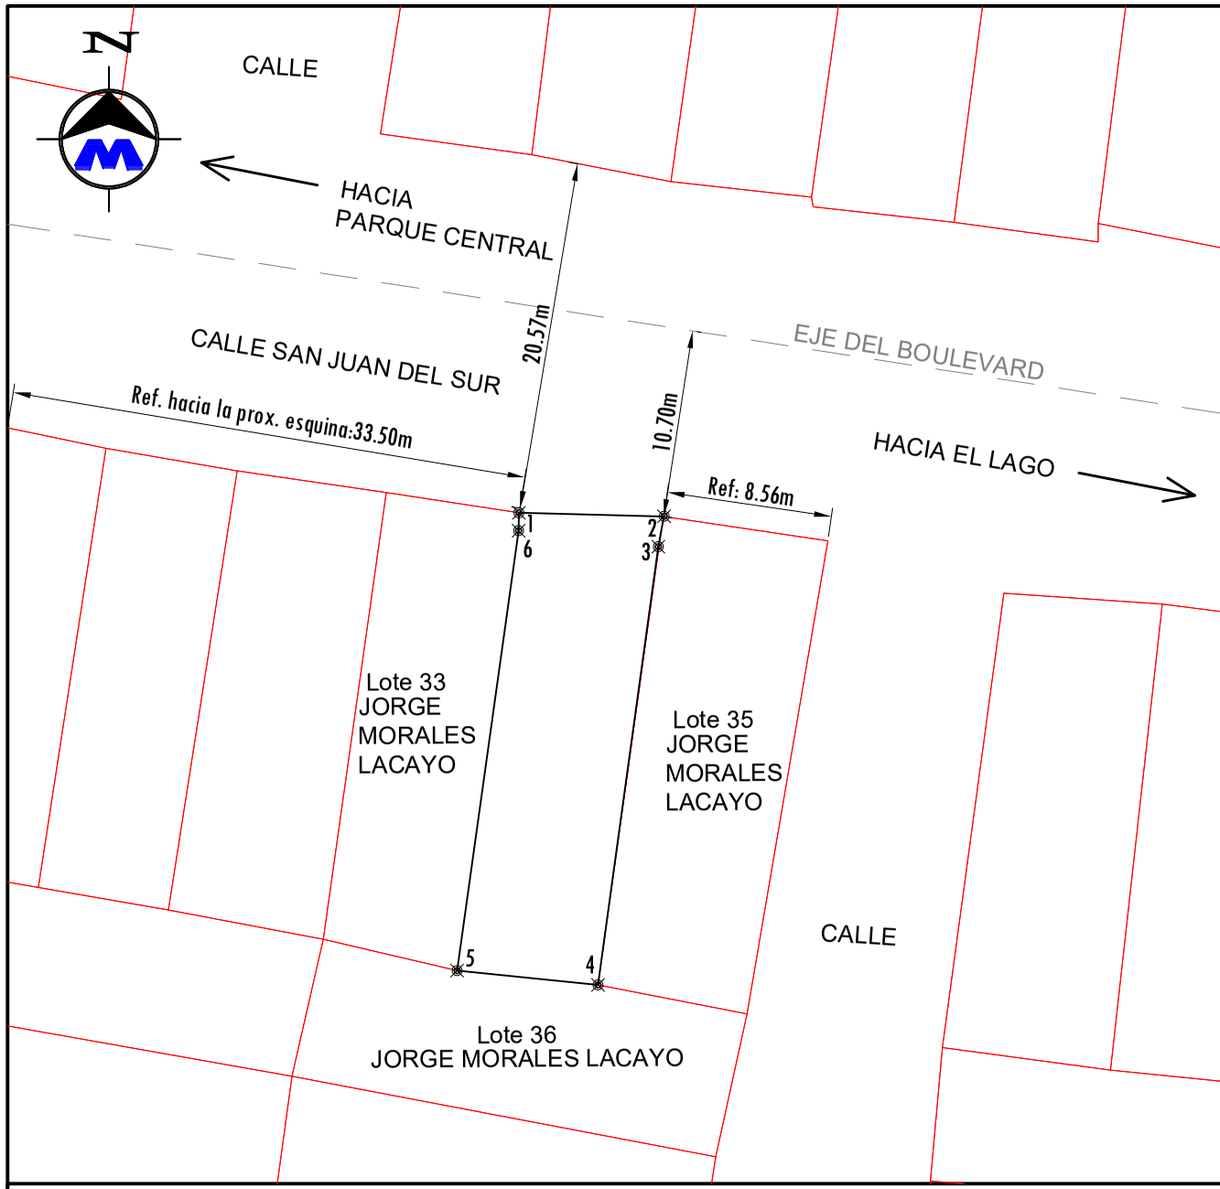

DEPARTAMENTO DE GRANADA MUNICIPIO DE GRANADA

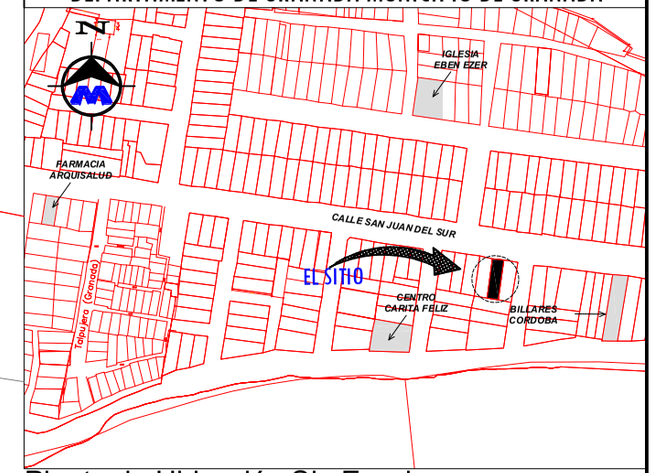

Planta de Ubicación Sin Escala
Número Catastral: 3051-4-05-079-20400

COORDENADAS NO VINCULADAS A LA RED GEODESICA DE NICARAGUA

CUADRO DE CONSTRUCCION

LADO EST	LADO PV	RUMBO	DISTANCIA	V	COORDENADAS Y	COORDENADAS X
				1	1,318,795.3705	614,979.7335
1	2	S 88°29'44.96" E	8.374	2	1,318,795.1507	614,988.1046
2	3	S 10°17'33.83" W	1.775	3	1,318,793.4048	614,987.7875
3	4	S 07°48'48.01" W	25.595	4	1,318,768.0473	614,984.3079
4	5	N 84°11'37.25" W	8.194	5	1,318,768.8762	614,976.1565
5	6	N 07°57'29.36" E	25.700	6	1,318,794.3290	614,979.7147
6	1	N 01°02'09.00" E	1.042	1	1,318,795.3705	614,979.7335

SUPERFICIE = 220.730 m2 = 313.09 Vrs2

Objeto Lev: Mensura Judicial	Número Catastral: 3051-4-05-079-20400		FIRMA:
Propietario: William Tyrone Zambrana Dominguez Ced: 201-240564-00107T	Ubicación: Del Centro Carita Feliz 51.12m al N, 33.50 m al E. Municipio de Granada, Departamento de Granada.		Ejecuta: Ing.Bosco Javier Morgan Lic. Catastral: BMM100426 Cel: 8883-7568 Email: ingmorgan73@gmail.com SERVICIOS TOPOGRAFICOS
Factor de escala: 1.418415	Área: 220.730 m2 = 313.09 Vrs2	Escala: 1 /400	Fecha: 16 de Febrero del 2026

ESPACIO PARA ESQUELA