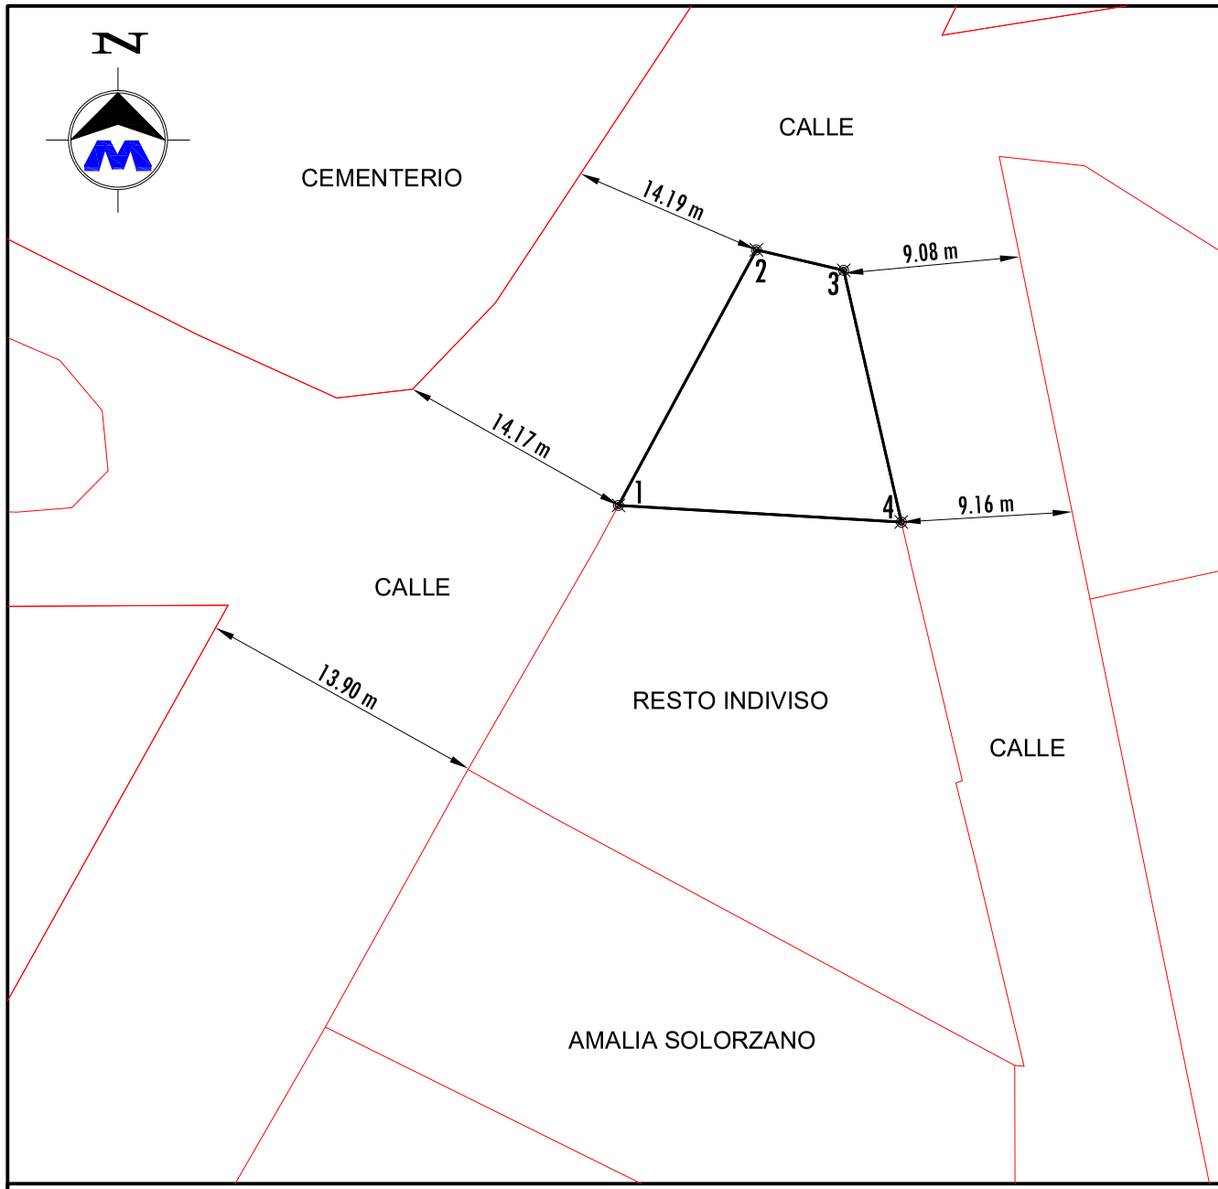

DEPARTAMENTO DE GRANADA MUNICIPIO DE GRANADA

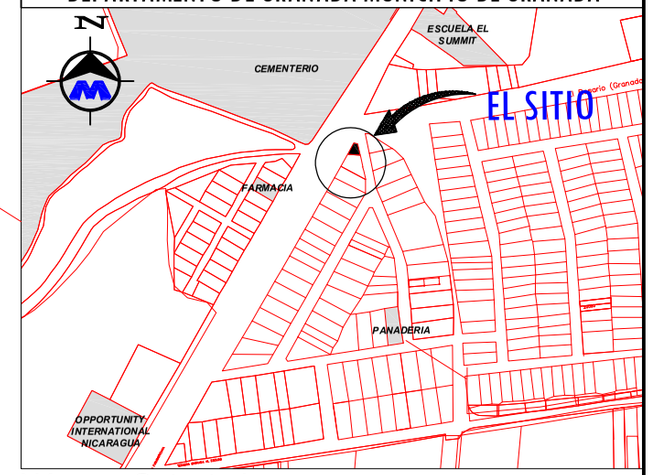

Número Catastral:
3051-4-05-096-00502
Planta de Ubicación Sin Escala

COORDENADAS NO VINCULADAS A LA RED GEODESICA DE NICARAGUA

CUADRO DE CONSTRUCCION

LADO EST	LADO PV	RUMBO	DISTANCIA	V	COORDENADAS Y	COORDENADAS X
				1	1,318,027.0610	612,666.6910
1	2	N 28°19'11.12" E	10.491	2	1,318,036.2965	612,671.6679
2	3	S 76°51'27.45" E	3.240	3	1,318,035.5599	612,674.8227
3	4	S 12°53'31.85" E	9.336	4	1,318,026.4596	612,676.9056
4	1	N 86°37'50.12" W	10.232	1	1,318,027.0610	612,666.6910

SUPERFICIE = 62.253 m2 = 88.30 Vrs2

Objeto Lev: Venta Total de su parte indivisa	Número Catastral: 3051-4-05-096-00502	FIRMA:
Enajenante: Anayancy Pasos Vanega, Ced: 201-250686-0001X	Ubicación: Primera entrada del Escudo, frente al Cementerio de Granada. Municipio de Granada, Departamento de Granada.	Ejecuta: Ing.Bosco Javier Morgan Lic. Catastral: BMM100426 Cel: 8883-7568 Email: ingmorgan73@gmail.com servicios topograficos
Adquiriente: Ovilia del Socorro Arguello Rocha; Ced: 365-241075-0002K	Área: 62.253 m2 = 88.30 Vrs2 — Escala: 1 / 250	Fecha: 2 de Marzo 2026

ESPACIO PARA ESQUELA