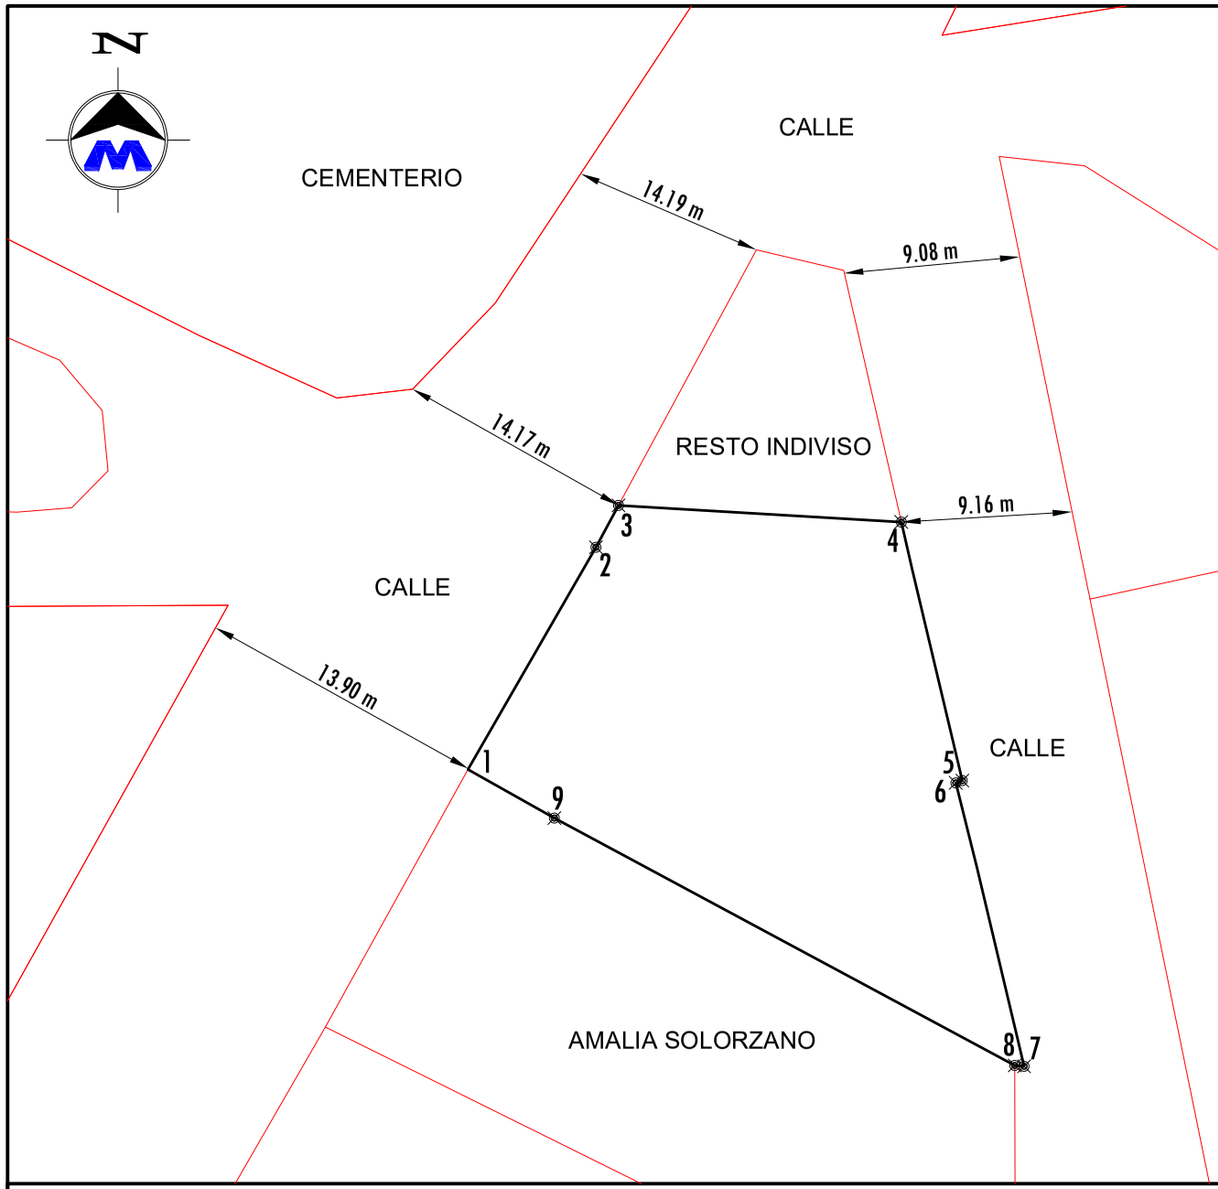

DEPARTAMENTO DE GRANADA MUNICIPIO DE GRANADA

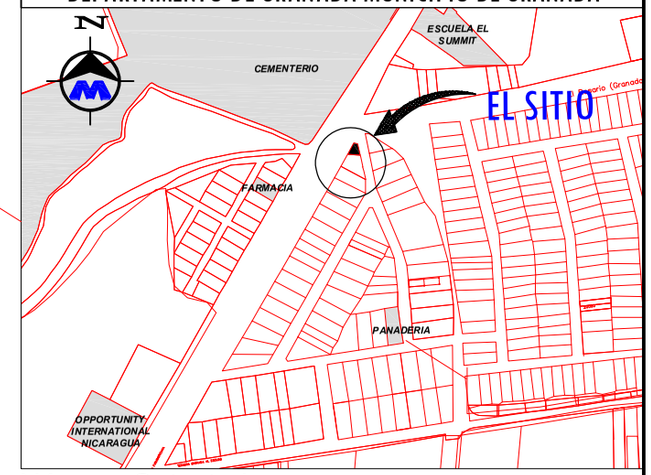

Número Catastral:
3051-4-05-096-00502
Planta de Ubicación Sin Escala

COORDENADAS NO VINCULADAS A LA RED GEODESICA DE NICARAGUA

CUADRO DE CONSTRUCCION

LADO EST	LADO PV	RUMBO	DISTANCIA	V	COORDENADAS Y	COORDENADAS X
				1	1,318,017.5128	612,661.2471
1	2	N 29°56'41.02" E	9.265	2	1,318,025.5411	612,665.8719
2	3	N 28°19'11.12" E	1.726	3	1,318,027.0610	612,666.6910
3	4	S 86°37'50.12" E	10.232	4	1,318,026.4596	612,676.9056
4	5	S 12°53'31.85" E	1.717	5	1,318,024.7859	612,677.2887
5	6	S 13°19'40.33" E	7.894	6	1,318,017.1045	612,679.1084
6	7	S 71°52'03.28" W	0.246	7	1,318,017.0279	612,678.8745
7	8	S 13°59'49.66" E	3.155	8	1,318,013.9663	612,679.6377
8	9	S 13°20'14.09" E	7.388	9	1,318,006.7772	612,681.3420
9	10	N 85°14'34.04" W	0.333	10	1,318,006.8048	612,681.0105
10	11	N 61°43'57.60" W	18.897	11	1,318,015.7540	612,664.3674
11	1	N 60°35'30.03" W	3.582	1	1,318,017.5128	612,661.2471

SUPERFICIE = 226.012 m2 = 320.58 Vrs2

Objeto Lev: Venta Total de su parte indivisa	Número Catastral: 3051-4-05-096-00502	FIRMA:
Enajenante: Moises Perez Martinez; Ced: 329-010752-0000M	Ubicación: Primera entrada del Escudo, frente al Cementerio de Granada. Municipio de Granada, Departamento de Granada.	Ejecuta: Ing.Bosco Javier Morgan Lic. Catastral: BMM100426 Cel: 8883-7568 Email: ingmorgan73@gmail.com servicios topograficos
Adquiriente: Ovilia del Socorro Arguello Rocha; Ced: 365-241075-0002K	Área: 62.253 m2 = 88.30 Vrs2 — Escala: 1 / 250	Fecha: 2 de Marzo 2026

ESPACIO PARA ESQUELA