Transacción	Cudoc	Objeto Plano	Área (m²)	No. Lote
T-46HN46-001	0040997	DESMEMBRACIÓN	49,359.37	
Parcela Objeto	63113555331311		Documento	W8BZ7II
No. Licencia: BMM100426	Fecha Aprobación: 11/12/2025		Fecha Vencimiento: 11/12/2026	

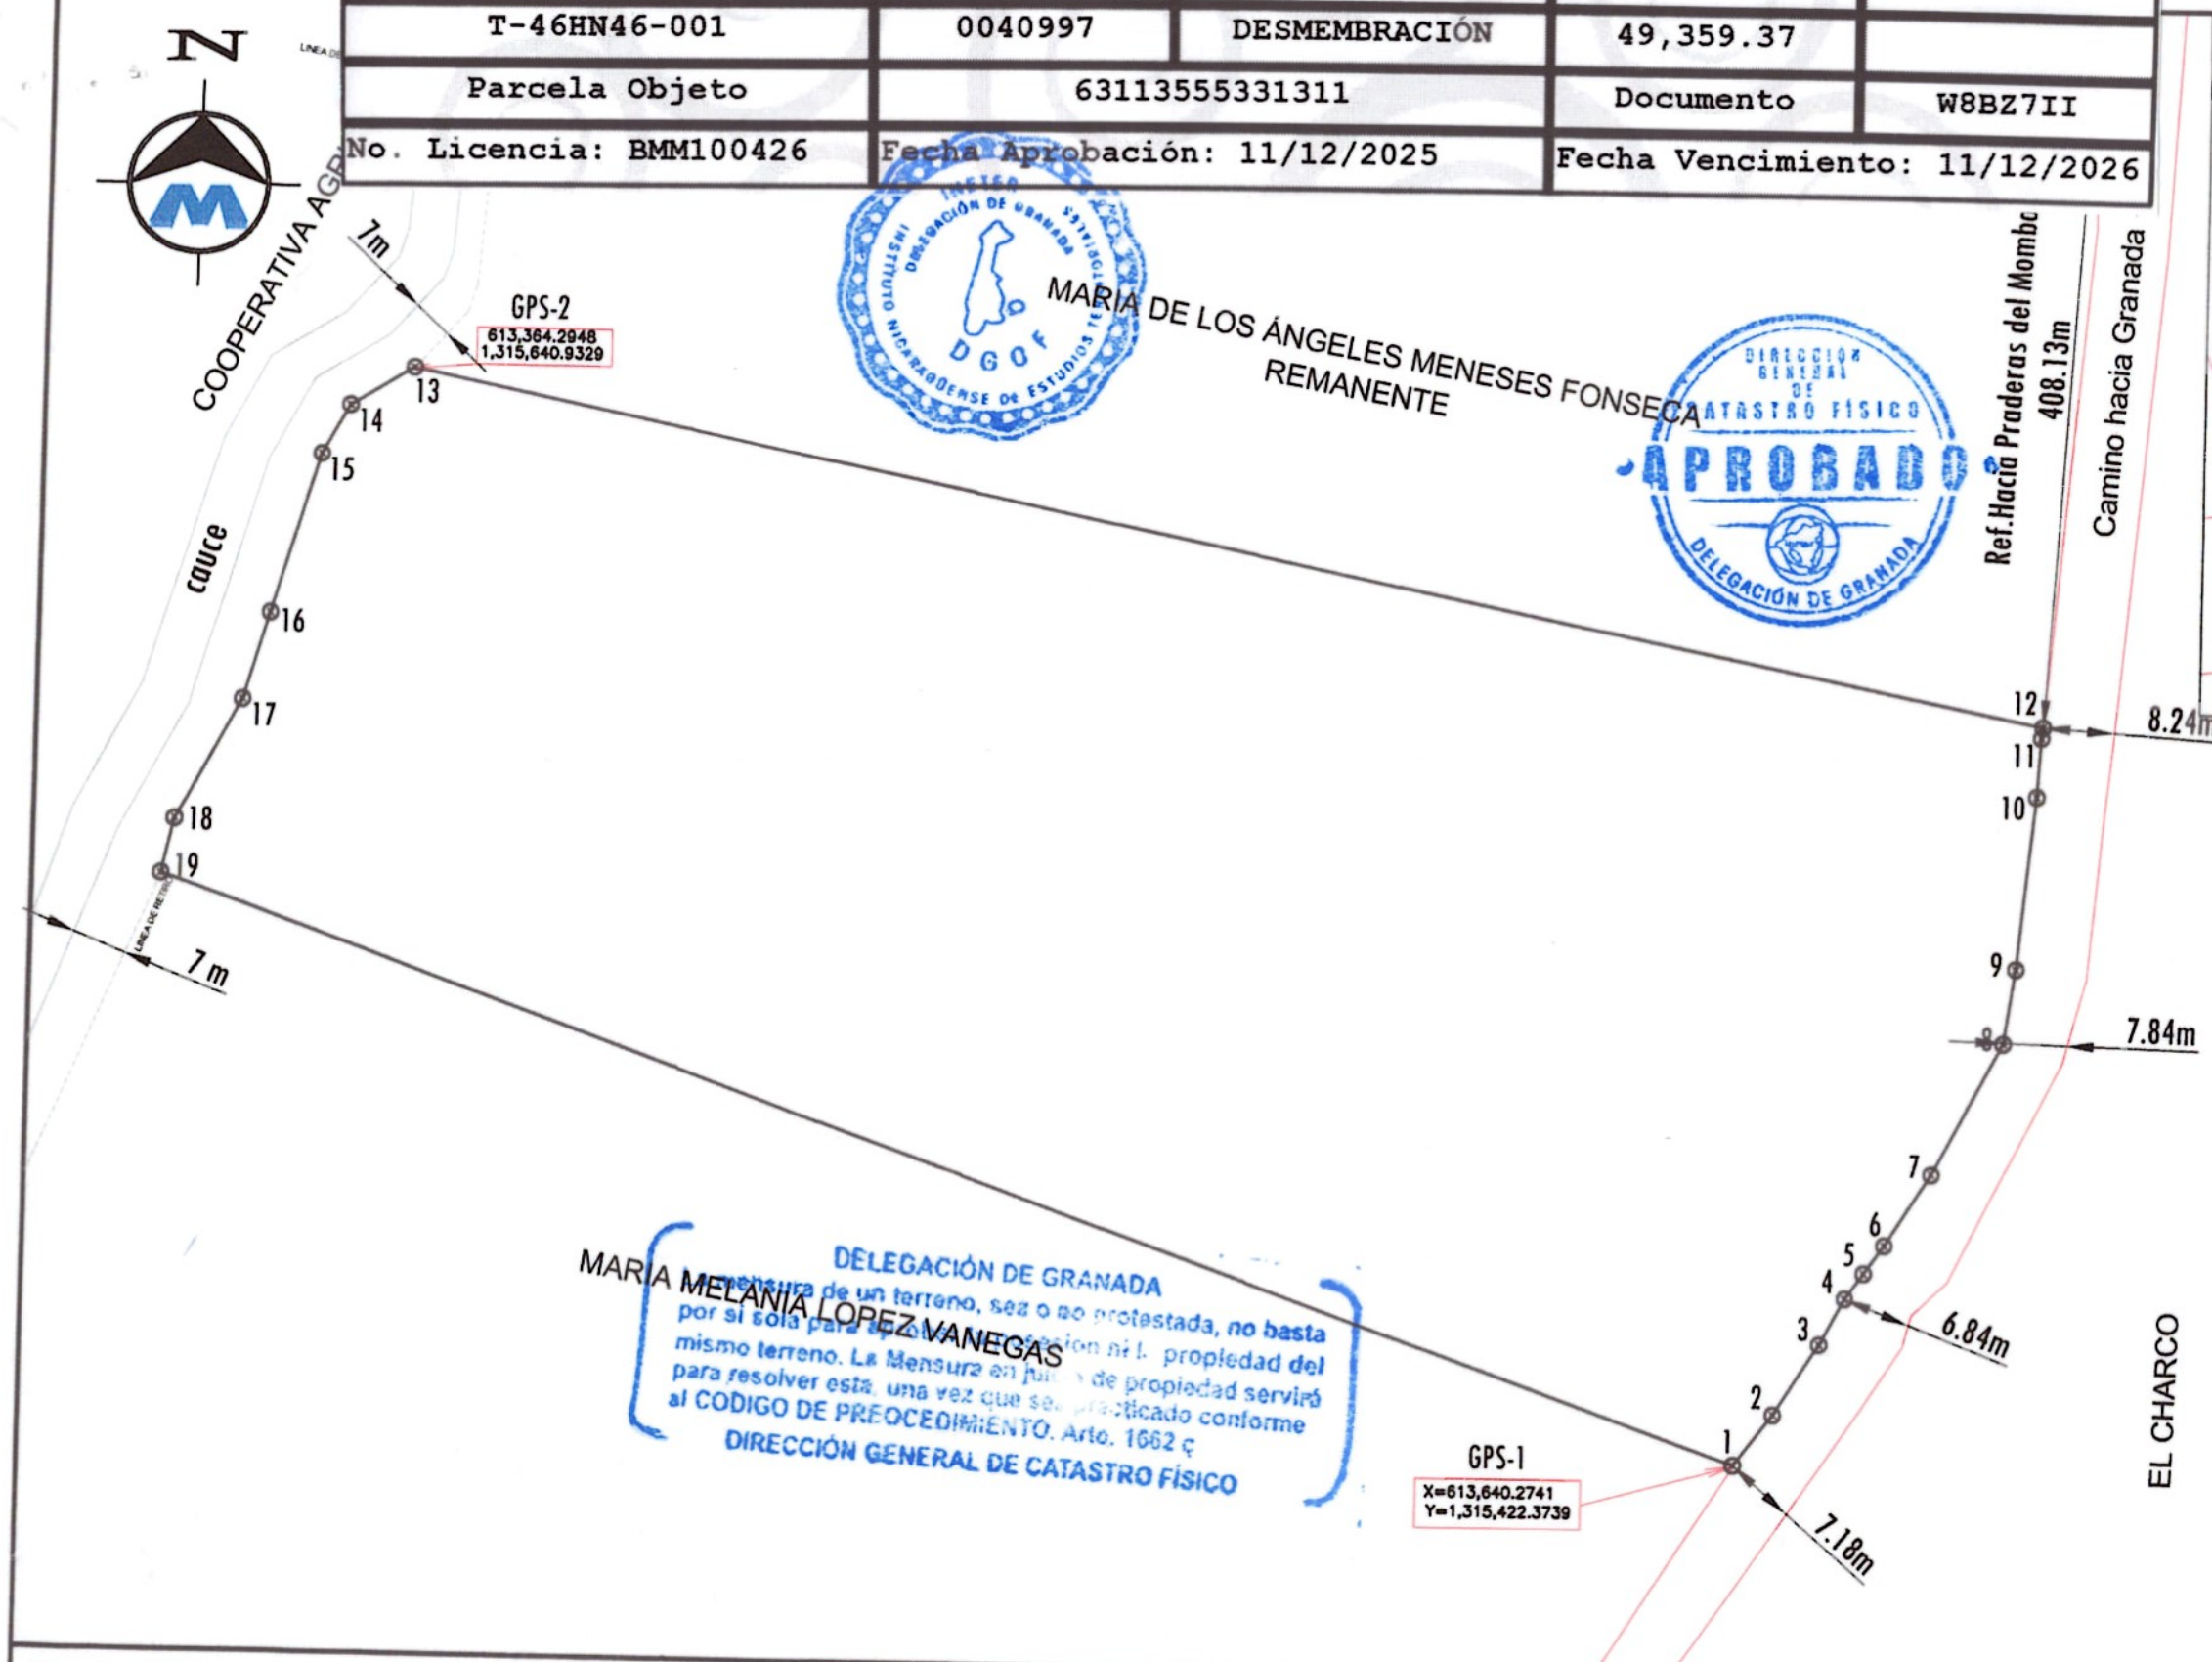

Planta de Ubicacion Sin Escala
Número Catastral:3051-4-09-000-05908

CUADRO DE CONSTRUCCION

LADO EST	LADO PV	RUMBO	DISTANCIA	V	COORDENADAS Y	COORDENADAS X
				1	1,315,422.3739	613,640.2741
1	2	N 37°52'54.37" E	13.096	2	1,315,432.7105	613,648.3156
2	3	N 32°51'18.07" E	17.192	3	1,315,447.1522	613,657.6423
3	4	N 28°28'24.53" E	10.718	4	1,315,456.5735	613,662.7520
4	5	N 36°54'54.12" E	6.443	5	1,315,461.7246	613,666.6216
5	6	N 35°30'41.32" E	7.106	6	1,315,467.5090	613,670.7494
6	7	N 32°45'27.78" E	17.354	7	1,315,482.1031	613,680.1394
7	8	N 28°07'53.62" E	30.532	8	1,315,509.0283	613,694.5352
8	9	N 08°37'04.82" E	15.371	9	1,315,524.2262	613,696.8385
9	10	N 05°52'30.90" E	35.380	10	1,315,559.4206	613,700.4601
10	11	N 03°39'54.64" E	12.044	11	1,315,571.4405	613,701.2301
11	12	N 07°31'17.22" E	2.150	12	1,315,573.5721	613,701.5115
12	13	N 76°42'12.60" W	343.879	13	1,315,640.9329	613,364.2948
13	14	S 58°53'59.67" W	15.270	14	1,315,633.0456	613,351.2199
14	15	S 29°02'28.28" W	11.528	15	1,315,622.9669	613,345.6238
15	16	S 16°43'04.91" W	33.915	16	1,315,590.4855	613,335.8677
16	17	S 16°20'59.81" W	18.499	17	1,315,572.7344	613,330.6601
17	18	S 27°51'18.46" W	27.793	18	1,315,548.1613	613,317.6740
18	19	S 12°20'32.86" W	11.390	19	1,315,537.0348	613,315.2394
19	1	S 70°34'08.22" E	344.666	1	1,315,422.3739	613,640.2741

SUPERFICIE = 49,359.362 m2

Objeto Lev: Venta Parcial-Desmembracion	Número Catastral:3051-4-09-000-05908	Fecha: 5 de Diciembre del 2025	FIRMA:
Propietario: Maria de los Ángeles Meneses Fonseca c.c. Maria de los Ángeles Meneses Fonseca de Caldera CED- 201-120548-0002V	Ubicación:Finca San Agustin, del Residencial Las Praderas del Mombacho 408.13m al suroeste. Municipio de Granada. Departamento de Granada.	Ejecuta: Ing.Bosco Javier Morgan Lic. Catastral: BMM100426 Cel: 8883-7568 Email: ingmorgan73@gmail.com servicios topograficos	
Adquiere:Francisco Javier Gutierrez Ramirez CED- 201-040179-0012U	Area:49359.362 M2 = 4.94 HECTAREAS =7 Mnz	Escala: 1 / 2,100	

MORGAN
Servicios Topograficos
Ing. Bosco Javier Morgan
Lic Catastral BMM100426
Cel: 8883 7568

Objeto Lev: Venta Parcial-Desmembracion

Numero Catastral:3051-4-09-000-05908

COORDENADAS NO VINCULADAS A LA RED GEODESICA DE NICARAGUA

CUADRO DE CONSTRUCCION

LADO		RUMBO	DISTANCIA	V	COORDENADAS	
EST	PV				Y	X
				1	1,315,422.3739	613,640.2741
1	2	N 37°52'54.37" E	13.096	2	1,315,432.7105	613,648.3156
2	3	N 32°51'18.07" E	17.192	3	1,315,447.1522	613,657.6423
3	4	N 28°28'24.53" E	10.718	4	1,315,456.5735	613,662.7520
4	5	N 36°54'54.12" E	6.443	5	1,315,461.7246	613,666.6216
5	6	N 35°30'41.32" E	7.106	6	1,315,467.5090	613,670.7494
6	7	N 32°45'27.78" E	17.354	7	1,315,482.1031	613,680.1394
7	8	N 28°07'53.62" E	30.532	8	1,315,509.0283	613,694.5352
8	9	N 08°37'04.82" E	15.371	9	1,315,524.2262	613,696.8385
9	10	N 05°52'30.90" E	35.380	10	1,315,559.4206	613,700.4601
10	11	N 03°39'54.64" E	12.044	11	1,315,571.4405	613,701.2301
11	12	N 07°31'17.22" E	2.150	12	1,315,573.5721	613,701.5115
12	13	N 78°42'12.80" W	343.879	13	1,315,640.9329	613,364.2948
13	14	S 58°53'59.67" W	15.270	14	1,315,633.0456	613,351.2199
14	15	S 29°02'28.28" W	11.528	15	1,315,622.9669	613,345.6238
15	16	S 16°43'04.91" W	33.915	16	1,315,590.4855	613,335.8677
16	17	S 16°20'59.81" W	18.499	17	1,315,572.7344	613,330.6601
17	18	S 27°51'18.46" W	27.793	18	1,315,548.1613	613,317.6740
18	19	S 12°20'32.86" W	11.390	19	1,315,537.0348	613,315.2394
19	1	S 70°34'08.22" E	344.666	1	1,315,422.3739	613,640.2741

SUPERFICIE = 49,359.362 m2

Ejecuta: Ing.Bosco Javier Morgan
Lic. Catastral: BMM100426
Cel: 8883-7568 Email: ingmorgan73@gmail.com
servicios topograficos

MORGAN
Servicios Topograficos
Ing Bosco Javier Morgan
Lic Catastral BMM100426
Cel 8883 7568 T