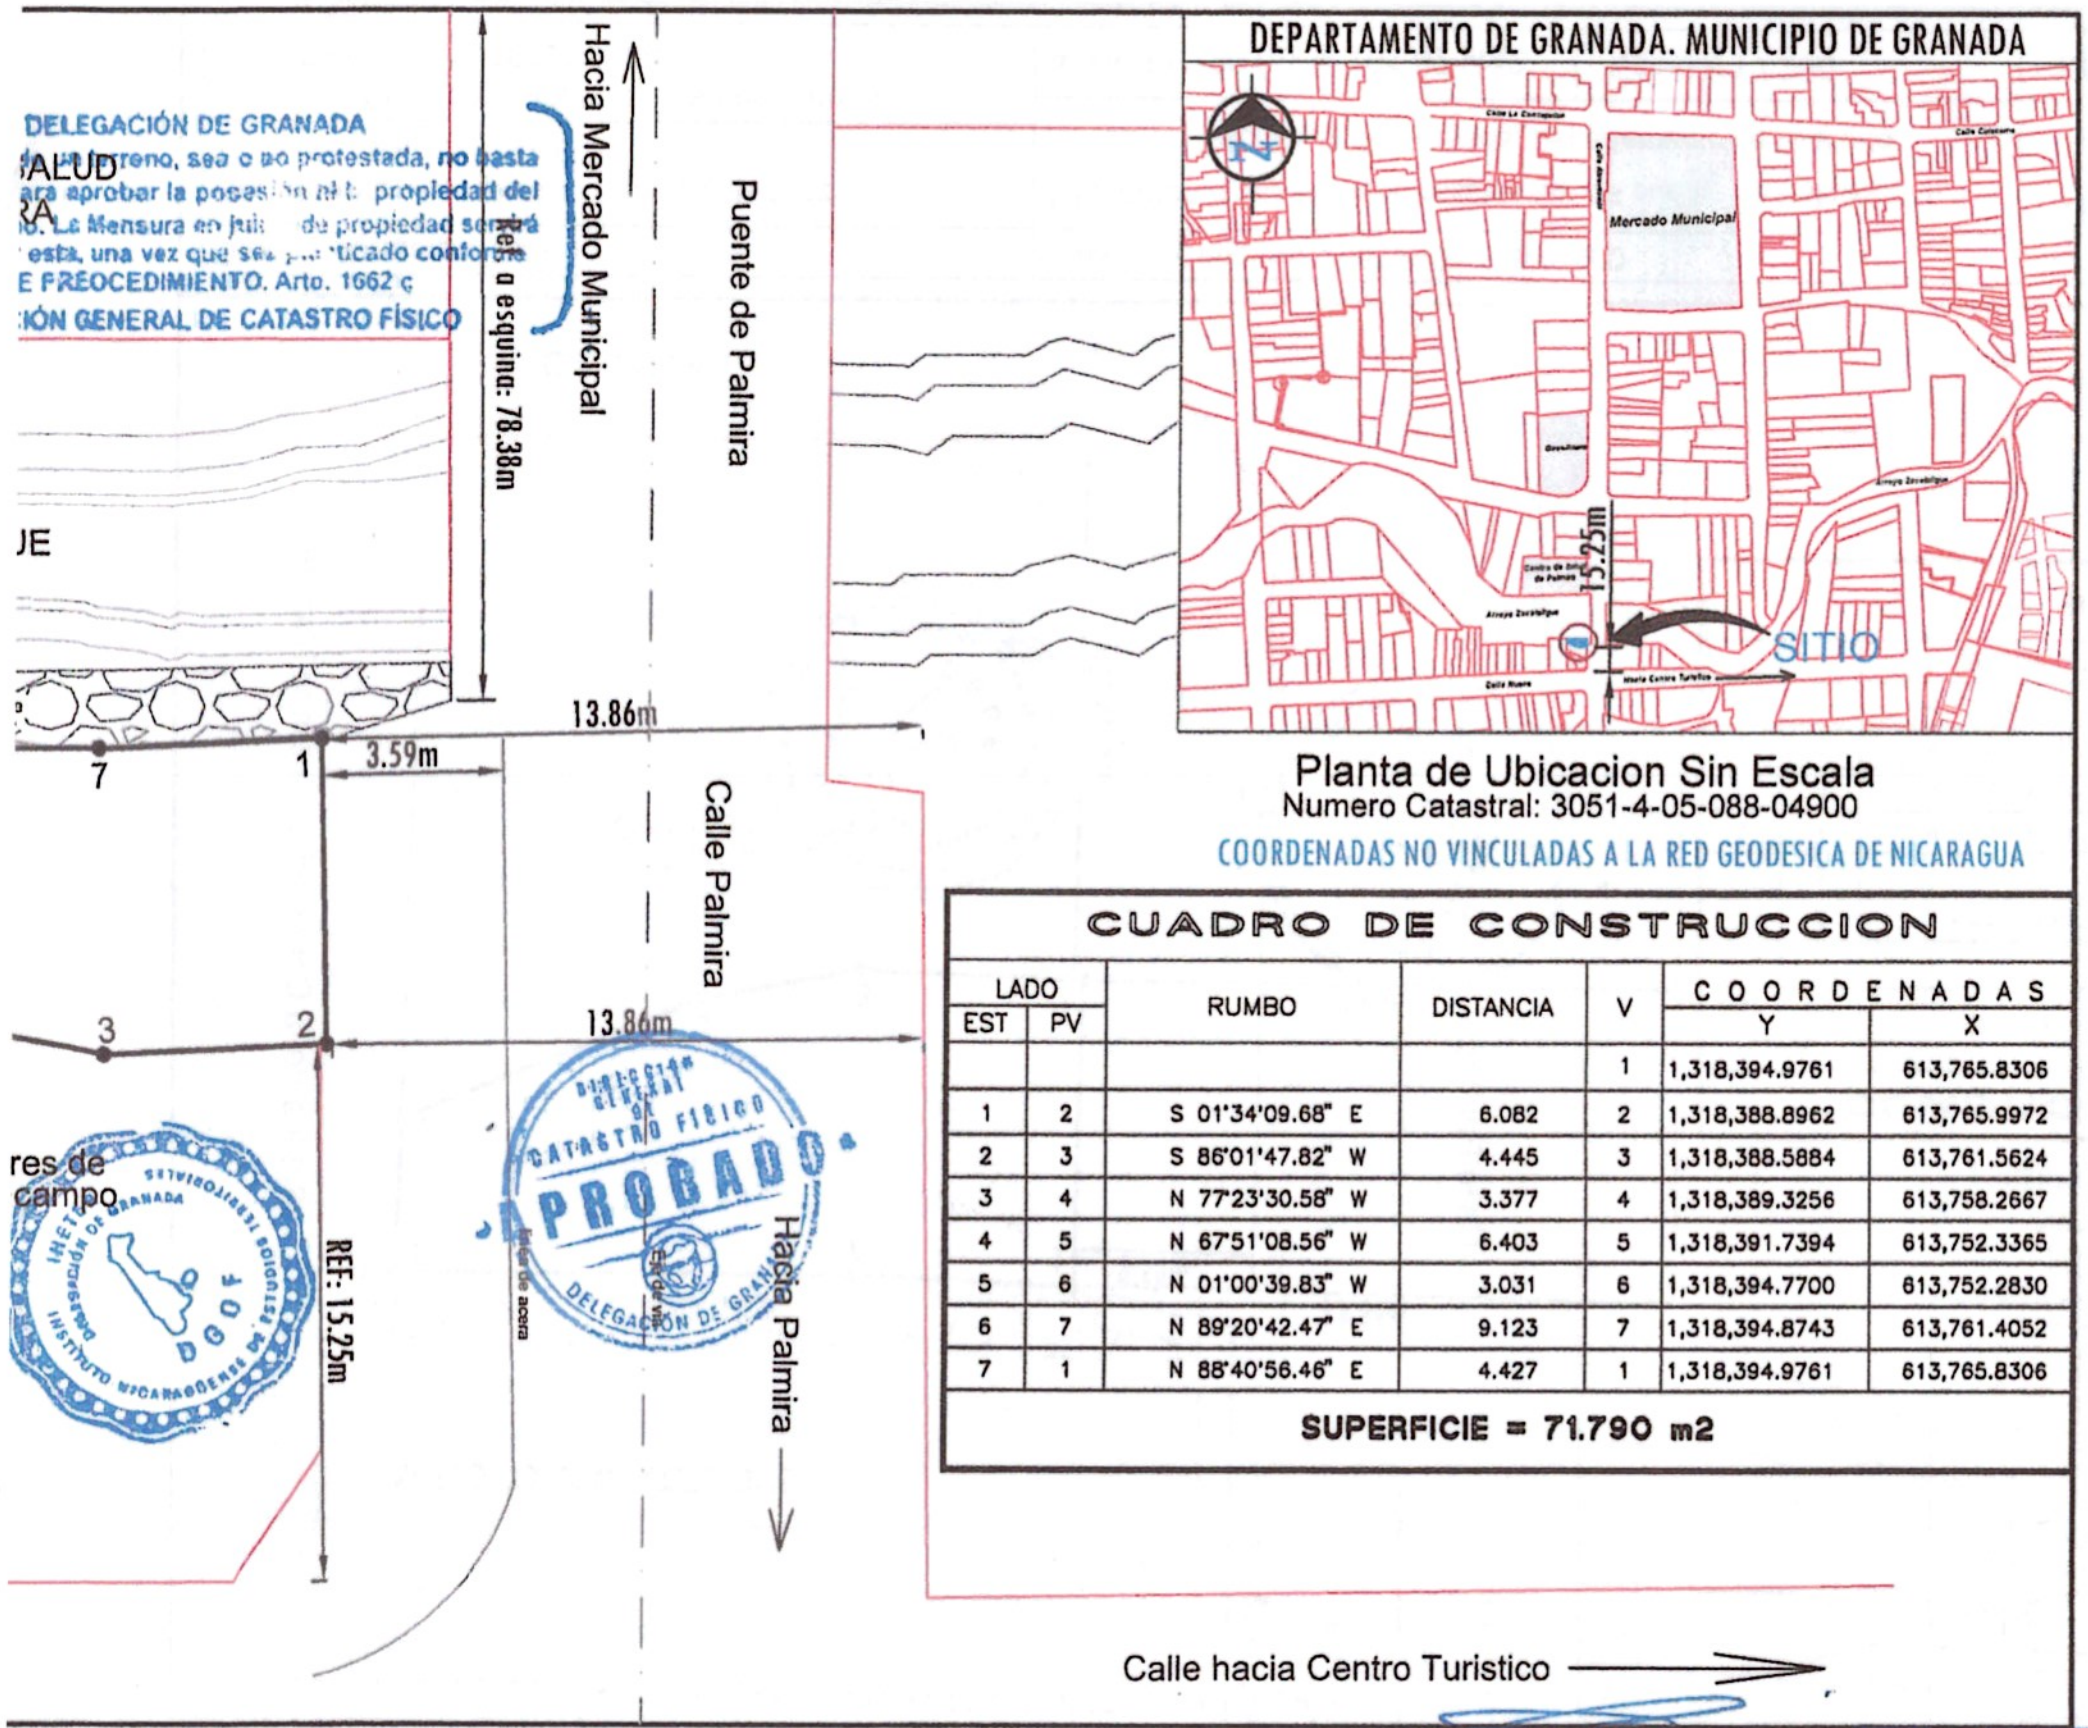

Planta de Ubicacion Sin Escala

Numero Catastral: 3051-4-05-088-04900

COORDENADAS NO VINCULADAS A LA RED GEODESICA DE NICARAGUA

CUADRO DE CONSTRUCCION

LADO EST	LADO PV	RUMBO	DISTANCIA	V	COORDENADAS Y	COORDENADAS X
				1	1,318,394.9761	613,765.8306
1	2	S 01°34'09.68" E	6.082	2	1,318,388.8962	613,765.9972
2	3	S 86°01'47.82" W	4.445	3	1,318,388.5884	613,761.5624
3	4	N 77°23'30.58" W	3.377	4	1,318,389.3256	613,758.2667
4	5	N 67°51'08.56" W	6.403	5	1,318,391.7394	613,752.3365
5	6	N 01°00'39.83" W	3.031	6	1,318,394.7700	613,752.2830
6	7	N 89°20'42.47" E	9.123	7	1,318,394.8743	613,761.4052
7	1	N 88°40'56.46" E	4.427	1	1,318,394.9761	613,765.8306

SUPERFICIE = 71.790 m2

	Numero Catastral: 3051-4-05-088-04900	FIRMA:	SELLO
inez	Ubicacion: Calle Palmira, costado sur del puente de Palmira B/ I. Municipio de Granada, Departamento de Granada.	Ejecuta: Ing Bosco Javier Morgan Lic. Catastral: BMM100426 Cel: 8883-7568 Email: ingmorgan73@gmail.com SERVICIOS TOPOGRAFICOS	
Jarquin	Area: 71.790 m2 = 101.82 vrs2 — Escala: 1 / 200	Fecha:08 de diciembre del 2025	

Transacción	Cudoc	Objeto	Área (m²)	No. Lote
T-46HN2K-001	0040998	TRASPASO TOTAL	71.79	
Parcela Objeto	631138735836 14		Documento	W8BZ7IZ
No. Licencia: BMM100426	Fecha Aprobación: 11/12/2025		Fecha Vencimiento: 11/12/2026	

Planta de Ubicacion Sin Escala
Número Catastra: 3051-4-05-068-35000

COORDENADAS NO VINCULADAS A LA RED GEODESICA DE NICARAGUA

CUADRO DE CONSTRUCCION

LADO EST	LADO PV	RUMBO	DISTANCIA	V	COORDENADAS Y	COORDENADAS X
				1	1,319,202.1270	613,872.3360
1	2	S 89°48'08.21" E	22.208	2	1,319,202.0604	613,894.5422
2	3	S 00°39'57.82" W	7.909	3	1,319,194.1424	613,894.4905
3	4	S 00°10'23.06" E	13.315	4	1,319,180.8389	613,894.9550
4	5	N 89°51'41.01" W	20.551	5	1,319,180.5884	613,874.4043
5	6	N 00°22'38.62" W	15.308	6	1,319,194.1138	613,872.9263
6	1	N 00°12'44.26" W	8.035	1	1,319,202.1270	613,872.3360

SUPERFICIE = 453.091 m2

Adquirientes:
Veronica Gabriela Martinez
Numero de pasaporte: A38694999
Monica Valeria Martinez
Numero de pasaporte: A41993131
Samuel Lionel Martinez
Numero de pasaporte 667467087

Objeto Lev: Donacion total de la Nuda Propiedad con Reserva de Usufructo	Número Catastral: 3051-4-05-068-35000	Fecha: 21 de Noviembre de 2025	FIRMA:
Enajenante: Sonia Veronica Miranda Bengochea. Cédula: 201-080358-0005X conocida registralmente como: Veronica Miranda De Martinez	Ubicación: Calle El Beso, del restaurante El Tiptop 37.35m al Oeste Municipio de Granada. Dpto. Granada	Ejecuta: Ing Bosco Javier Morgan Lic. Catastral: BMM100426 Cel: 8833-7568 Email: ingmorgan73@gmail.com servicios topograficos	
Adquirientes: Arriba indicados	Area 453.091 m2 = 642.671 vrs2	Factor de Escala: 1.418415	Escala: 1 / 400

Objeto Plano	Área (m²)	No. Lote	
TRASPASO TOTAL	453.09		
63113981882610	Documento	WRRZ3DX	
Fecha Aprobación: 28/11/2025	Fecha Vencimiento: 28/11/2026 17:32:59		
Cudoc	0040648		
Transacción	T-46H264-001		
Parcela Objeto			
No. Licencia: BMM100426			

Servicios Topograficos
Ing Bosco Javier Morgan
Lic. Catastral BMM100426
Cel 8833 7568

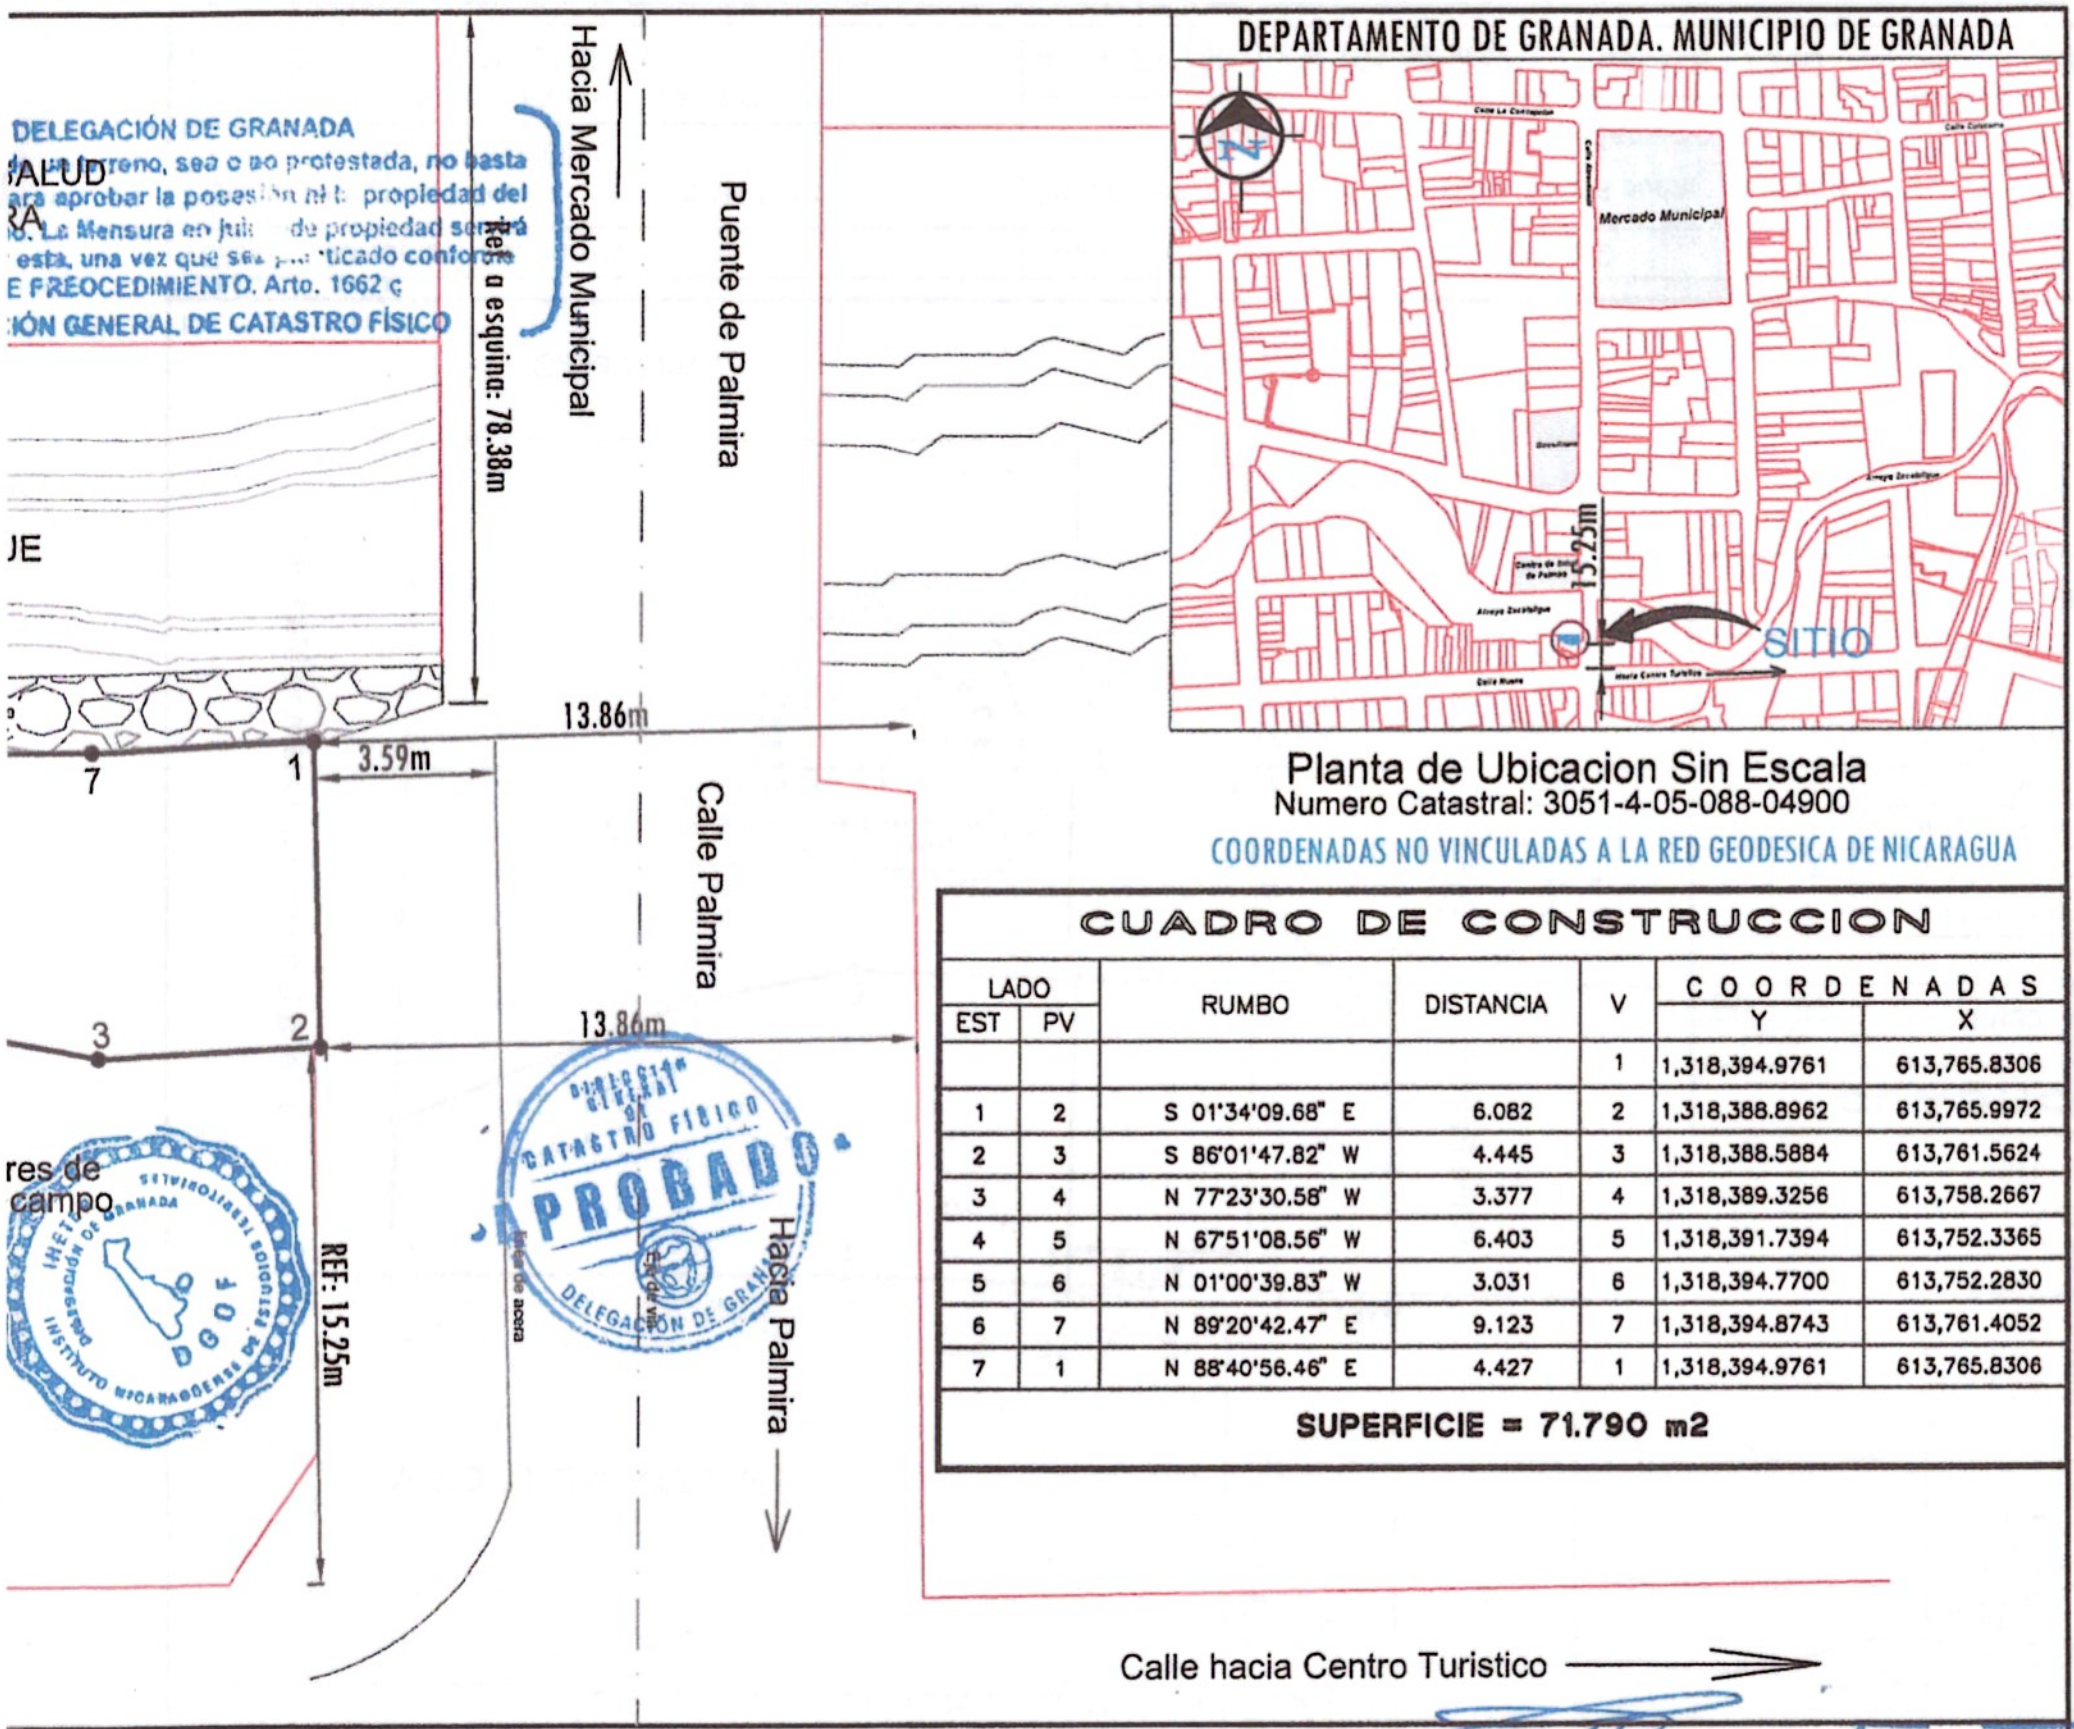

CUADRO DE CONSTRUCCION

LADO EST	LADO PV	RUMBO	DISTANCIA	V	COORDENADAS Y	COORDENADAS X
				1	1,318,394.9761	613,765.8306
1	2	S 01°34'09.68" E	6.082	2	1,318,388.8962	613,765.9972
2	3	S 86°01'47.82" W	4.445	3	1,318,388.5884	613,761.5624
3	4	N 77°23'30.58" W	3.377	4	1,318,389.3256	613,758.2667
4	5	N 67°51'08.56" W	6.403	5	1,318,391.7394	613,752.3365
5	6	N 01°00'39.83" W	3.031	6	1,318,394.7700	613,752.2830
6	7	N 89°20'42.47" E	9.123	7	1,318,394.8743	613,761.4052
7	1	N 88°40'56.46" E	4.427	1	1,318,394.9761	613,765.8306

SUPERFICIE = 71.790 m2

Transacción	Cudoc	Objeto Plano	No. Lote
T-46HN2K-001	0040998	TRASPASO TOTAL	
Parcela Objeto		63113873583614	W8BZ7IZ
No. Licencia: BMM100426	Fecha Aprobación: 11/12/2025		Fecha Vencimiento: 11/12/2026

	Numero Catastral: 3051-4-05-088-04900	FIRMA:	SELLO
	Ubicacion: Calle Palmira, costado sur del puente de Palmira B/ I. Municipio de Granada, Departamento de Granada.	Ejecuta: Ing Bosco Javier Morgan Lic. Catastral: BMM100426 Cel: 8883-7568 Email: ingmorgan73@gmail.com SERVICIOS TOPOGRAFICOS	
	Area: 71.790 m2 = 101.82 vrs2	Escala: 1 / 200	Fecha:08 de diciembre del 2025