DELEGACIÓN DE GRANADA
La mensura de un terreno, sea o no protestada, no basta por sí sola para aprobar la posesión ni la propiedad del mismo terreno. La Mensura en juicio de propiedad servirá para resolver esta, una vez que sea practicado conforme al CODIGO DE PROCEDIMIENTO. Arto. 1662 c
DIRECCIÓN GENERAL DE CATASTRO FÍSICO

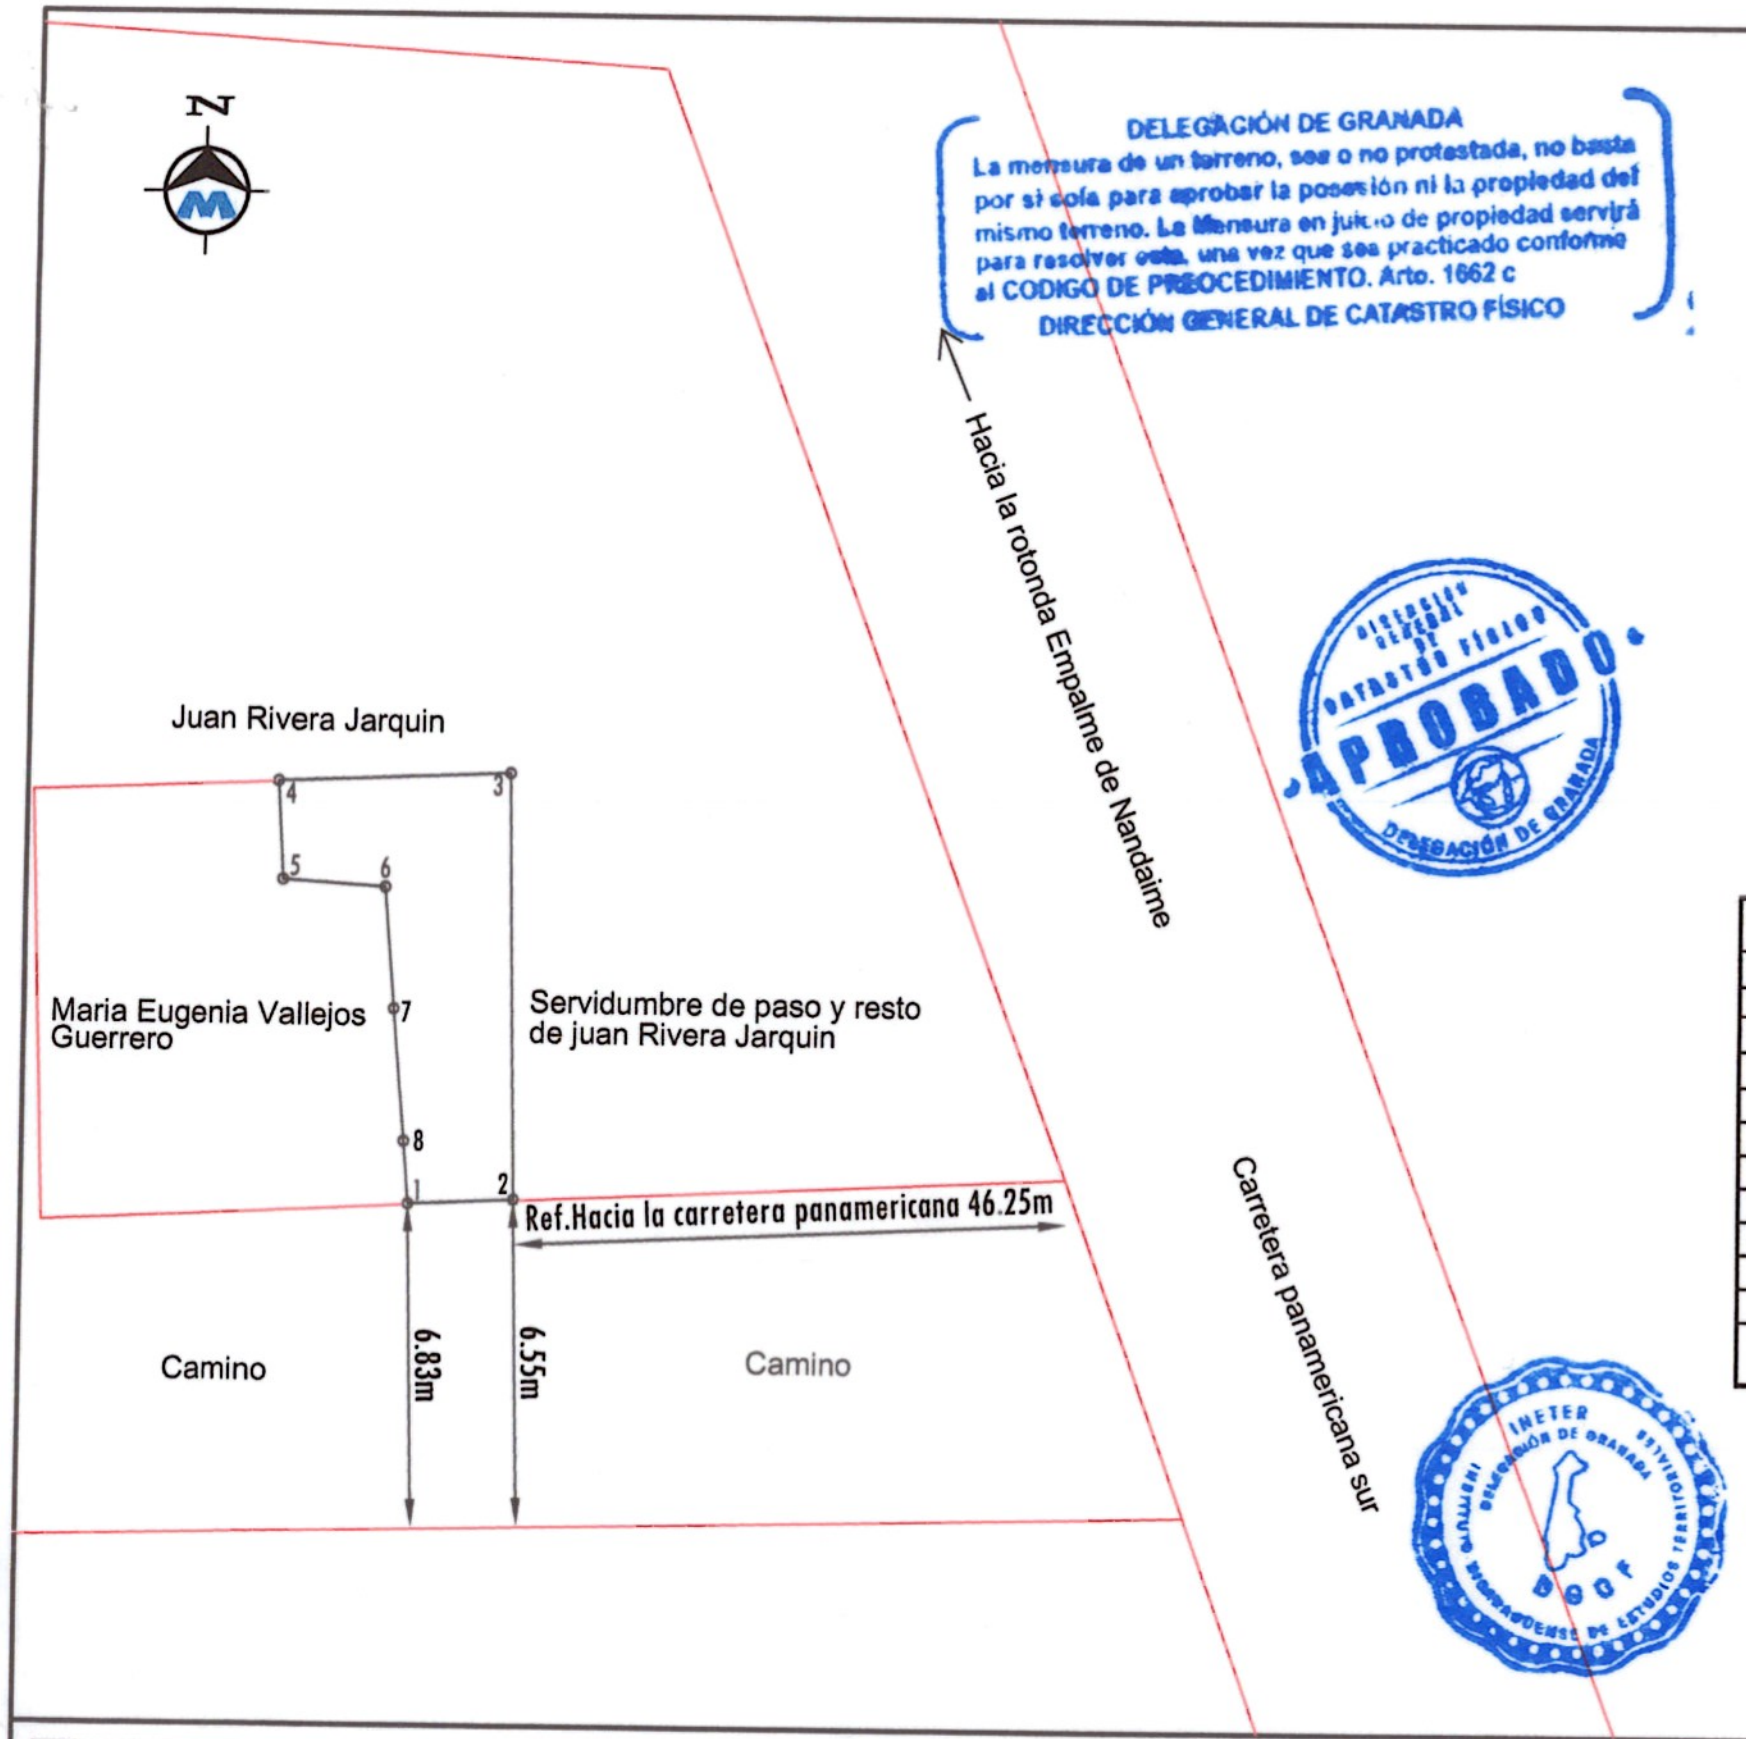

APROBADO
DIRECCIÓN GENERAL DE CATASTRO FÍSICO
DELEGACIÓN DE GRANADA

Planta de Ubicacion Sin Escala
Número Catastra:2951-2-08-000-13303 N/C

COORDENADAS NO VINCULADAS A LA RED GEODESICA DE NICARAGUA

CUADRO DE CONSTRUCCION

LADO EST	LADO PV	RUMBO	DISTANCIA	V	COORDENADAS Y	COORDENADAS X
				1	1,301,410.3942	603,319.3076
1	2	N 87°16'28.22" E	8.476	2	1,301,410.7972	603,327.7739
2	3	N 01°11'52.43" W	33.942	3	1,301,444.7314	603,327.0644
3	4	S 87°31'23.55" W	18.504	4	1,301,443.9317	603,308.5772
4	5	S 03°28'08.11" E	7.877	5	1,301,436.0691	603,309.0538
5	6	S 86°26'19.66" E	8.109	6	1,301,435.5654	603,317.1476
6	7	S 04°49'27.47" E	9.702	7	1,301,425.8975	603,317.9635
7	8	S 05°12'15.56" E	10.583	8	1,301,415.3579	603,318.9235
8	1	S 04°25'27.77" E	4.979	1	1,301,410.3942	603,319.3076

SUPERFICIE = 390.774 m2

INETER DELEGACIÓN DE GRANADA INSTITUTO NICARAGÜENSE DE ESTUDIOS TERRITORIALES

MORGAN
Servicios Topograficos
Ing Bosco Javier Morgan
Lic Catastral: BMM100426
Cel: 8883 7568 T

Objeto Lev: Desmembracion y compra Venta	Número Catastral:2951-2-08-000-13303 N/C	Fecha: 4 de Diciembre del 2025	FIRMA:
Enajenante: Teodora Del Carmen Berroteran Garcia. Cédula: 202-281070-0005P	Ubicación: CMCA.Breñas N°1 entrada la pollera Municipio de Nandaime. Dpto. Granada	Ejecuta: Ing.Bosco Javier Morgan Lic. Catastral: BMM100426 Cel: 8883-7568 Email: ingmorgan73@gmail.com servicios topograficos	
Adquiriente: Ana Dalila Vallejos Guerrero Cédula: 202-160893-0002W	Area: 390.774 m2 = 554.279vrs2	Escala: 1 / 800	

Transacción	Cudoc	Objeto Plano	Área (m²)	No. Lote
T-46H082-001	0041034	DESMEMBRACIÓN	390.77	
Parcela Objeto	63003134122914		Documento	W8BZ9JF
No. Licencia: BMM100426	Fecha Aprobación: 16/12/2025		Fecha Vencimiento: 16/12/2026	

Objeto Lev: Desmembracion y compra Venta

Numero Catastral:2951-2-08-000-13303 N/C

Fecha: 4 de Diciembre del 2025

COORDENADAS NO VINCULADAS A LA RED GEODESICA DE NICARAGUA

CUADRO DE CONSTRUCCION

LADO		RUMBO	DISTANCIA	V	COORDENADAS	
EST	PV				Y	X
				1	1,301,410.3942	603,319.3076
1	2	N 87°16'28.22" E	8.476	2	1,301,410.7972	603,327.7739
2	3	N 01°11'52.43" W	33.942	3	1,301,444.7314	603,327.0644
3	4	S 87°31'23.55" W	18.504	4	1,301,443.9317	603,308.5772
4	5	S 03°28'08.11" E	7.877	5	1,301,436.0691	603,309.0538
5	6	S 86°26'19.66" E	8.109	6	1,301,435.5654	603,317.1476
6	7	S 04°49'27.47" E	9.702	7	1,301,425.8975	603,317.9635
7	8	S 05°12'15.58" E	10.583	8	1,301,415.3579	603,318.9235
8	1	S 04°25'27.77" E	4.979	1	1,301,410.3942	603,319.3076

SUPERFICIE = 390.774 m2

Ejecuta: Ing.Bosco Javier Morgan
Lic. Catastral: BMM100426
Cel: 8883-7568 Email: ingmorgan73@gmail.com
servicios topograficos

MORGAN
Servicios Topograficos
Ing. Bosco Javier Morgan
Lic. Catastral: BMM100426
Cel: 8883 7568 T