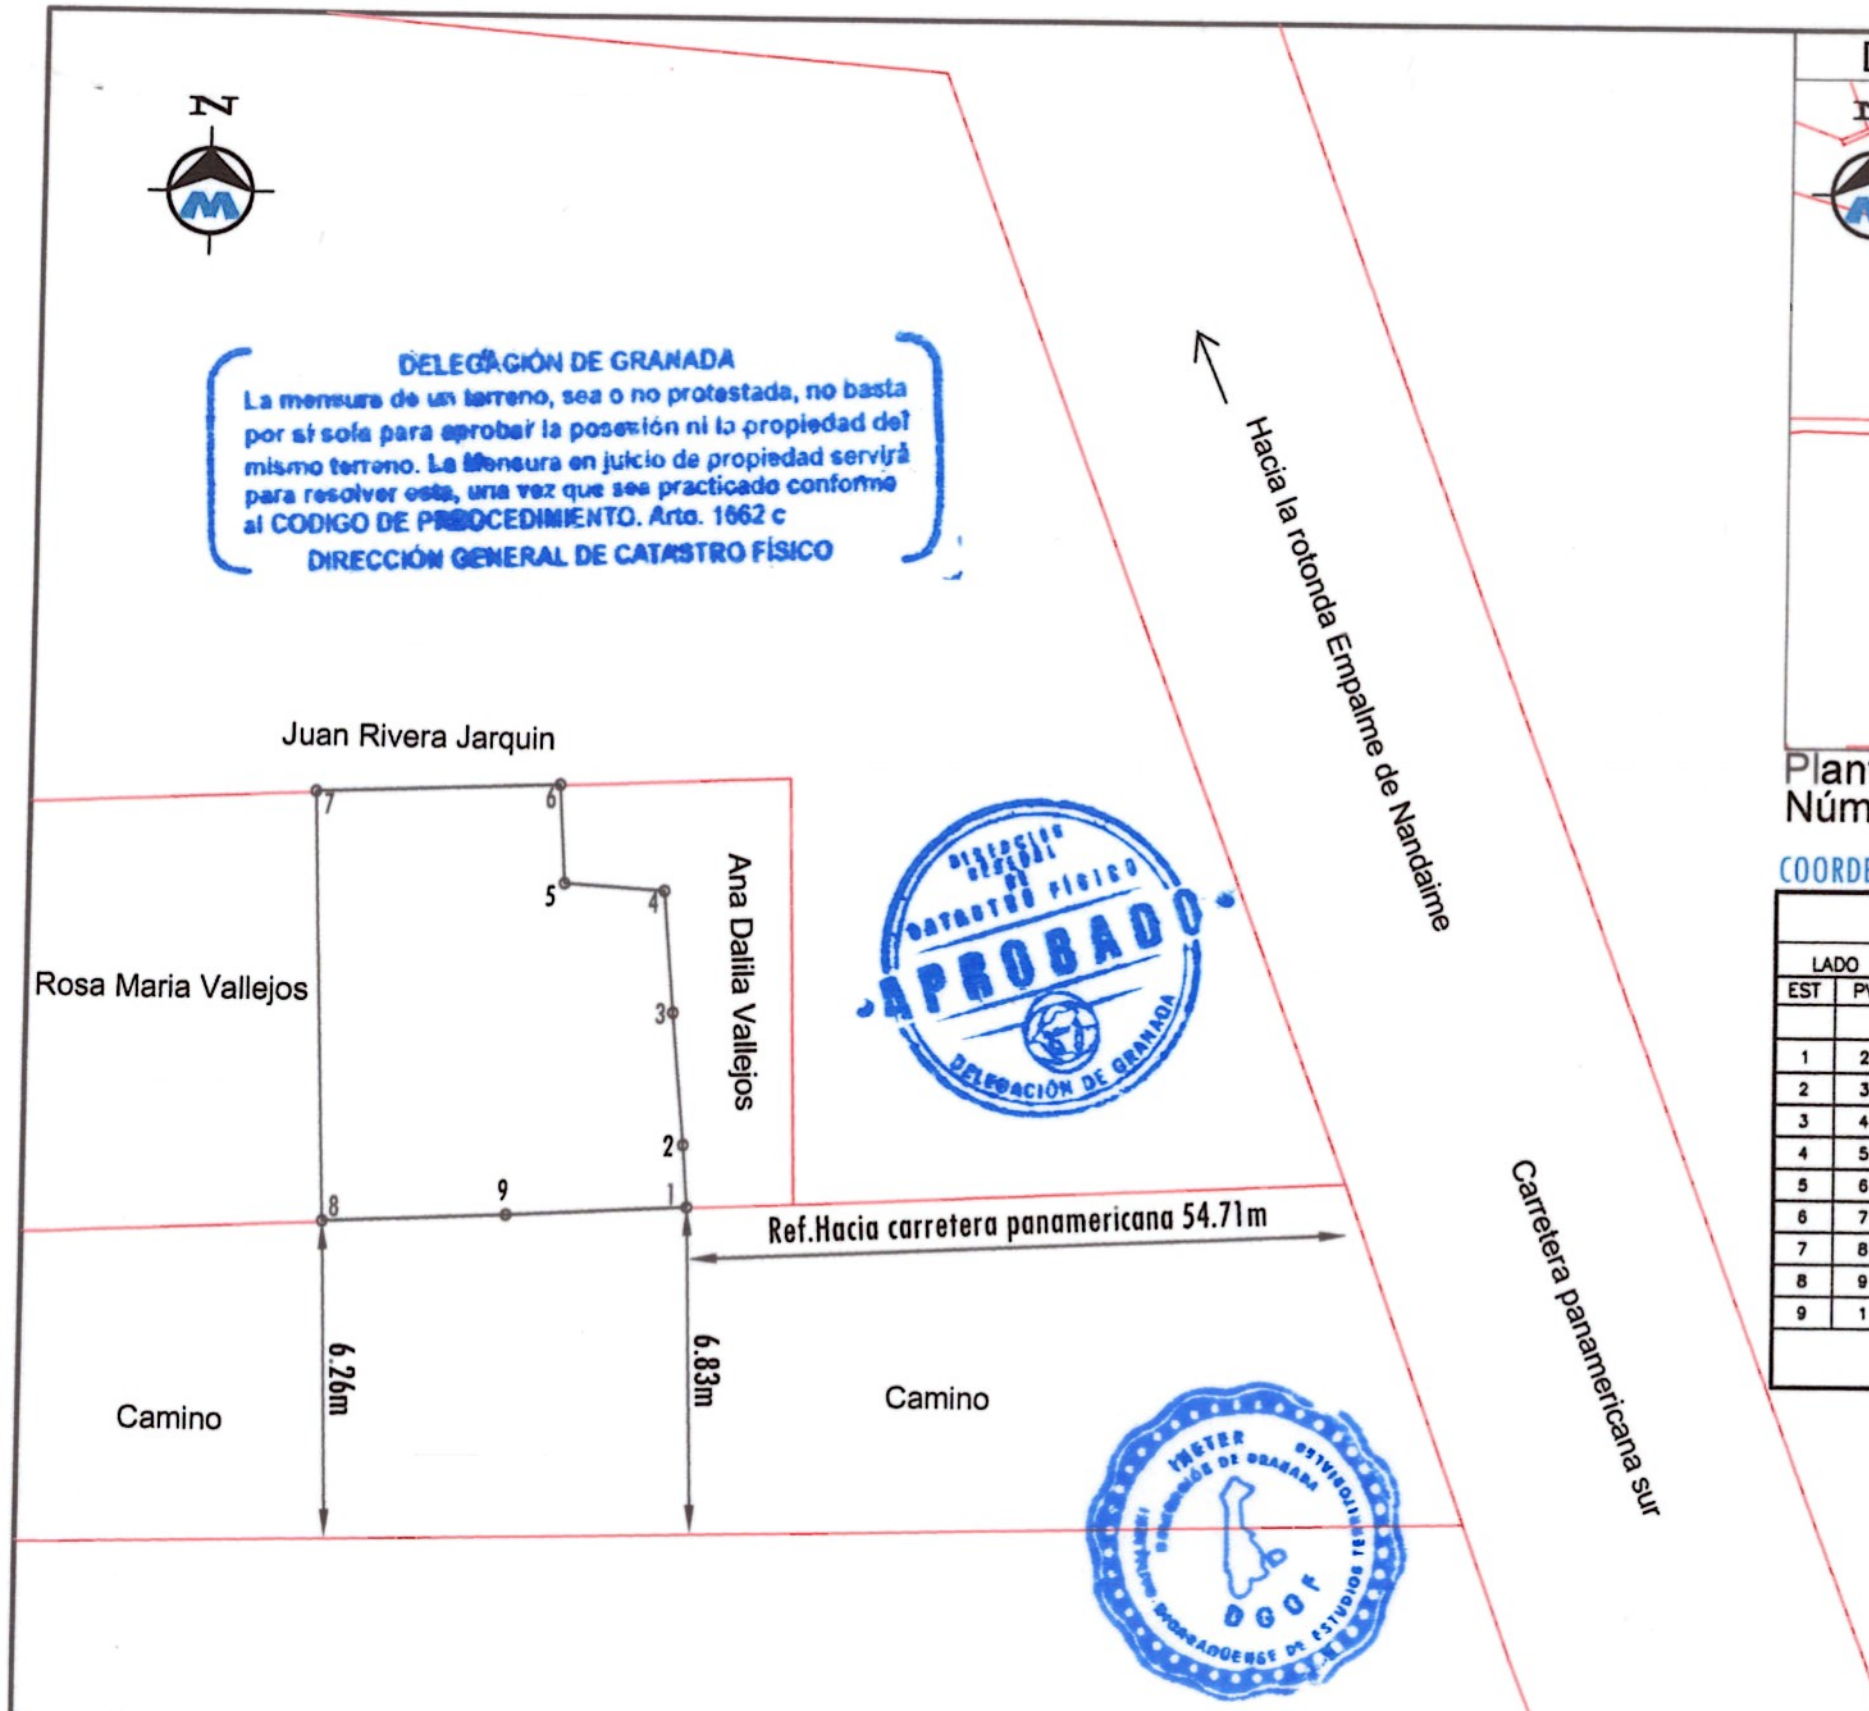

DEPARTAMENTO DE GRANADA MUNICIPIO DE NANDAIME

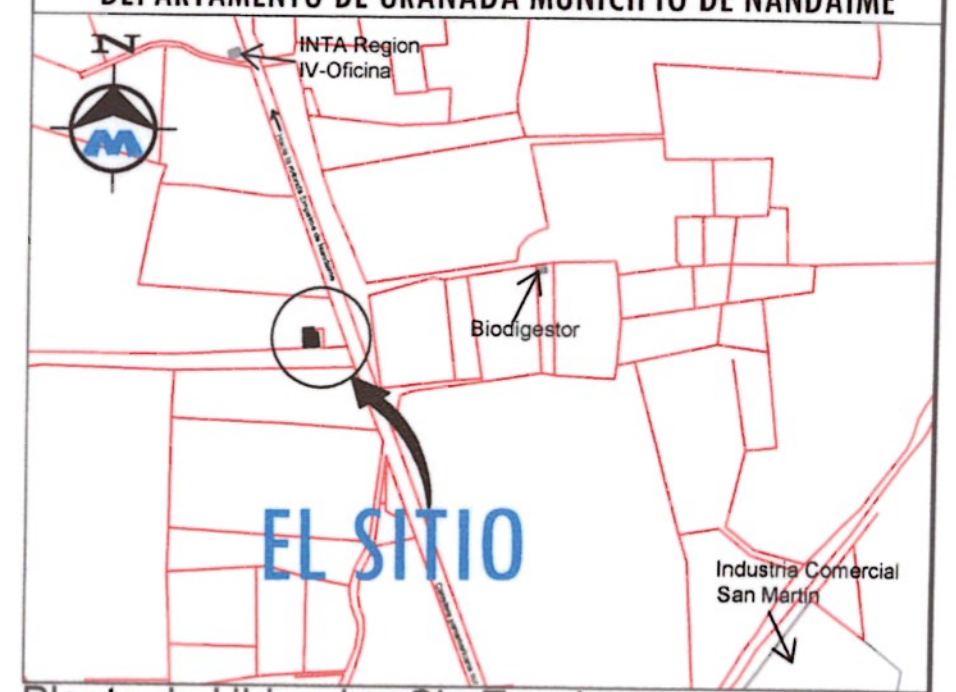

Planta de Ubicacion Sin Escala
Número Catastra:2951-2-08-000-13303 N/C

COORDENADAS NO VINCULADAS A LA RED GEODESICA DE NICARAGUA

CUADRO DE CONSTRUCCION

LADO EST	LADO PV	RUMBO	DISTANCIA	V	COORDENADAS Y	COORDENADAS X
				1	1,301,410.3942	603,319.3076
1	2	N 04°25'27.77" W	4.979	2	1,301,415.3579	603,318.9235
2	3	N 05°12'15.58" W	10.583	3	1,301,425.8975	603,317.9635
3	4	N 04°49'27.47" W	9.702	4	1,301,435.5654	603,317.1476
4	5	N 86°26'19.66" W	8.109	5	1,301,436.0691	603,309.0538
5	6	N 03°28'08.11" W	7.877	6	1,301,443.9317	603,308.5772
6	7	S 87°41'15.40" W	19.613	7	1,301,443.1404	603,288.9799
7	8	S 01°54'41.59" E	34.242	8	1,301,408.9179	603,290.1221
8	9	N 87°16'08.00" E	14.682	9	1,301,409.6175	603,304.7875
9	1	N 86°56'16.91" E	14.541	1	1,301,410.3942	603,319.3076
SUPERFICIE = 901.043 m2						

MORGAN
Servicios Topograficos
Ing Bosco Javier Morgan
Lic Catastral: BMM100426
Cel: 8883 7568

Objeto Lev: Desmembracion y compra Venta	Número Catastral:2951-2-08-000-13303 N/C	Fecha: 4 de Diciembre del 2025	FIRMA:
Enajenante: Teodora Del Carmen Berroteran Garcia. Cédula: 202-281070-0005P	Ubicación: CMCA.Breñas N°1 entrada la pollera Municipio de Nandaime. Dpto. Granada	Ejecuta: Ing.Bosco Javier Morgan Lic. Catastral: BMM100426 Cel: 8883-7568 Email: ingmorgan73@gmail.com servicios topograficos	
Adquiriente: Maria Eugenia Vallejos Guerrero Cédula: 202-311288-0001G	Area: 901.043 m2 = 1278.05vrs2	Escala: 1 / 800	

Objeto Plano	Área (m²)	No. Lote
DESMEMBRACIÓN	901.04	
Documento		W8BZ9L8
Cudoc	Transacción	
0041033	T-46H08H-001	
6300312492 4519	Parcela Objeto	
Fecha Aprobación: 16/12/2025	No. Licencia: BMM100426	Fecha Vencimiento: 16/12/2026

Objeto Lev: Desmembracion y compra Venta

Numero Catastral:2951-2-08-000-13303 N/C

Fecha: 4 de Diciembre del 2025

COORDENADAS NO VINCULADAS A LA RED GEODESICA DE NICARAGUA

CUADRO DE CONSTRUCCION

LADO		RUMBO	DISTANCIA	V	COORDENADAS	
EST	PV				Y	X
				1	1,301,410.3942	603,319.3076
1	2	N 04°25'27.77" W	4.979	2	1,301,415.3579	603,318.9235
2	3	N 05°12'15.58" W	10.583	3	1,301,425.8975	603,317.9635
3	4	N 04°49'27.47" W	9.702	4	1,301,435.5654	603,317.1476
4	5	N 86°26'19.66" W	8.109	5	1,301,436.0691	603,309.0538
5	6	N 03°28'08.11" W	7.877	6	1,301,443.9317	603,308.5772
6	7	S 87°41'15.40" W	19.613	7	1,301,443.1404	603,288.9799
7	8	S 01°54'41.59" E	34.242	8	1,301,408.9179	603,290.1221
8	9	N 87°16'08.00" E	14.682	9	1,301,409.6175	603,304.7875
9	1	N 86°56'16.91" E	14.541	1	1,301,410.3942	603,319.3076

SUPERFICIE = 901.043 m2

MORGAN
Servicios Topograficos
Ing. Bosco Javier Morgan
Lic. Catastral: BMM100426
Cel: 8883 7568 T

Ejecuta: Ing.Bosco Javier Morgan
Lic. Catastral: BMM100426
Cel: 8883-7568 Email: ingmorgan73@gmail.com
servicios topograficos