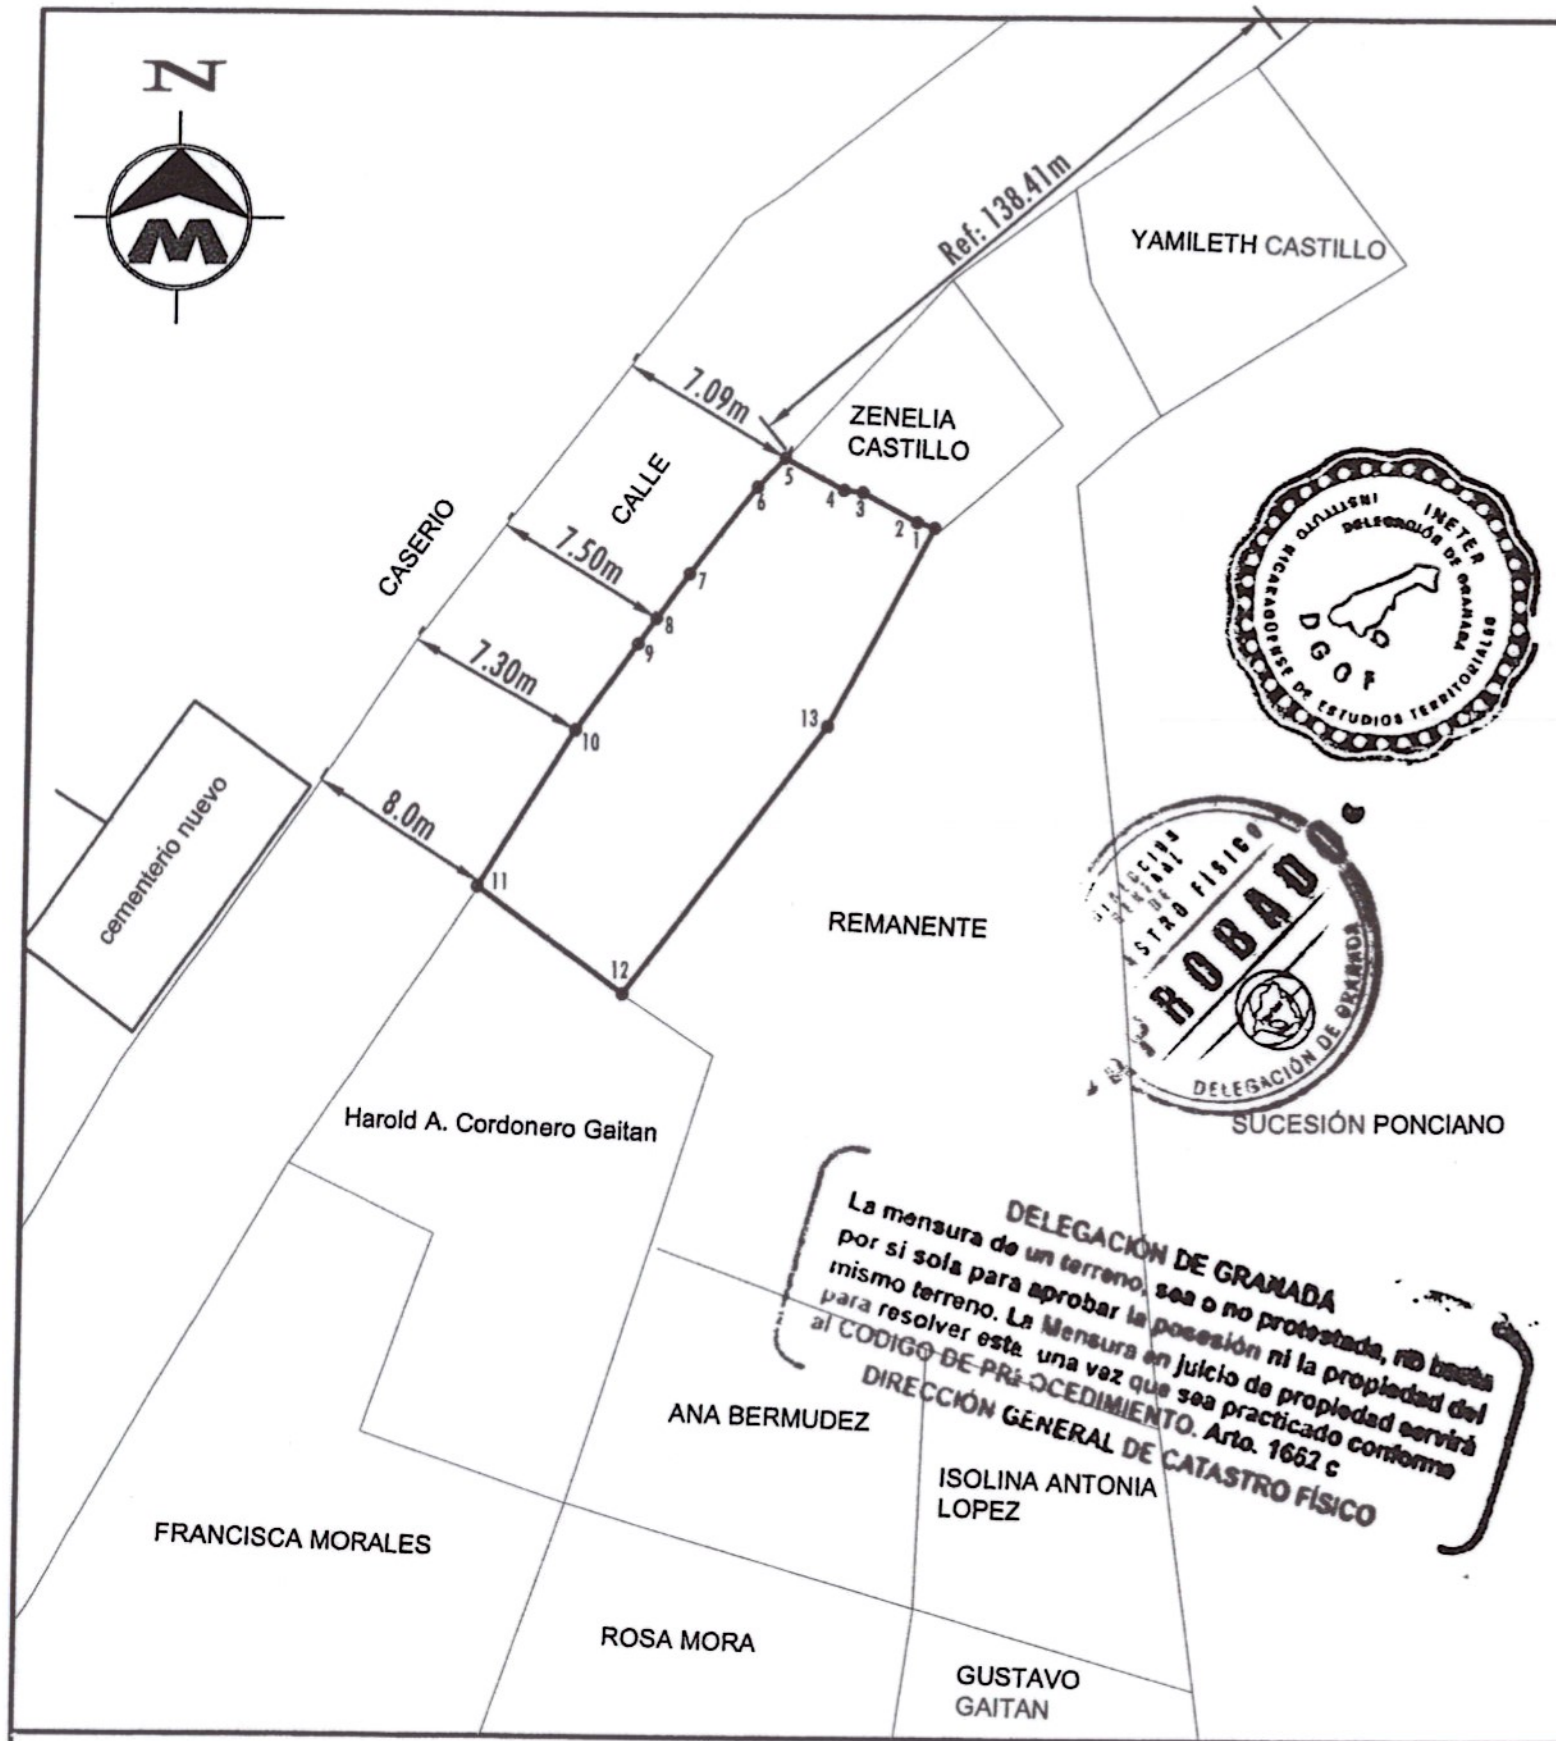

DELEGACIÓN DE GRANADA
La mensura de un terreno, sea o no protestada, no basta por si sola para aprobar la posesión ni la propiedad del mismo terreno. La Mensura en juicio de propiedad servirá para resolver esta una vez que sea practicado conforme al CODIGO DE PROCEDIMIENTO. Arto. 1662 c
DIRECCIÓN GENERAL DE CATASTRO FÍSICO

DEPARTAMENTO DE GRANADA MUNICIPIO DE GRANADA

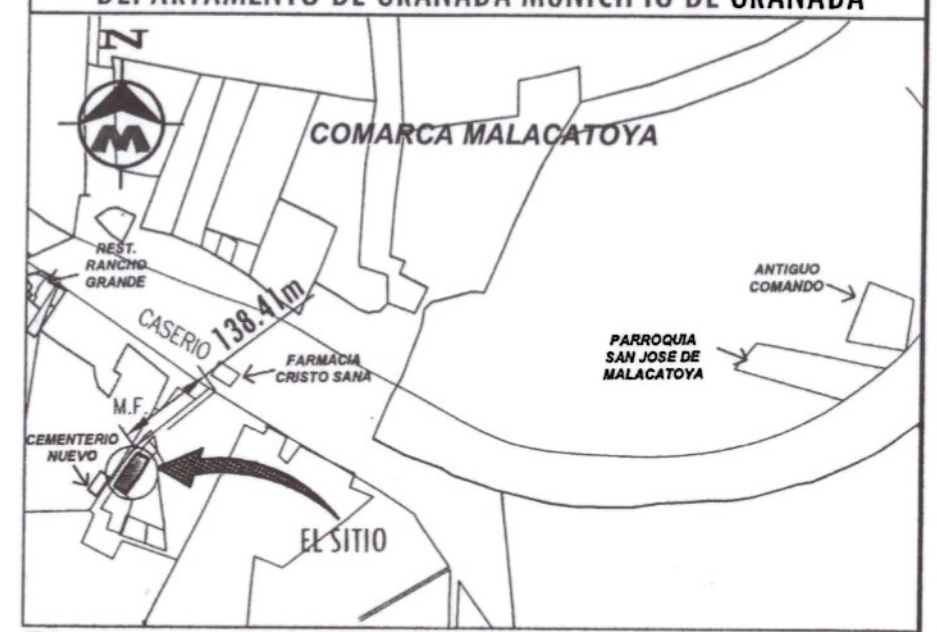

Planta de Ubicacion Sin Escala
Numero Catastral: 3052-3-03-000-02850
COORDENADAS NO VINCULADAS A LA RED GEODESICA DE NICARAGUA

CUADRO DE CONSTRUCCION

LADO EST	LADO PV	RUMBO	DISTANCIA	V	COORDENADAS Y	COORDENADAS X
				1	1,343,094.0944	626,180.8838
1	2	N 71°20'47.25" W	1.807	2	1,343,094.6722	626,179.1722
2	3	N 61°30'52.56" W	6.199	3	1,343,097.6286	626,173.7239
3	4	N 83°19'54.65" W	1.886	4	1,343,097.8476	626,171.8509
4	5	N 61°56'47.43" W	6.624	5	1,343,100.9626	626,166.0056
5	6	S 43°50'36.47" W	4.161	6	1,343,097.9617	626,163.1234
6	7	S 37°49'43.27" W	10.775	7	1,343,089.4512	626,156.5151
7	8	S 36°28'56.63" W	5.466	8	1,343,085.0565	626,153.2654
8	9	S 34°21'21.47" W	3.080	9	1,343,082.5139	626,151.5273
9	10	S 35°25'10.60" W	10.555	10	1,343,073.9122	626,145.4099
10	11	S 31°11'16.61" W	18.234	11	1,343,058.3131	626,135.9672
11	12	S 54°10'51.85" E	17.882	12	1,343,047.8479	626,150.4675
12	13	N 37°05'09.18" E	33.302	13	1,343,074.4138	626,170.5489
13	1	N 27°42'19.39" E	22.229	1	1,343,094.0944	626,180.8838
SUPERFICIE = 1,019.312 m2 = 1,445.80 Vrs2						

Objeto Lev: Venta Parcial - Desmembracion	Número Catastral: 3052-3-03-000-02850		FIRMA:
Enajenante: Isaura del Carmen Castillo Ced: 201-280559-0003W	Ubicación: Del Antiguo Comando 1 1/2c Este y 184.69m al Sur. Frente al Cementerio Nuevo Comarca de Malacatoya. Municipio de Granada. Depto de Granada.		Ejecuta: Ing.Bosco Javier Morgan Lic. Catastral: BMM100426 Cel: 8883-7568 Email: ingmorgan73@gmail.com servicios topograficos
Adquiriente: Ana Lopez Bermudez Ced: 201-240263-0004X	Área: 1,019.312 m2=1,445.80 vrs2	Escala: 1 / 1000	Fecha: 20 de Enero del 2026

Transacción	Cudoc	Objeto Plano
T-4CH4JR-001	0041758	DESMEMBRACIÓN
Parcela Objeto	6324631067631 7	Área (m²)
		1,019.31
No. Licencia: BMM100426	Fecha Aprobación: 26/1/2026	Documento
		W8BZKS6
	Fecha Vencimiento: 26/1/2027	No. Lote

Servicios Topograficos
Morgan
BMM100426
7568 T

Objeto Lev: Venta Parcial
Número Catastral: 3052-3-03-000-02850

COORDENADAS NO VINCULADAS A LA RED GEODESICA DE NICARAGUA

CUADRO DE CONSTRUCCION

LADO		RUMBO	DISTANCIA	V	COORDENADAS	
EST	PV				Y	X
				1	1,343,094.0944	626,180.8838
1	2	N 71°20'47.25" W	1.807	2	1,343,094.6722	626,179.1722
2	3	N 61°30'52.56" W	6.199	3	1,343,097.6286	626,173.7239
3	4	N 83°19'54.65" W	1.886	4	1,343,097.8476	626,171.8509
4	5	N 61°56'47.43" W	6.624	5	1,343,100.9626	626,166.0056
5	6	S 43°50'36.47" W	4.161	6	1,343,097.9617	626,163.1234
6	7	S 37°49'43.27" W	10.775	7	1,343,089.4512	626,156.5151
7	8	S 36°28'56.63" W	5.466	8	1,343,085.0565	626,153.2654
8	9	S 34°21'21.47" W	3.080	9	1,343,082.5139	626,151.5273
9	10	S 35°25'10.60" W	10.555	10	1,343,073.9122	626,145.4099
10	11	S 31°11'16.61" W	18.234	11	1,343,058.3131	626,135.9672
11	12	S 54°10'51.85" E	17.882	12	1,343,047.8479	626,150.4675
12	13	N 37°05'09.18" E	33.302	13	1,343,074.4138	626,170.5489
13	1	N 27°42'19.39" E	22.229	1	1,343,094.0944	626,180.8838

SUPERFICIE = 1,019.312 m2 = 1,445.80 Vrs2

Ejecuta: Ing.Bosco Javier Morgan
Lic. Catastral: BMM100426
Cel: 8883-7568 Email: ingmorgan73@gmail.com
servicios topograficos

MORGAN
Servicios Topograficos
Ing Bosco Javier Morgan
Lic Catastral: BMM100426
Cel: 8883 7568