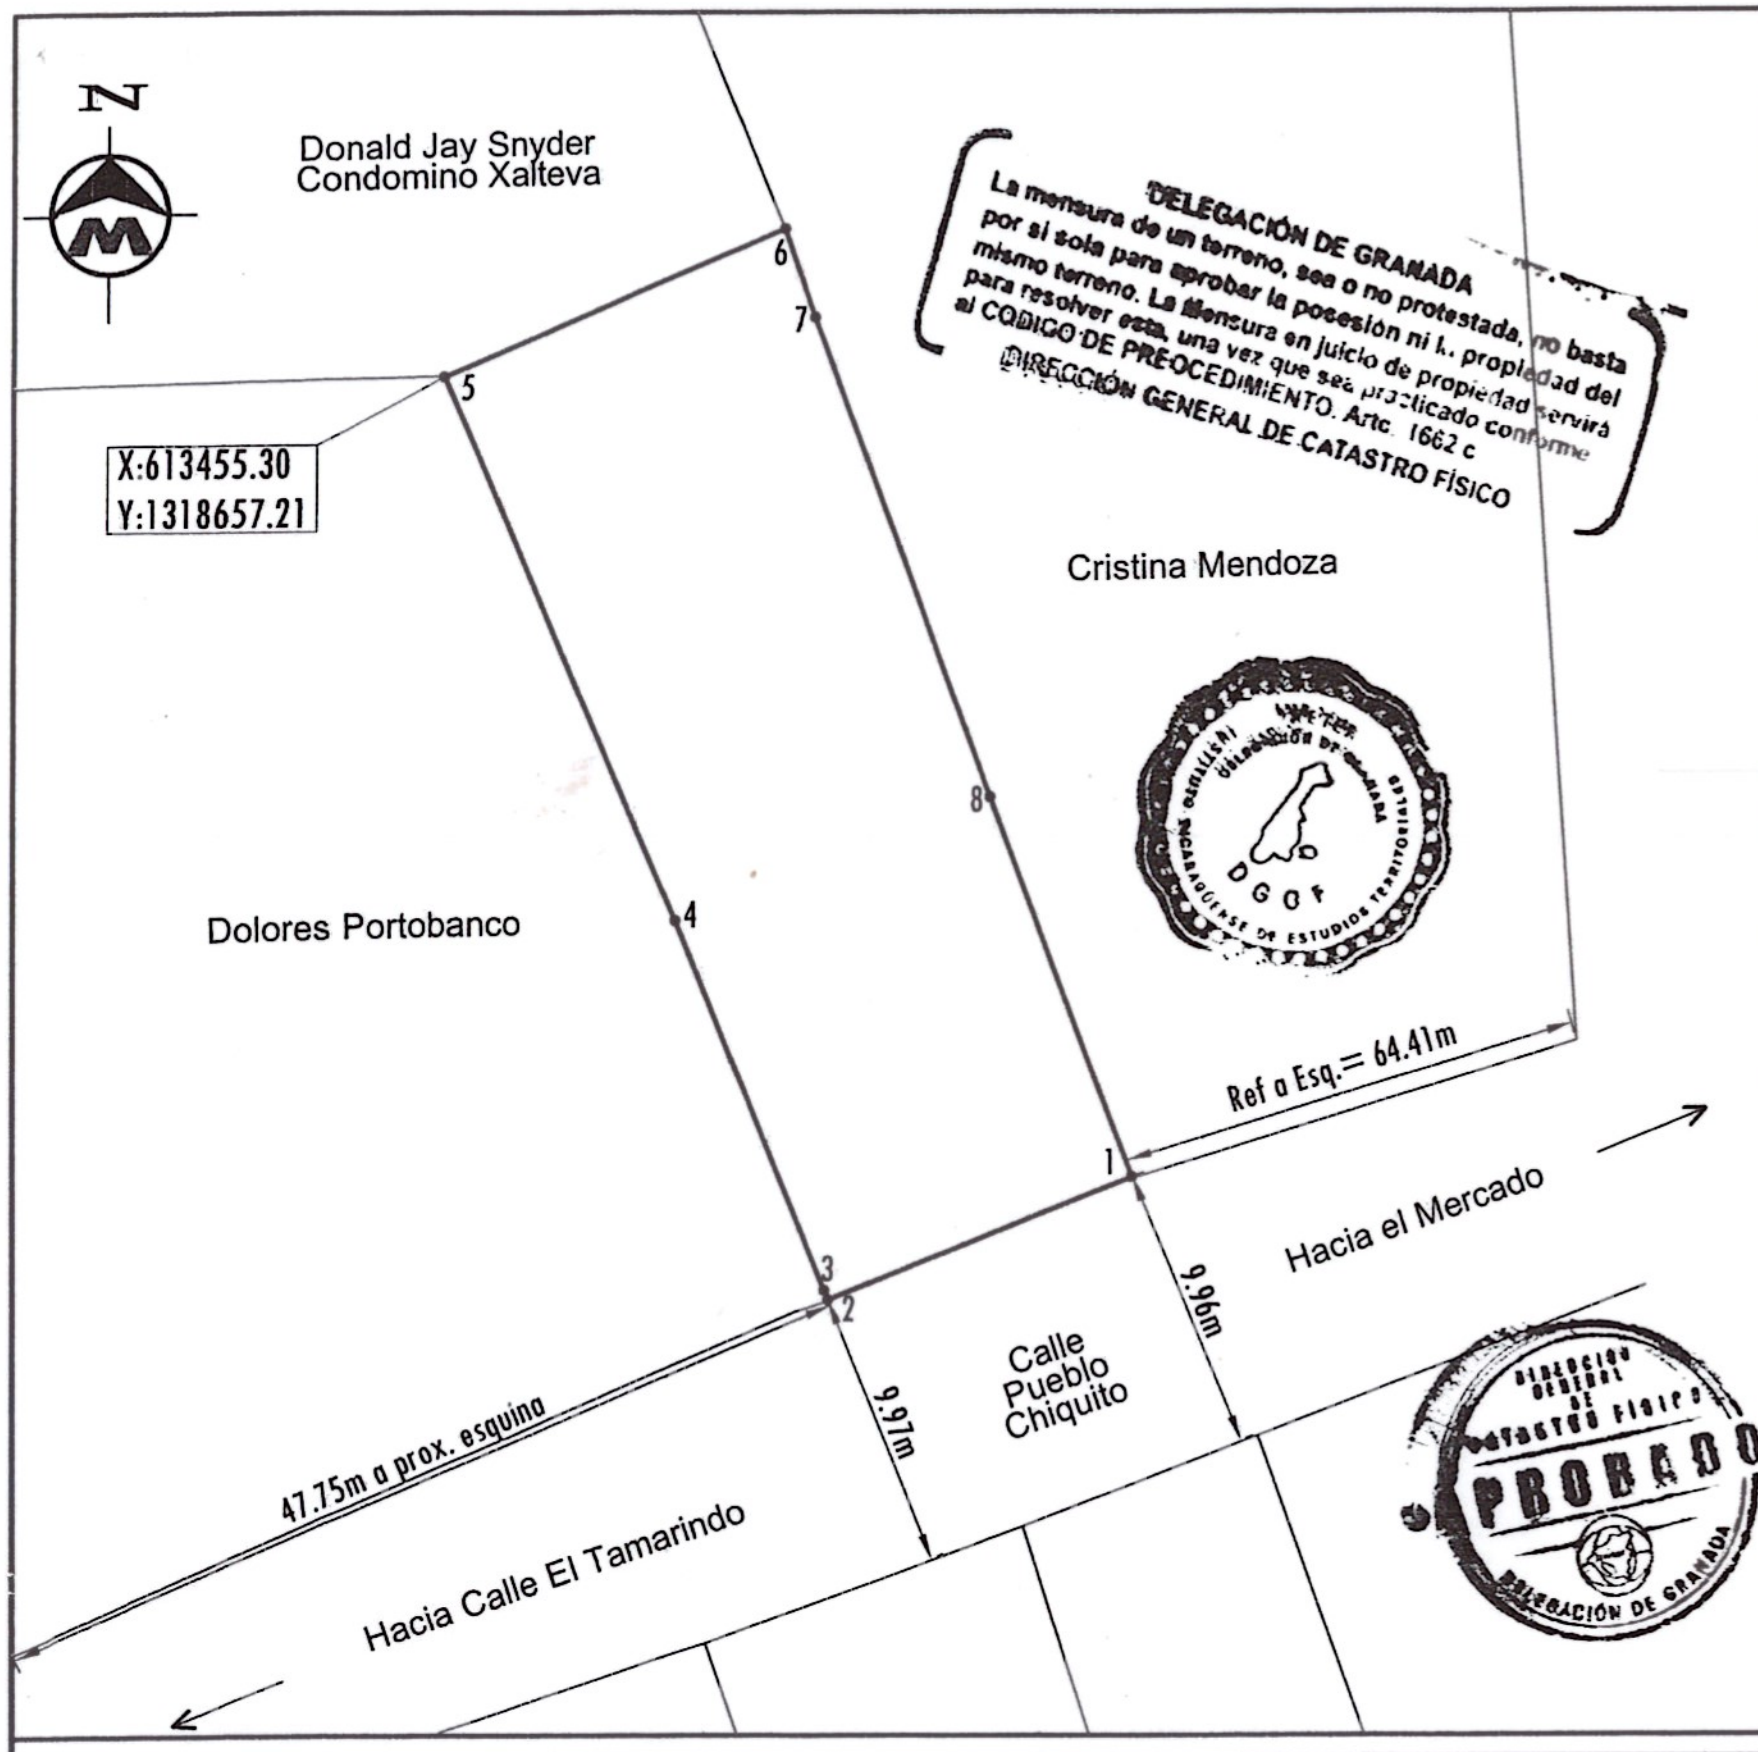

DELEGACIÓN DE GRANADA
La mensura de un terreno, sea o no protestada, no basta por sí sola para aprobar la posesión ni la propiedad del mismo terreno. La mensura en juicio de propiedad servirá para resolver esta, una vez que sea practicado conforme al CODIGO DE PREOCEDIMIENTO. Artc. 1662 c
DIRECCIÓN GENERAL DE CATASTRO FÍSICO

DELEGACIÓN DE GRANADA
DGCF
NICARAGÜENSE DE ESTUDIOS TERRITORIALES

DIRECCIÓN GENERAL DE CATASTRO FÍSICO
PROBADO
DELEGACIÓN DE GRANADA

DEPARTAMENTO DE GRANADA MUNICIPIO DE GRANADA

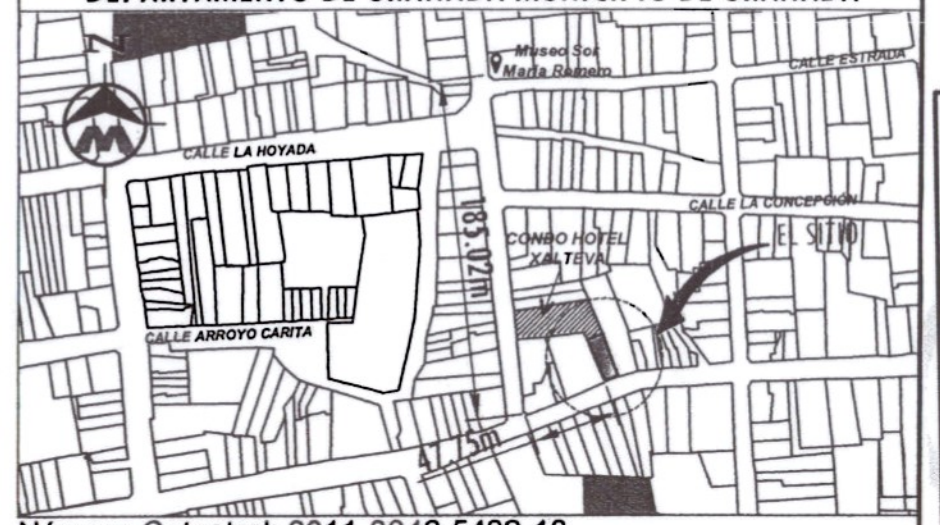

Número Catastral: 6311-3846-5482-13
Planta de Ubicación Sin Escala

COORDENADAS NO VINCULADAS A LA RED GEODESICA DE NICARAGUA

CUADRO DE CONSTRUCCION

LADO EST	LADO PV	RUMBO	DISTANCIA	V	COORDENADAS Y	COORDENADAS X
				1	1,318,637.4050	613,472.5020
1	2	S 68°17'26.09" W	8.200	2	1,318,634.3717	613,464.8833
2	3	N 21°54'00.30" W	0.248	3	1,318,634.6018	613,464.7908
3	4	N 21°53'52.68" W	9.873	4	1,318,643.7625	613,461.1086
4	5	N 23°22'08.03" W	14.644	5	1,318,657.2054	613,455.3000
5	6	N 66°48'47.56" E	9.244	6	1,318,660.8449	613,463.7970
6	7	S 18°52'46.31" E	2.307	7	1,318,658.6623	613,464.5434
7	8	S 20°25'24.12" E	12.651	8	1,318,646.8066	613,468.9580
8	1	S 20°39'15.45" E	10.047	1	1,318,637.4050	613,472.5020

SUPERFICIE = 214.031 m2 = 303.58 Vrs2

MORGAN
Servicios Topograficos
Ing Bosco Javier Morgan
Lic Catastral: BMM100426
Cel: 8883 7568 T

Objeto Lev: Venta Total	Numero Catastral: 6311-3846-5482-13		FIRMA:
Enajenante: Donald Jay Snyder Pasaporte USA: A28963085	Ubicacion: Casa Museo Sor María Romero 185.02 m SE, 47.75 m al Este, Condominio Hotel Xalteva, M/I. Municipio de Granada, Departamento de Granada.		Ejecuta: Ing.Bosco Javier Morgan Lic. Catastral: BMM100426 Cel: 8883-7568 Email: ingmorgan73@gmail.com
Adquiriente: Ramak Jaafar-Nejad Pasaporte: AA334424	Área: 214.031 m2 = 303.58 Vrs2	Escala: 1 / 250	Fecha: 9 de Enero del 2026

Transacción	Cudoc	Objeto Plano	Área (m²)	No. Lote
T-4CGPFJ-001	0041466	TRASPASO TOTAL	214.03	
Parcela Objeto	63113846548213		Documento	W8BZIIP
No. Licencia: BMM100426	Fecha Aprobación: 20/1/2026		Fecha Vencimiento: 20/1/2027 12:30:19	

Fecha: 9 de Enero del 2026

COORDENADAS NO VINCULADAS A LA RED GEODESICA DE NICARAGUA

CUADRO DE CONSTRUCCION

LADO		RUMBO	DISTANCIA	V	COORDENADAS	
EST	PV				Y	X
				1	1,318,637.4050	613,472.5020
1	2	S 68°17'26.09" W	8.200	2	1,318,634.3717	613,464.8833
2	3	N 21°54'00.30" W	0.248	3	1,318,634.6018	613,464.7908
3	4	N 21°53'52.68" W	9.873	4	1,318,643.7625	613,461.1086
4	5	N 23°22'08.03" W	14.644	5	1,318,657.2054	613,455.3000
5	6	N 66°48'47.56" E	9.244	6	1,318,660.8449	613,463.7970
6	7	S 18°52'46.31" E	2.307	7	1,318,658.6623	613,464.5434
7	8	S 20°25'24.12" E	12.651	8	1,318,646.8066	613,468.9580
8	1	S 20°39'15.45" E	10.047	1	1,318,637.4050	613,472.5020

SUPERFICIE = 214.031 m2 = 303.58 Vrs2

FIRMA:

Ejecuta: Ing.Bosco Javier Morgan
Lic. Catastral: BMM100426
Cel: 8883-7568 Email: ingmorgan73@gmail.com