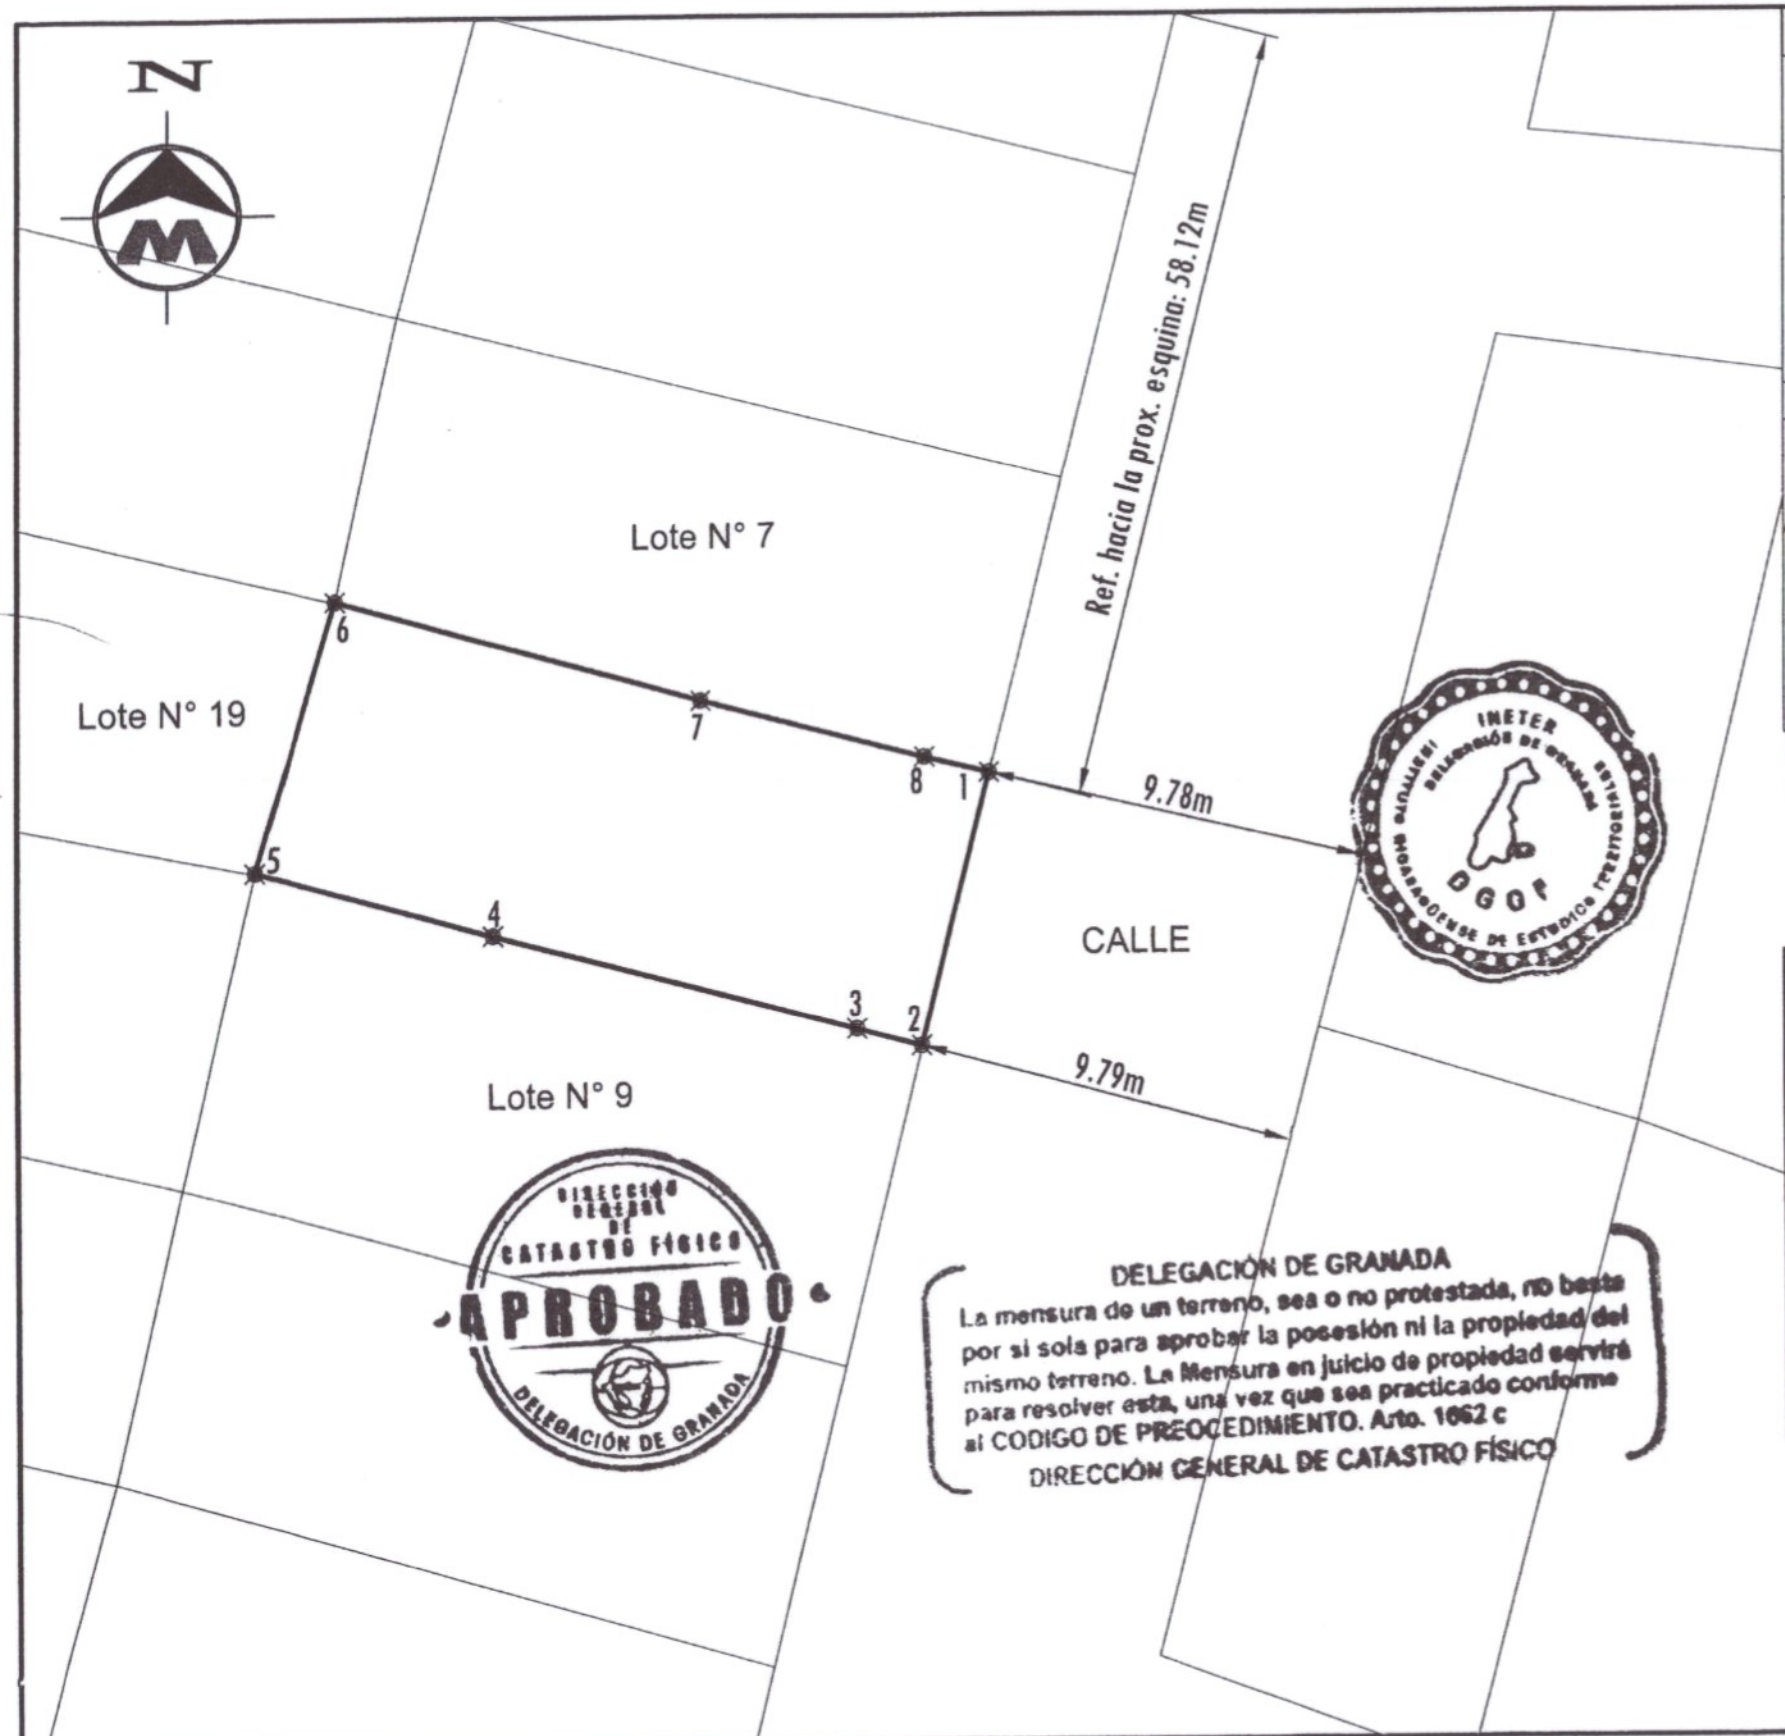

DIRECCIÓN GENERAL DE CATASTRO FÍSICO
APROBADO
DELEGACIÓN DE GRANADA

INETER
DGOT

DELEGACIÓN DE GRANADA
La mensura de un terreno, sea o no protestada, no basta por si sola para aprobar la posesión ni la propiedad del mismo terreno. La Mensura en juicio de propiedad servirá para resolver esta, una vez que sea practicado conforme al CODIGO DE PREOCEDIMIENTO. Arto. 1662 c
DIRECCIÓN GENERAL DE CATASTRO FÍSICO

DEPARTAMENTO DE GRANADA MUNICIPIO DE GRANADA

Planta de Ubicación Sin Escala
Número Catastral: 3051-4-05-089-12400

COORDENADAS NO VINCULADAS A LA RED GEODESICA DE NICARAGUA

CUADRO DE CONSTRUCCION

LADO EST	LADO PV	RUMBO	DISTANCIA	V	COORDENADAS Y	COORDENADAS X
				1	1,318,390.1467	614,442.6338
1	2	S 14°08'43.70" W	8.331	2	1,318,382.0686	614,440.5979
2	3	N 75°15'14.51" W	2.001	3	1,318,382.5778	614,438.6630
3	4	N 75°28'55.41" W	11.251	4	1,318,385.3983	614,427.7712
4	5	N 74°52'25.79" W	7.364	5	1,318,387.3200	614,420.8620
5	6	N 16°30'17.83" E	8.364	6	1,318,395.3394	614,423.0382
6	7	S 74°38'59.01" E	11.389	7	1,318,392.3244	614,434.0214
7	8	S 75°35'01.97" E	6.893	8	1,318,390.6082	614,440.6975
8	1	S 76°35'29.72" E	1.991	1	1,318,390.1467	614,442.6338

SUPERFICIE = 169.908 m2 = 241.00 Vrs2

MORGAN
Servicios Topograficos
Ing Bosco Javier Morgan
Lic. Catastral: BMM100426
Cel: 8883 7568 T

Objeto Lev: Compraventa total	Número Catastral: 3051-4-05-089-12400		FIRMA:
Enajenante: Isabelita del Carmen Arcia Noguera, Ced: 042-120152-0002H Pedro José Sandino Mendoza, Ced: 201-071047-0001W	Ubicación:Rpto Eddy Ruiz, del Restaurante Colinas Sur 3c E, 75 vrs al Norte. Municipio de Granada, Departamento de Granada.		Ejecuta: Ing.Bosco Javier Morgan Lic. Catastral: BMM100426 Cel: 8883-7568 Email: ingmorgan73@gmail.com SERVICIOS TOPOGRAFICOS
Adquiriente: Giovannia Auxiliadora Wellington Alonso, Ced: 201-250681-0002B	Área: 169.908 m2 = 241.00 Vrs2	Escala: 1 /300	Fecha: 21 de Enero del 2026

Transacción	Cudoc	Objeto Plano	
T-4CH4KT-001	0041756	TRASPASO TOTAL	
Parcela Objeto	6311484328 1015		Área (m^2)
			169.91
No. Licencia: BMM100426	Fecha Aprobación: 26/1/2026	Documento	No. Lote
	Fecha Vencimiento: 26/1/2027	W8BZKS2	

Objeto Lev: Compraventa total
Número Catastral: 3051-4-05-089-12400

COORDENADAS NO VINCULADAS A LA RED GEODESICA DE NICARAGUA

CUADRO DE CONSTRUCCION

LADO		RUMBO	DISTANCIA	V	COORDENADAS	
EST	PV				Y	X
				1	1,318,390.1467	614,442.6338
1	2	S 14°08'43.70" W	8.331	2	1,318,382.0686	614,440.5979
2	3	N 75°15'14.51" W	2.001	3	1,318,382.5778	614,438.6630
3	4	N 75°28'55.41" W	11.251	4	1,318,385.3983	614,427.7712
4	5	N 74°52'25.79" W	7.364	5	1,318,387.3200	614,420.6620
5	6	N 16°30'17.83" E	8.364	6	1,318,395.3394	614,423.0382
6	7	S 74°38'59.01" E	11.389	7	1,318,392.3244	614,434.0214
7	8	S 75°35'01.97" E	6.893	8	1,318,390.6082	614,440.6975
8	1	S 76°35'29.72" E	1.991	1	1,318,390.1467	614,442.6338

SUPERFICIE = 169.908 m2 = 241.00 Vrs2

Ejecuta: Ing.Bosco Javier Morgan
Lic. Catastral: BMM100426
Cel: 8883-7568 Email: ingmorgan73@gmail.com
SERVICIOS TOPOGRAFICOS

MORGAN
Servicios Topograficos
Ing Bosco Javier Morgan
Lic Catastral BMM100426
Cel 8883 7568 T