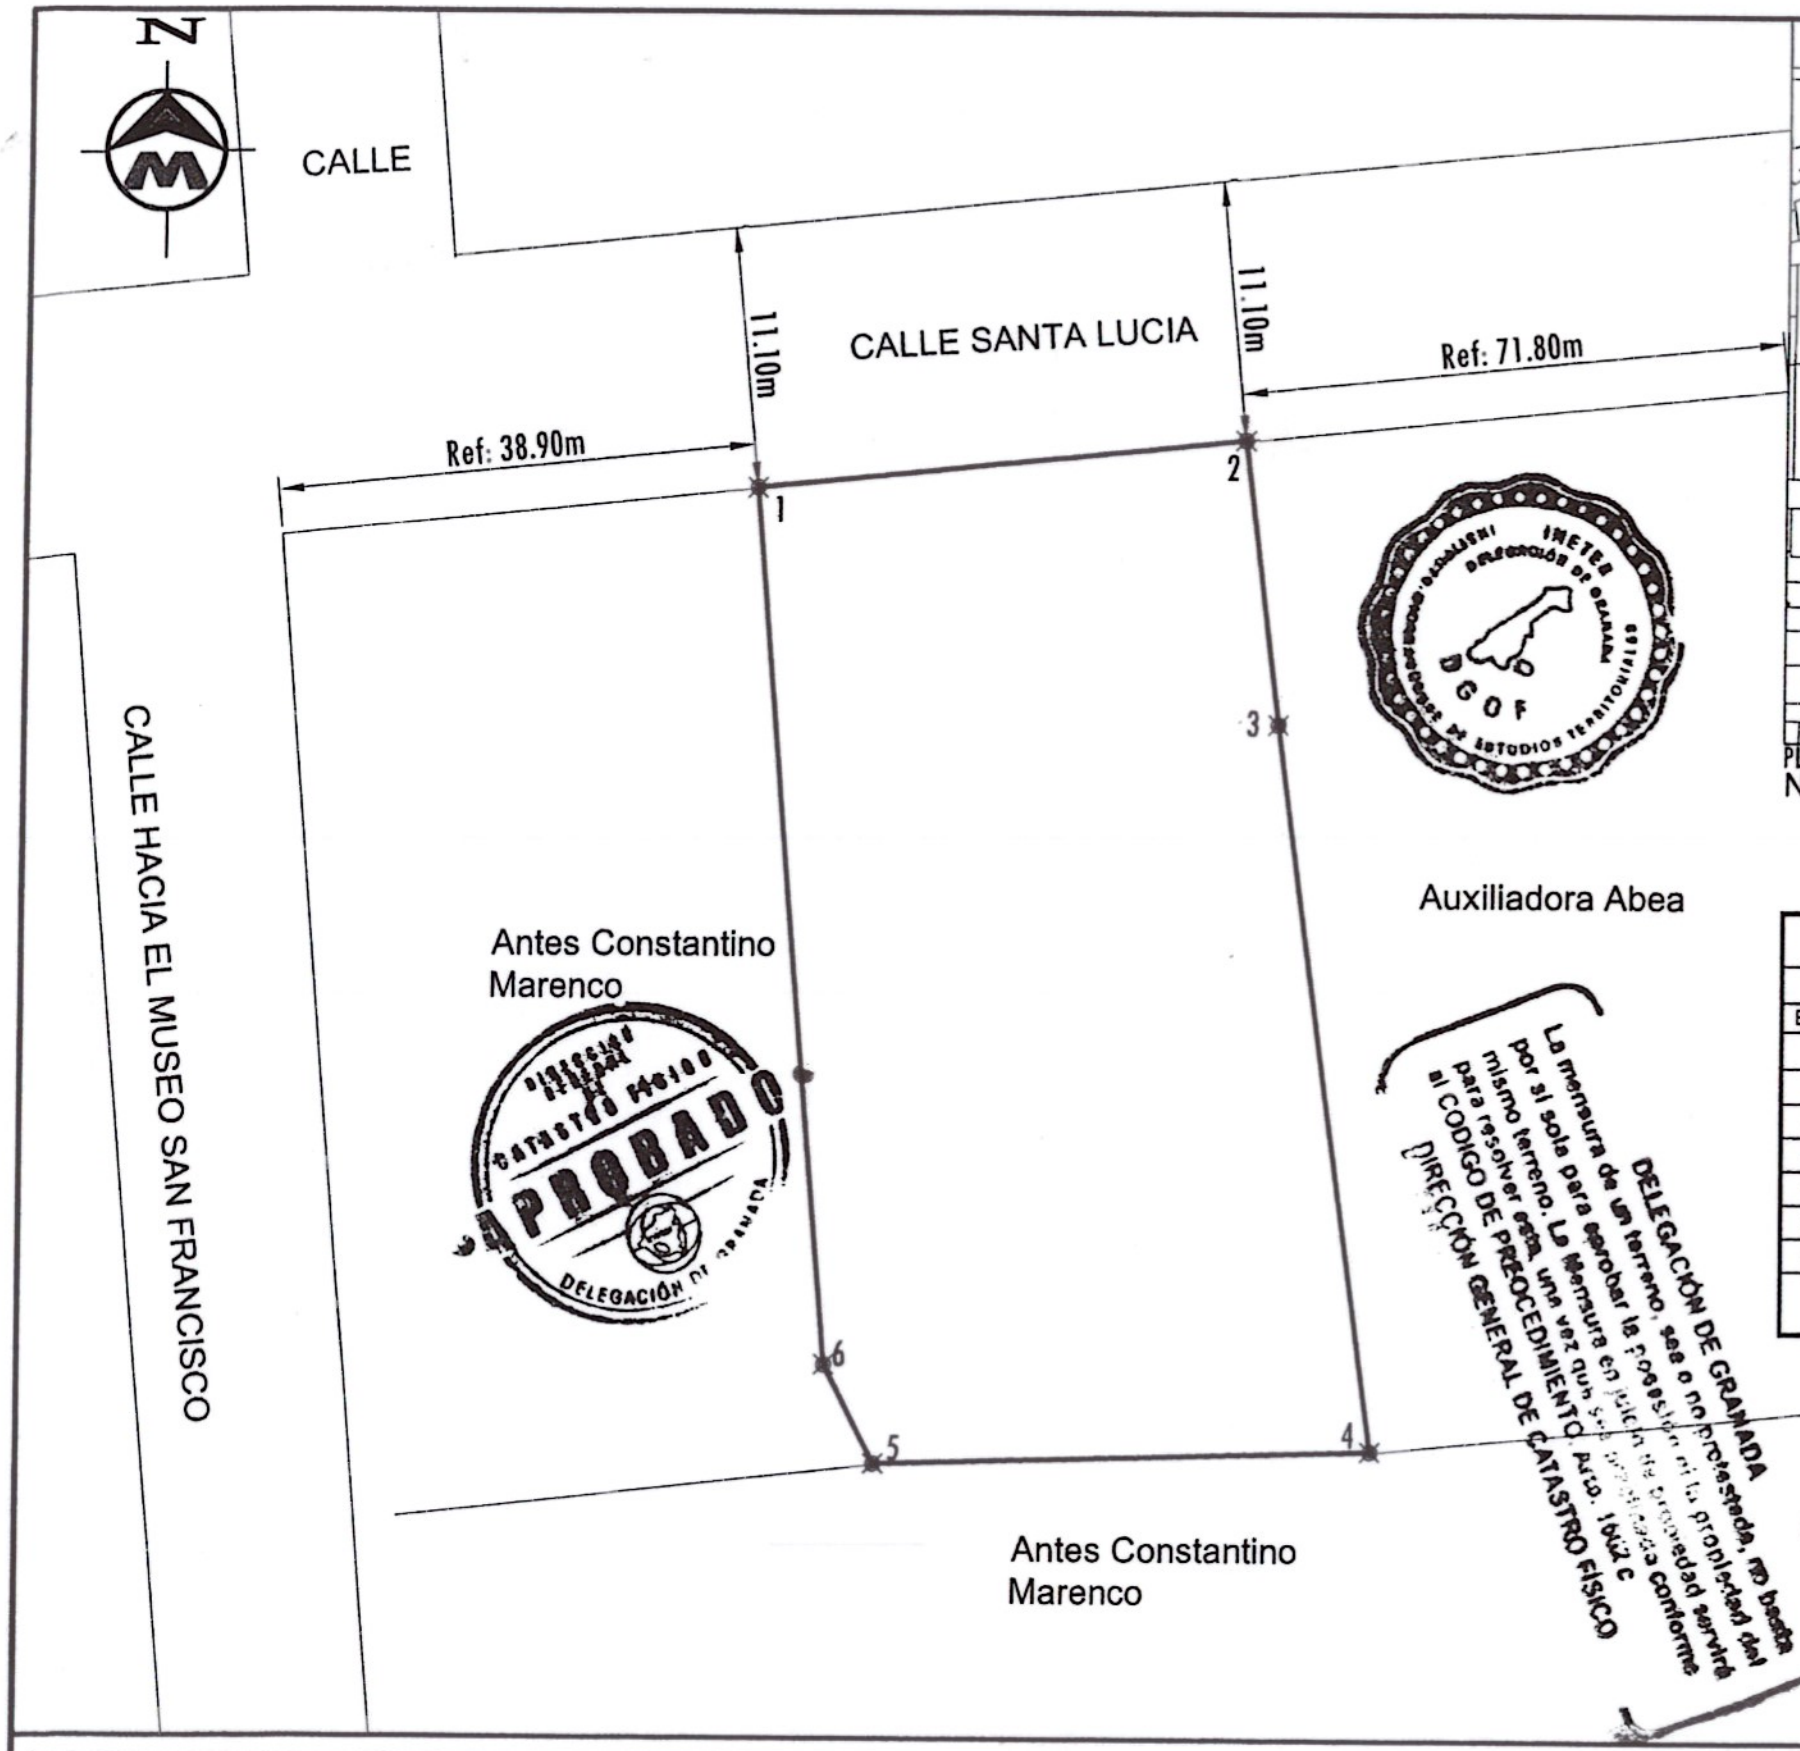

MUNICIPIO DE GRANADA. DEPARTAMENTO DE GRANADA

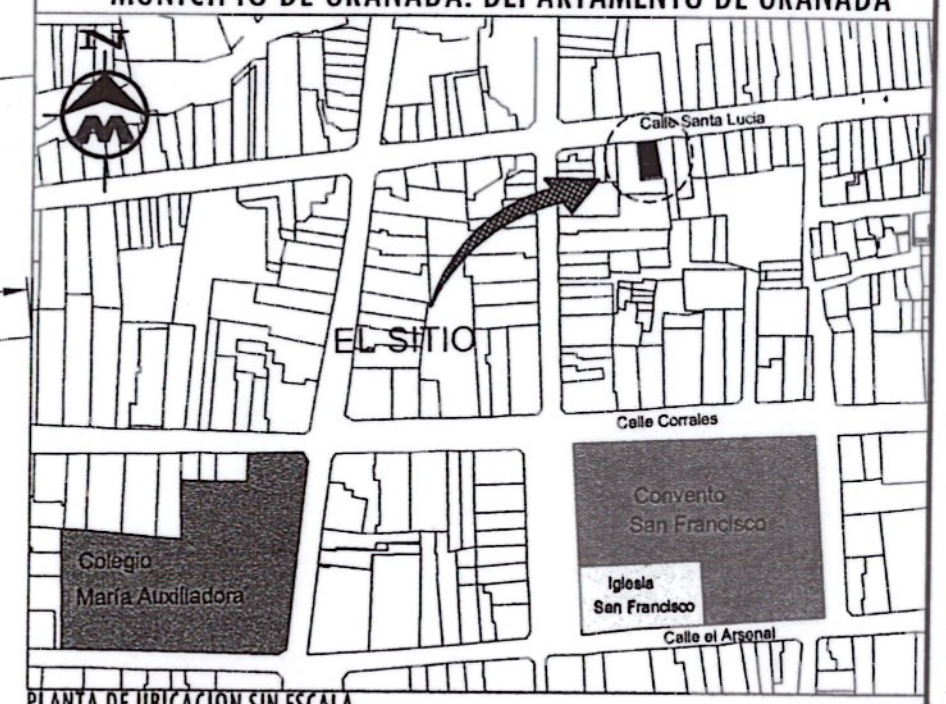

PLANTA DE UBICACION SIN ESCALA

Número Catastral: 6311-4914-0530-17

COORDENADAS NO VINCULADAS A LA RED GEODESICA DE NICARAGUA

CUADRO DE CONSTRUCCION

LADO EST	LADO PV	RUMBO	DISTANCIA	V	COORDENADAS Y	COORDENADAS X
				1	1,319,459.4654	614,096.9865
1	2	N 84°19'27.42" E	9.808	2	1,319,460.4354	614,106.7465
2	3	S 07°00'42.69" E	5.652	3	1,319,454.8254	614,107.4365
3	4	S 07°46'20.24" E	14.474	4	1,319,440.4841	614,109.3939
4	5	S 88°20'51.72" W	9.918	5	1,319,440.1981	614,099.4798
5	6	N 26°40'32.38" W	2.190	6	1,319,442.1554	614,098.4965
6	1	N 04°59'07.63" W	17.376	1	1,319,459.4654	614,096.9865

SUPERFICIE = 201.00 m2 = 285.10 Vrs2

MORGAN
Servicios Topograficos
Ing Bosco Javier Morgan
Lic Catastral: BMM100426
Cel: 8883 7568 T

Nota: Este plano esta ajustado al área registral

Objeto: Venta Total	Número Catastral: 6311-4914-0530-17		FIRMA:
Enajenante: Marco Antonio Jarquin Ruiz, Ced: 201-010264-1000A	Ubicación: De Casa Museo San Francisco 1c al N y ½c al E. Calle Santa Lucia. Municipio de Granada. Dpto Granada.		Ejecuta: Ing.Bosco Javier Morgan Lic. Catastral: BMM100426 Cel: 8883-7568 Email: ingmorgan73@gmail.com www.morganconstrucciones.com
Adquiriente: Joel Fernando Lara Miranda, Ced: 201-140583-0004M	Área: 201.00 m² = 285.10 Vrs²	Escala: 1: 400	Fecha: 19 de Enero del 2026

Transacción	Cudoc	Objeto Plano	No. Lote
T-4CH2D7-001	0041722	TRASPASO TOTAL	W8BZJQ8
Parcela Objeto	63114914053017	Área (m²) 201.00	Documento
No. Licencia: BMM100426	Fecha Aprobación: 22/1/2026		Fecha Vencimiento: 22/1/2027 11:46:10

Objeto: Venta Total
Número Catastral: 6311-4914-0530-17

COORDENADAS NO VINCULADAS A LA RED GEODESICA DE NICARAGUA

CUADRO DE CONSTRUCCION

LADO		RUMBO	DISTANCIA	V	COORDENADAS	
EST	PV				Y	X
				1	1,319,459.4654	614,096.9865
1	2	N 84°19'27.42" E	9.808	2	1,319,460.4354	614,106.7465
2	3	S 07°00'42.69" E	5.652	3	1,319,454.8254	614,107.4365
3	4	S 07°46'20.24" E	14.474	4	1,319,440.4841	614,109.3939
4	5	S 88°20'51.72" W	9.918	5	1,319,440.1981	614,099.4798
5	6	N 26°40'32.38" W	2.190	6	1,319,442.1554	614,098.4965
6	1	N 04°59'07.63" W	17.376	1	1,319,459.4654	614,096.9865

SUPERFICIE = 201.00 m2 = 285.10 Vrs2

Ejecuta: Ing.Bosco Javier Morgan
Lic. Catastral: BMM100426
Cel: 8883-7568 Email: ingmorgan73@gmail.com
www.morganconstrucciones.com

MORGAN
Servicios Topograficos
Ing Bosco Javier Morgan
Lic Catastral BMM100
Cel 8883 7568