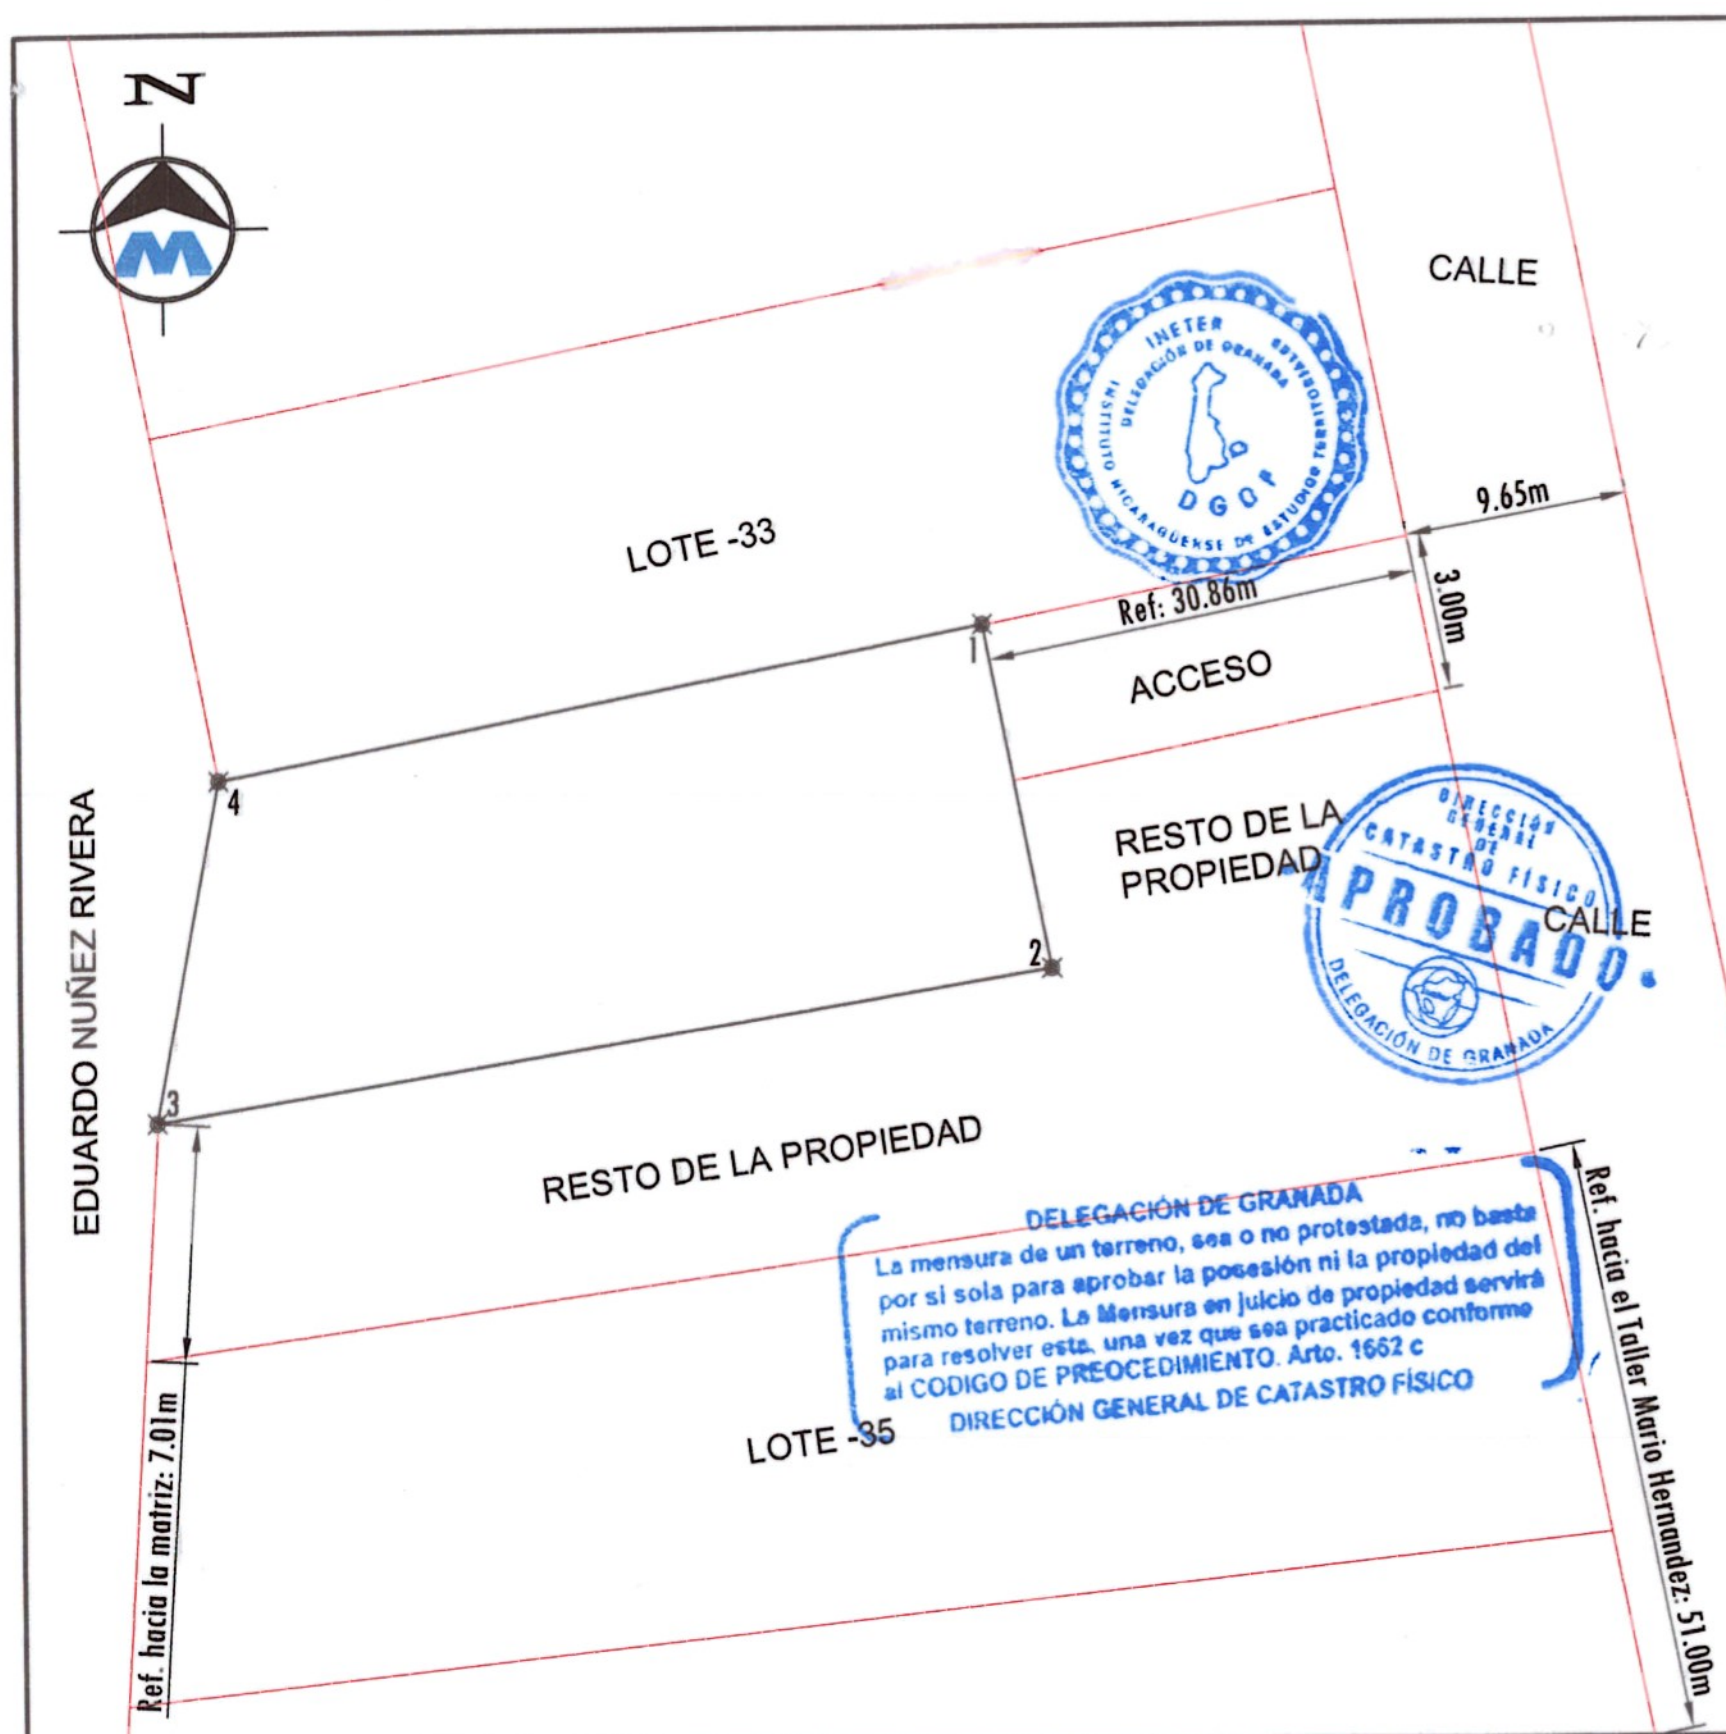

DEPARTAMENTO DE GRANADA MUNICIPIO DE GRANADA

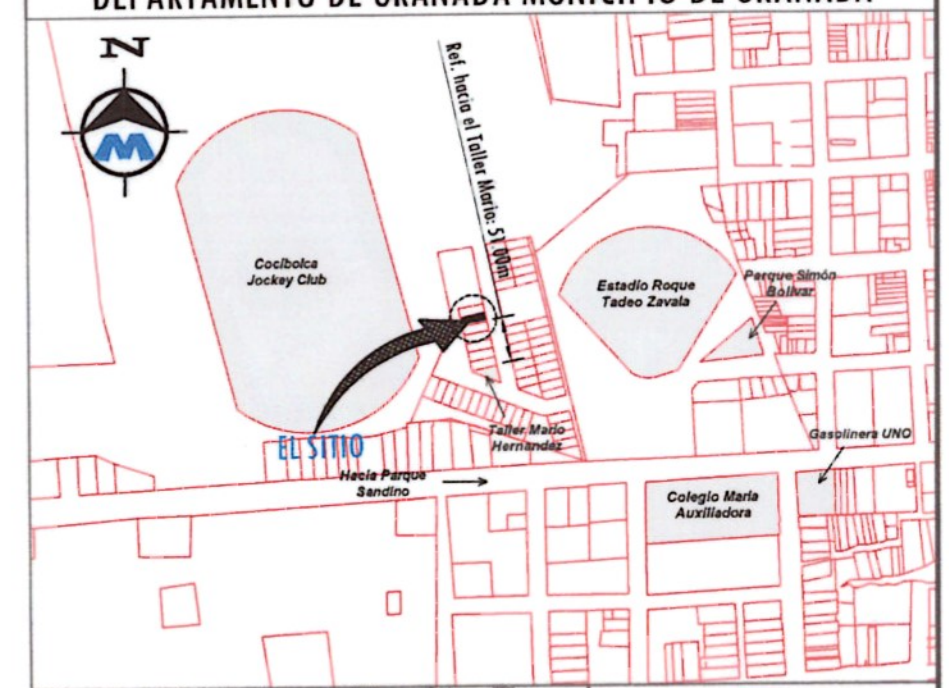

Planta de Ubicación Sin Escala
Número Catastral: 3051-4-05-056-08700

COORDENADAS NO VINCULADAS A LA RED GEODESICA DE NICARAGUA

CUADRO DE CONSTRUCCION

LADO EST	LADO PV	RUMBO	DISTANCIA	V	COORDENADAS Y	COORDENADAS X
				1	1,319,898.0542	612,619.1792
1	2	S 11°10'34.67" E	6.972	2	1,319,891.2145	612,620.5305
2	3	S 80°50'12.17" W	18.141	3	1,319,888.3256	612,602.6208
3	4	N 10°32'12.64" E	6.894	4	1,319,895.1038	612,603.8816
4	1	N 79°04'59.99" E	15.579	1	1,319,898.0542	612,619.1792

SUPERFICIE = 113.186 m2 = 160.54 Vrs2

MORGAN
Servicios Topograficos
Ing Bosco Javier Morgan
Lic Catastral: BMM100426
Cel: 8883 7568 T

Objeto Lev: Donación Parcial	Número Catastral: 3051-4-05-056-08700	FIRMA:
Enajenante: Rosa Aleyda Mendieta Centeno Ced: 203-290973-0002H	Ubicación: Del Taller Mario Hernandez 51.00m al Norte. Municipio de Granada, Departamento de Granada.	Ejecuta: Ing.Bosco Javier Morgan Lic. Catastral: BMM100426 Cel: 8883-7568 Email: ingmorgan73@gmail.com SERVICIOS TOPOGRAFICOS
Adquiriente: José Francisco Zambrana Gorgona, Ced: 201-170549-0002B Candy Fatima Herrera, Pasaporte: 642392597	Área: 113.186 m² = 160.54 Vrs² Escala: 1 /200	Fecha: 19 de Enero del 2026

Transacción	Cudoc	Objeto Plano	Área (m²)	No. Lote
T-4CH2CX-001	0041721	DESMEMBRACIÓN	113.19	

Parcela Objeto		Documento	
6311296828423		W8BZK1E	

No. Licencia: BMM100426	Fecha Aprobación: 22/1/2026	Fecha Vencimiento: 22/1/2027

Objeto Lev: Donación Parcial
Número Catastral: 3051-4-05-056-08700

COORDENADAS NO VINCULADAS A LA RED GEODESICA DE NICARAGUA

CUADRO DE CONSTRUCCION

LADO		RUMBO	DISTANCIA	V	COORDENADAS	
EST	PV				Y	X
				1	1,319,898.0542	612,619.1792
1	2	S 11°10'34.67" E	6.972	2	1,319,891.2145	612,620.5305
2	3	S 80°50'12.17" W	18.141	3	1,319,888.3256	612,602.6208
3	4	N 10°32'12.64" E	6.894	4	1,319,895.1038	612,603.8816
4	1	N 79°04'59.99" E	15.579	1	1,319,898.0542	612,619.1792

SUPERFICIE = 113.186 m2 = 160.54 Vrs2

MORGAN
Servicios Topograficos
Ing Bosco Javier Morgan
Lic Catastral BMM100426
Cel 8883 7568 T

Ejecuta: Ing.Bosco Javier Morgan
Lic. Catastral: BMM100426
Cel: 8883-7568 Email: ingmorgan73@gmail.com
SERVICIOS TOPOGRAFICOS