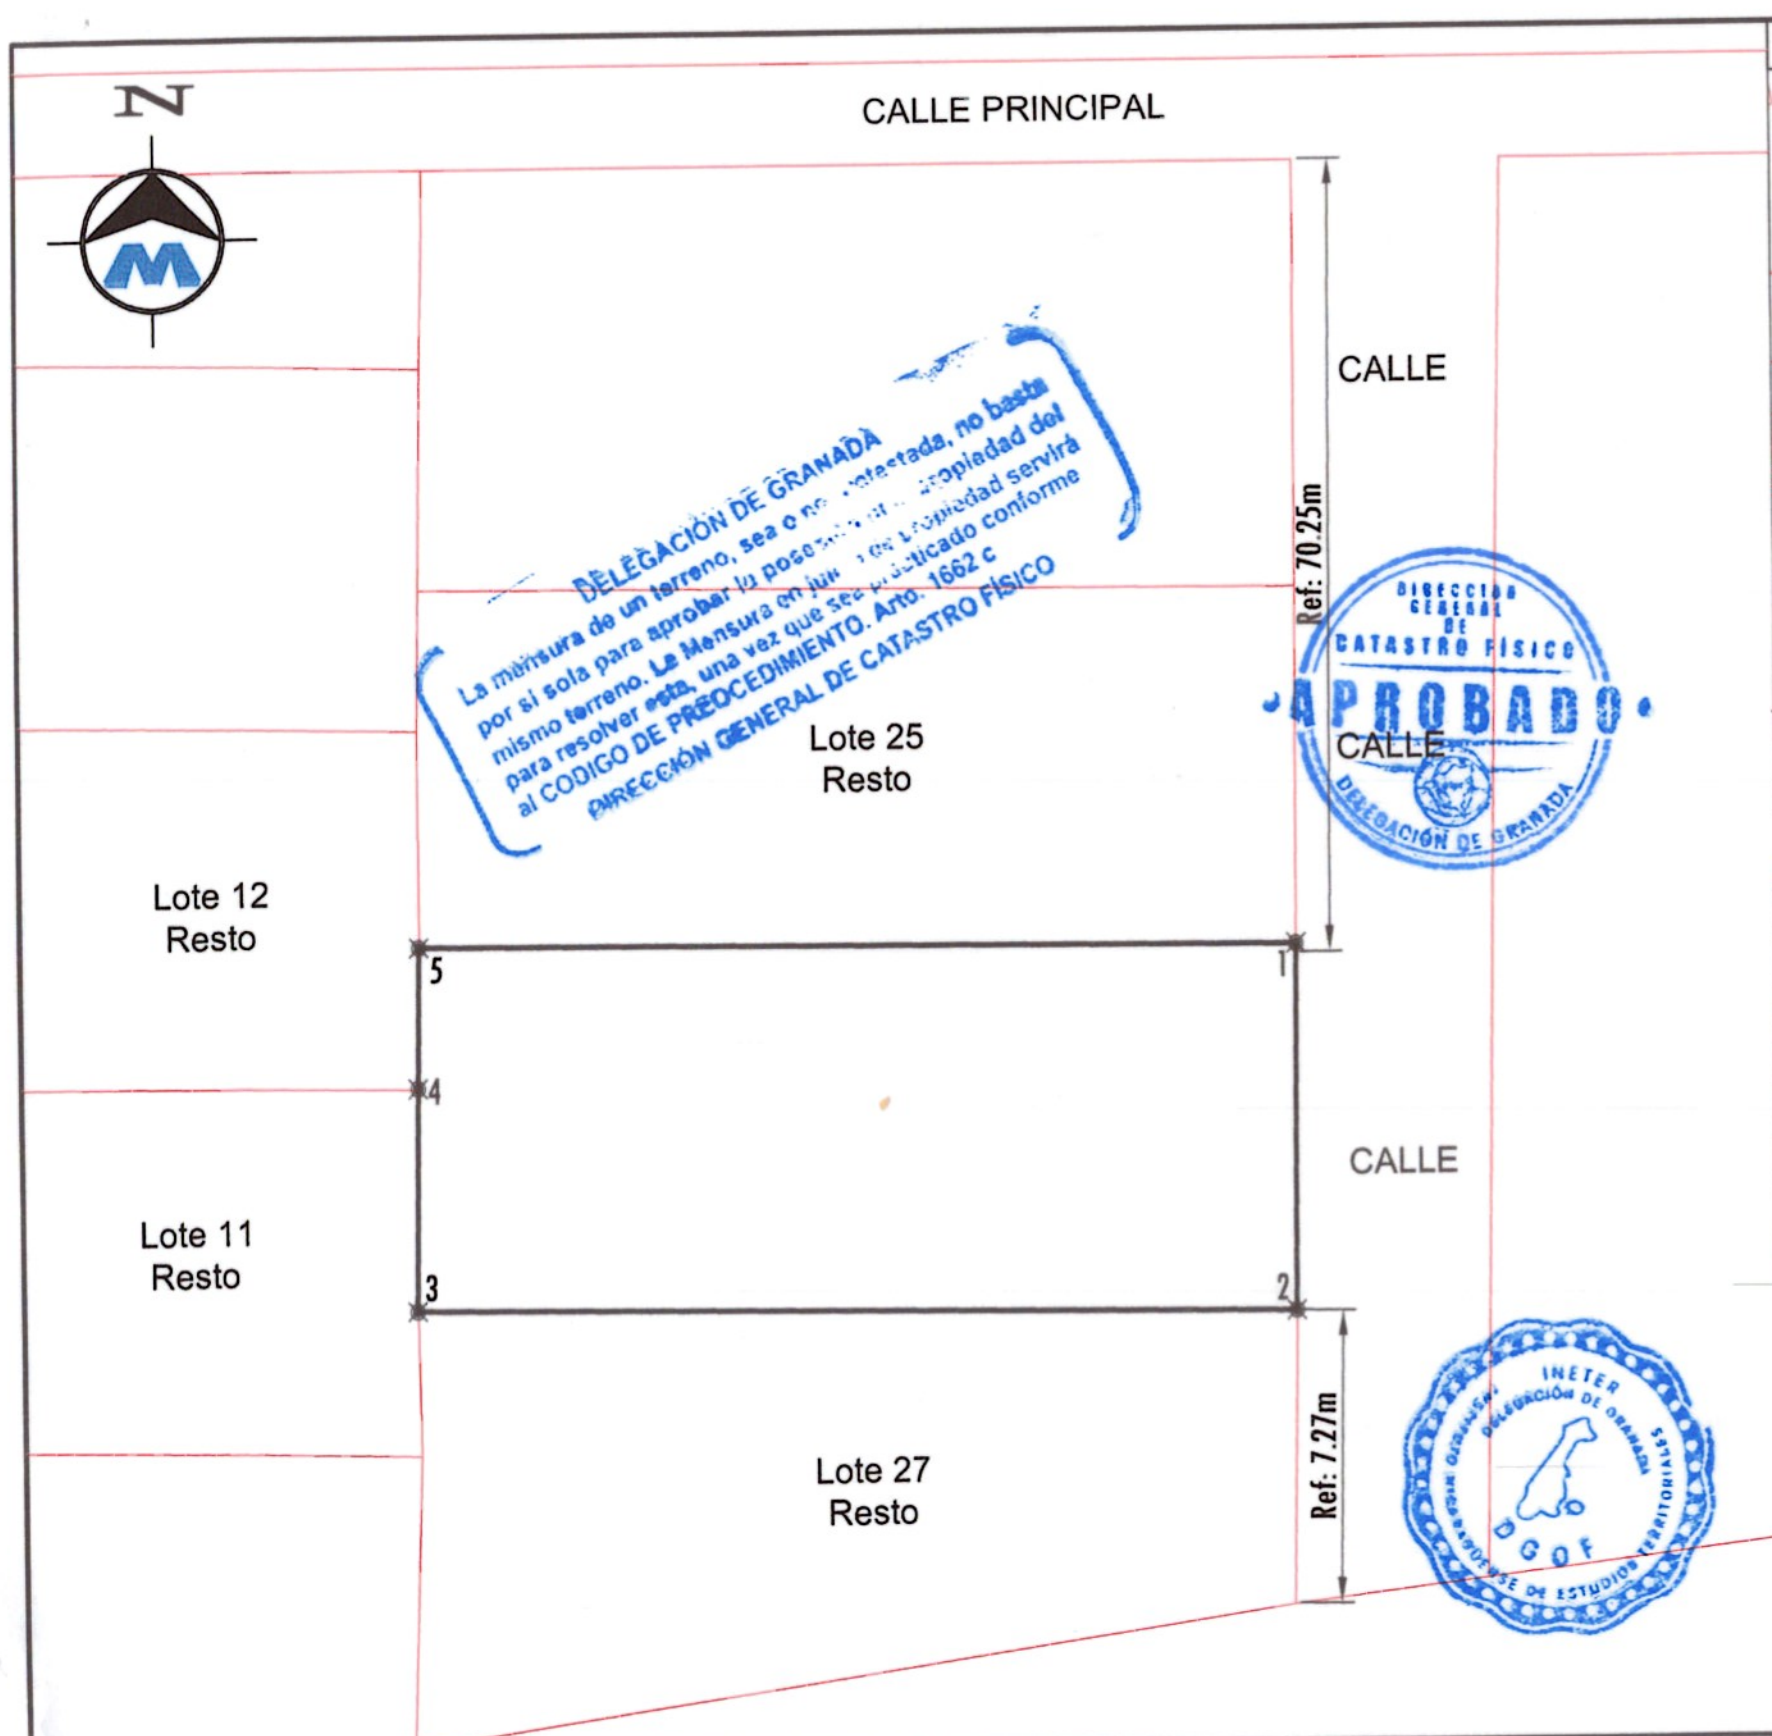

DEPARTAMENTO DE GRANADA MUNICIPIO DE GRANADA

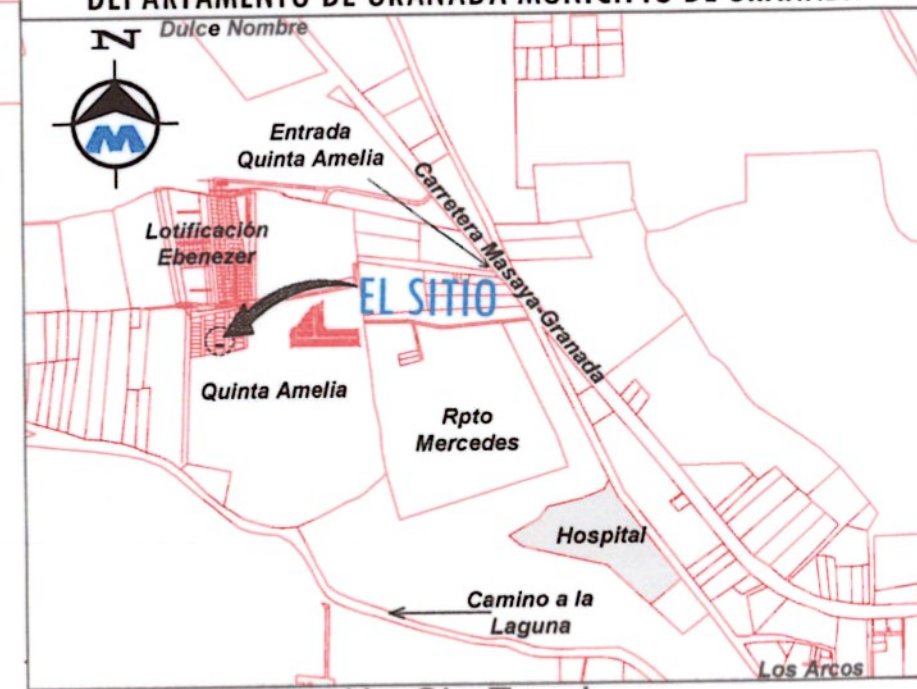

Planta de Ubicación Sin Escala

Número Catastral: 3051-4-05-000-04506

COORDENADAS NO VINCULADAS A LA RED GEODESICA DE NICARAGUA

CUADRO DE CONSTRUCCION

LADO EST	LADO PV	RUMBO	DISTANCIA	V	COORDENADAS Y	COORDENADAS X
				1	1,320,278.0848	610,582.0972
1	2	S 00°27'44.79" W	8.894	2	1,320,269.1911	610,582.0254
2	3	N 89°43'03.37" W	21.989	3	1,320,269.2995	610,560.0363
3	4	N 00°08'28.42" W	5.543	4	1,320,274.8420	610,560.0226
4	5	N 00°15'21.15" E	3.477	5	1,320,278.3186	610,560.0381
5	1	S 89°23'33.84" E	22.060	1	1,320,278.0848	610,582.0972

SUPERFICIE = 197.329 m2 = 279.89 Vrs2

MORGAN
Servicios Topograficos
Ing Bosco Javier Morgan
Lic Catastral: BMM100426
Cel: 8883 7568 T

Objeto Lev: Venta Parcial (Desmembración)	Número Catastral: 3051-4-05-000-04506			FIRMA:	SELLO
Enajenante: Francisco Javier Pedreira Pardo Ced: 22012008016	Ubicación: Cmca. La Laguna, costado Sur Rpto Ebenezer, calle por medio 70.25m al Sur, Lote 26. Municipio de Granada Departamento de Granada.			Ejecuta: Ing. Bosco Javier Morgan Lic. Catastral: BMM100426 Cel: 8883-7568 Email: ingmorgan73@gmail.com SERVICIOS TOPOGRAFICOS	
Adquiriente: Milton Javier Zavala Ced: 201-280604-1005R	Área: 197.329 m² = 279.89 Vrs²	Factor de escala: 1.418415	Escala: 1 /250	Fecha: 26 de Enero del 2026	

Transacción	Cudoc	Objeto Plano	No. Lote
T-4CHCQJ-001	0041879	DESMEMBRACIÓN	W8BZ034
Parcela Objeto	63120052773118	Área (m²)	Documento
No. Licencia: DRS101081	Fecha Aprobación: 3/2/2026	197.32	Fecha Vencimiento: 3/2/2027

Objeto Lev: Venta Parcial (Desmembración)
Número Catastral: 3051-4-05-000-04506

COORDENADAS NO VINCULADAS A LA RED GEODESICA DE NICARAGUA

CUADRO DE CONSTRUCCION

LADO		RUMBO	DISTANCIA	V	COORDENADAS	
EST	PV				Y	X
				1	1,320,278.0848	610,582.0972
1	2	S 00°27'44.79" W	8.894	2	1,320,269.1911	610,582.0254
2	3	N 89°43'03.37" W	21.989	3	1,320,269.2995	610,560.0363
3	4	N 00°08'28.42" W	5.543	4	1,320,274.8420	610,560.0226
4	5	N 00°15'21.15" E	3.477	5	1,320,278.3186	610,560.0381
5	1	S 89°23'33.84" E	22.060	1	1,320,278.0848	610,582.0972

SUPERFICIE = 197.329 m2 = 279.89 Vrs2

Ejecuta: Ing. Bosco Javier Morgan
Lic. Catastral BMM100426
Cel: 8883-7568 Email: ingmorgan73@gmail.com
SERVICIOS TOPOGRAFICOS

MORGAN
Servicios Topograficos
Ing. Bosco Javier Morgan
Lic. Catastral BMM100426
Cel: 8883 7568 T