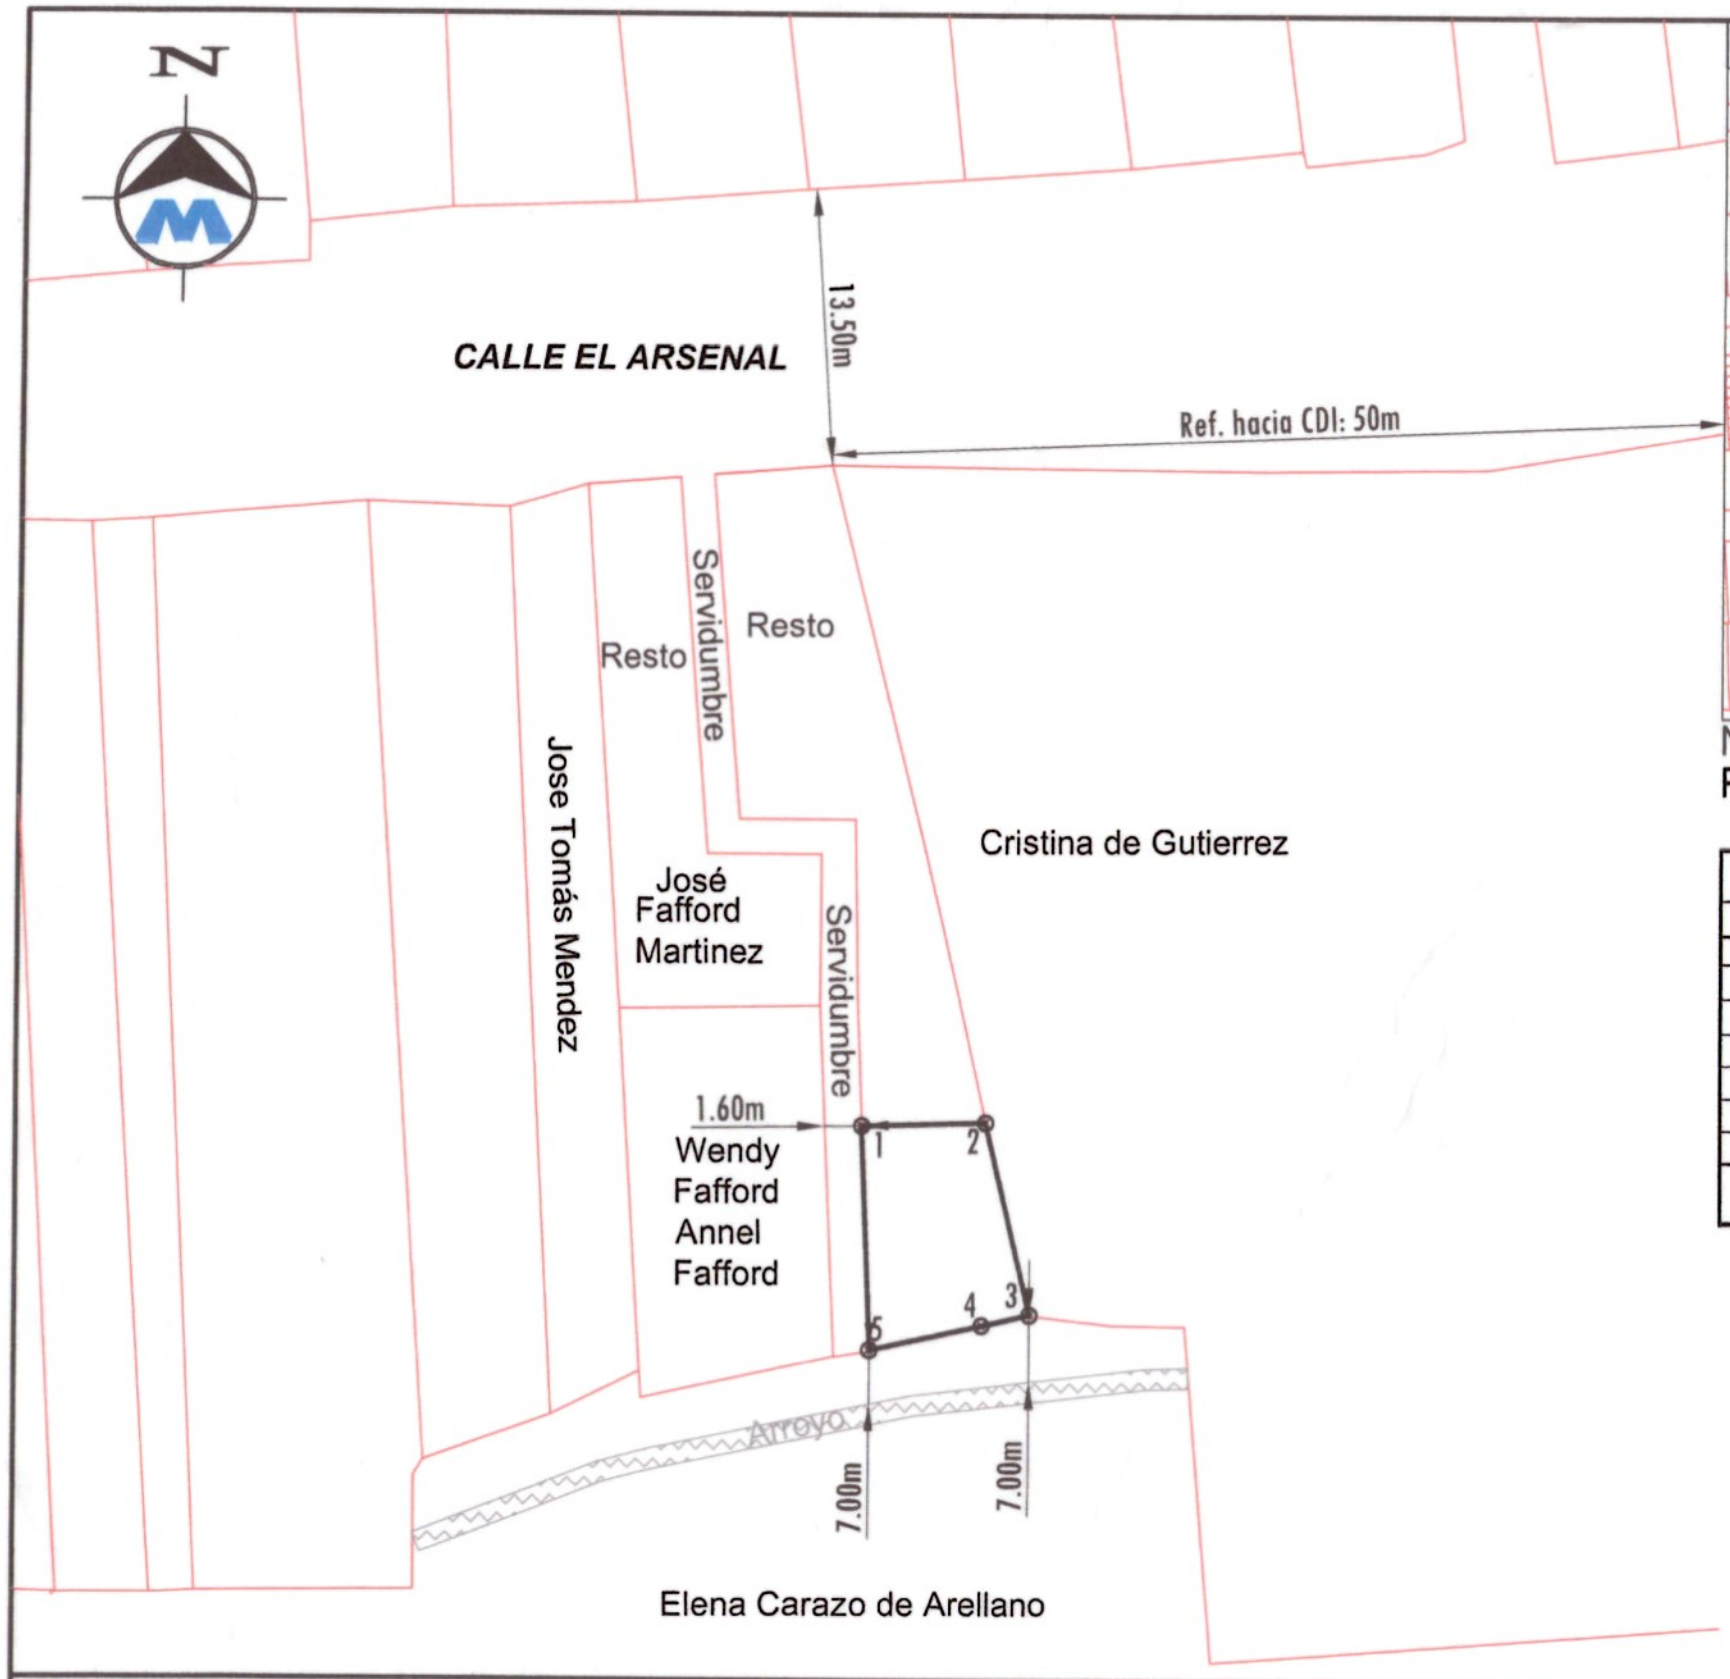

DEPARTAMENTO DE GRANADA MUNICIPIO DE GRANADA

Número Catastral: 3051-4-05-069-12010

Planta de Ubicación Sin Escala

COORDENADAS NO VINCULADAS A LA RED GEODESICA DE NICARAGUA

CUADRO DE CONSTRUCCION

LADO EST	LADO PV	RUMBO	DISTANCIA	V	COORDENADAS Y	COORDENADAS X
				1	1,319,214.0719	614,638.2897
1	2	N 88°28'00.00" E	6.404	2	1,319,214.2433	614,644.6912
2	3	S 13°23'42.00" E	10.090	3	1,319,204.4278	614,647.0287
3	4	S 77°36'06.00" W	2.540	4	1,319,203.8824	614,644.5480
4	5	S 77°36'06.00" W	5.940	5	1,319,202.6071	614,638.7465
5	1	N 02°16'54.00" W	11.474	1	1,319,214.0719	614,638.2897

SUPERFICIE: 79.511 m2 = 112.78 Vrs2

ESPACIO PARA ESQUELA

Objeto Lev: Verificación de Área	Número Catastral: 3051-4-05-069-12010	FIRMA:
Propietario: Manuel Salvador Fafford Martinez Tomo: 10018 Folio: 130	Ubicación: Bajada de la Calle el Arsenal, del CDI 50m al O. Municipio de Granada, Departamento de Granada.	Ejecuta: Ing.Bosco Javier Morgan Lic. Catastral: BMM100426 Cel: 8883-7568 Email: ingmorgan73@gmail.com servicios topograficos
Solicitante: Balford Jovanny Fafford Mena Ced: 201-030484-1000J	Área: 79.511 m² = 112.78 Vrs² / Escala: 1 / 500	Fecha: 23 de Julio 2025