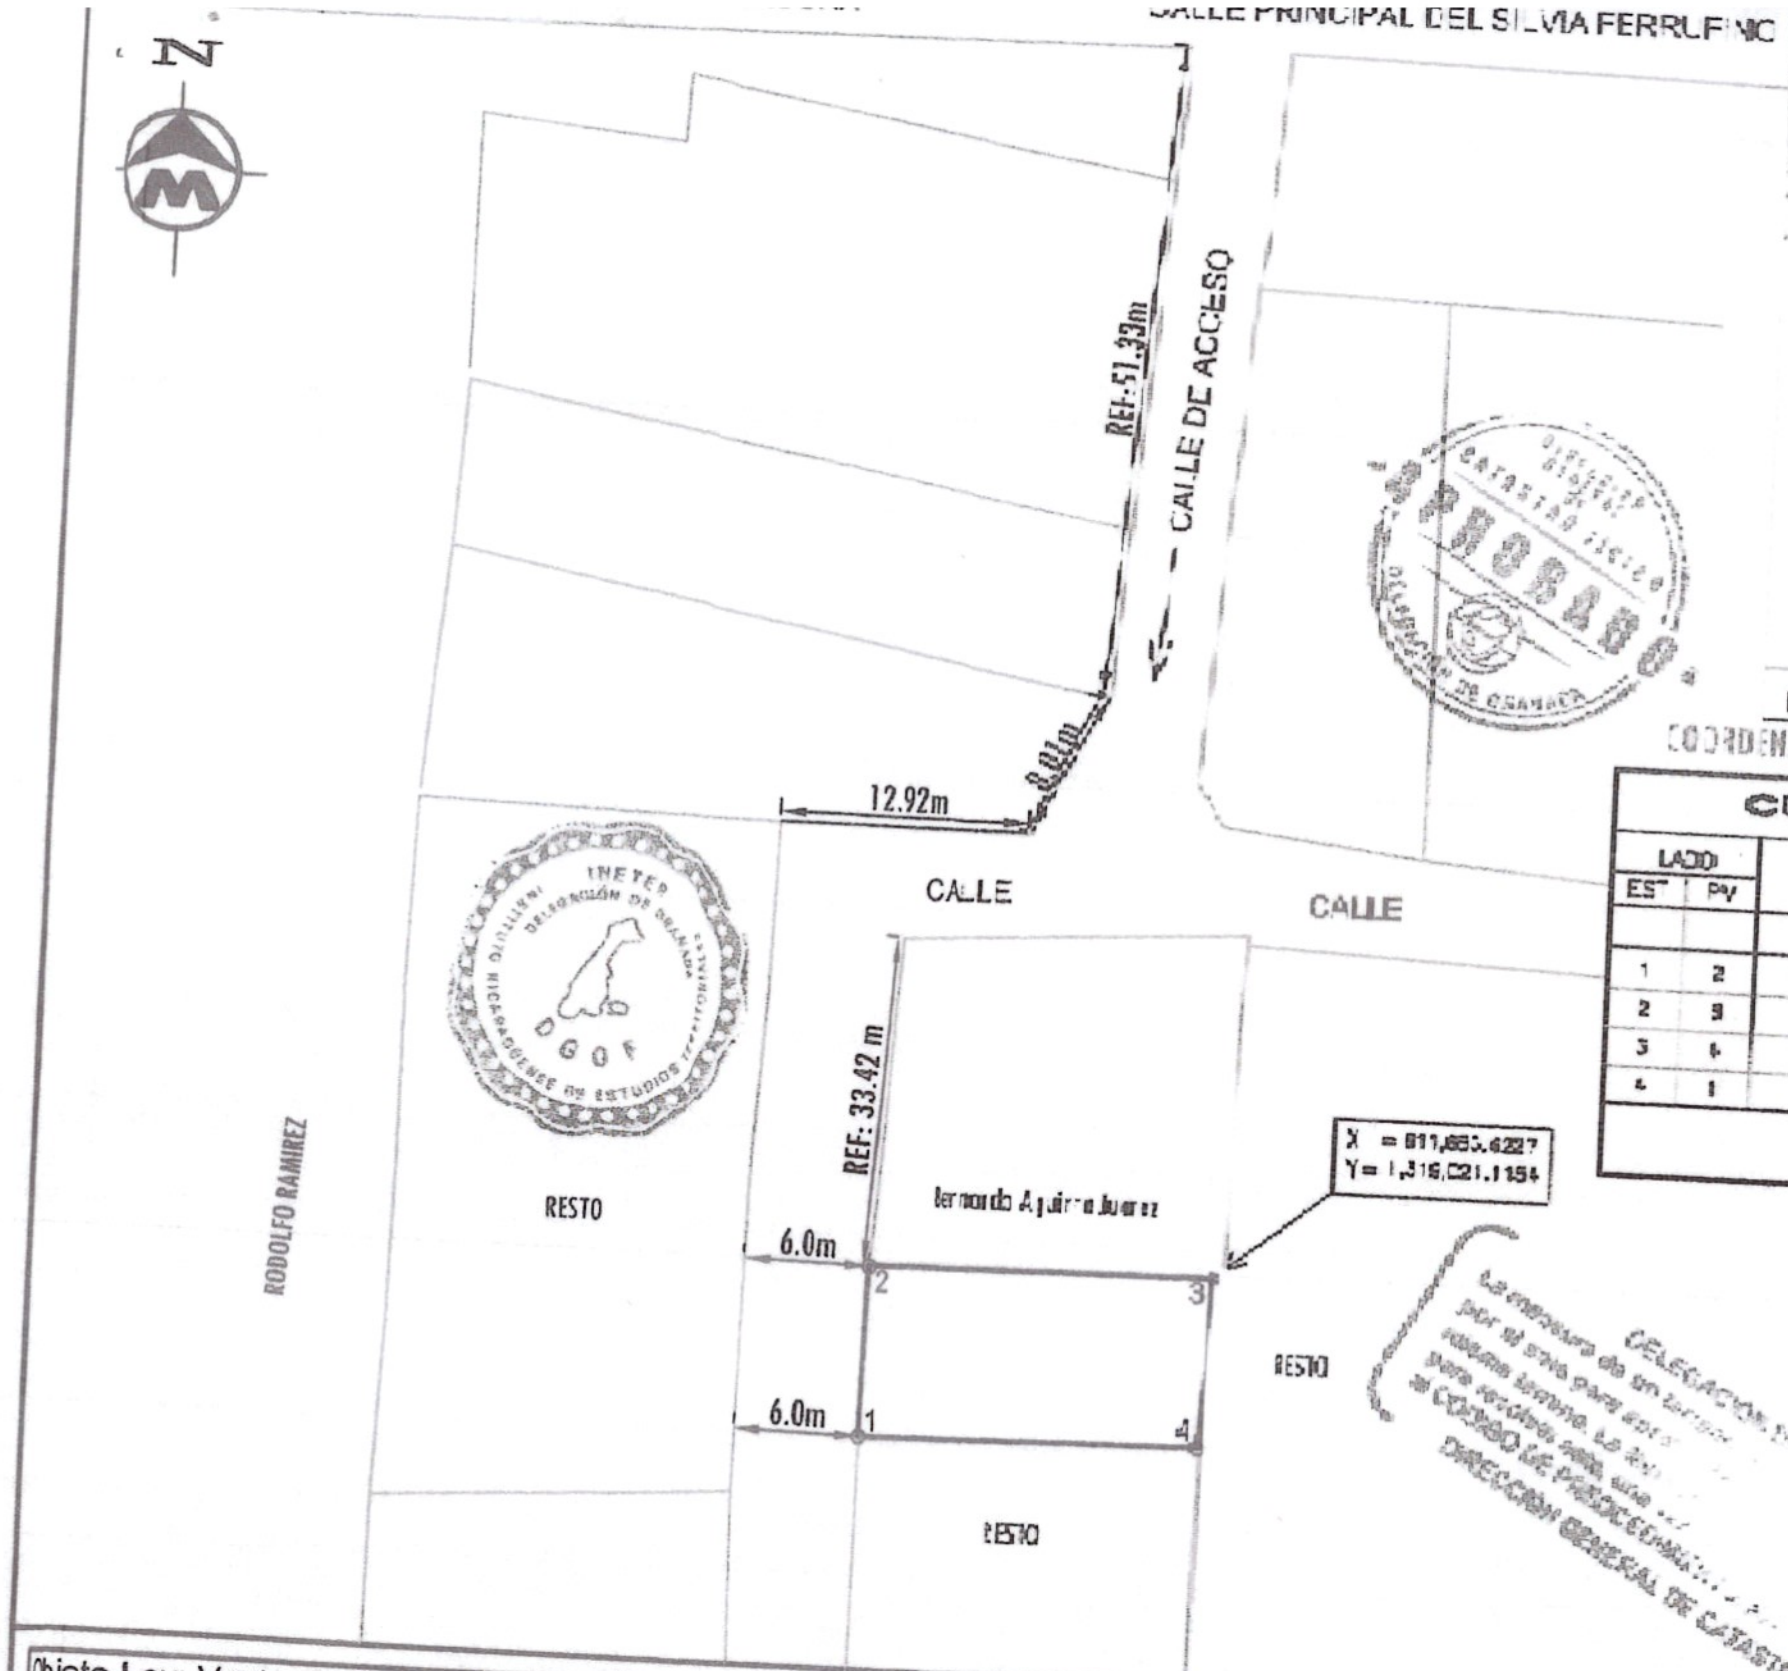

Numero Catastro: 3051-4-05-000-08620 PLANTA DE UBICACION S/N ESCALA

COORDENADAS NO VINCULADAS AL SISTEMA NACIONAL DE COORDENADAS

CUADRO DE CONSTRUCCION

LADO EST	LADO PV	RUMBO	DISTANCIA	V	COORDENADAS Y	COORDENADAS X
1	2	N 01°24'38.61" E	8.529	2	1,319,012.5014	811,655.5188
2	3	N 88°43'14.84" E	17.884	3	1,319,021.0292	811,638.7288
3	4	S 02°16'09.42" W	8.422	4	1,319,021.1154	811,653.6227
4	1	S 88°10'48.88" W	17.698	1	1,319,012.7253	811,653.2156
					1,319,012.5014	811,655.5188

SUPERFICIE = 150.673 m2

Objeto Lev: Venta de Parte Indivisa	Numero Catastro: 3051-4-05-000-08620	FIRMA	SELLO
Enajenante: Augusto Cesar Marenco Balladares Cédula: 201-151237-0005L	UBICACION: De la primera entrada al Reparto Silvia Ferrufino 379m W 51.33 m al S. 8.00 Mts S-W y 12.92 m Oeste, 33.42m S. Municipio de Granada. Departamento de Granada.	Ejecuta: Ing Bosco Javier Morgan Lic. Catastral: BMM100426 Cel 8883-7566 Email: morganjr2@gmail.com SERVICIOS TOPOGRAFICOS	
Adquirientes: Maria Yolanda Arcia Noguera Cédula: 201-091074-0002F	AREA= 150.673 m²= 213.716vrs2 Escala: 1:500	Fecha: 05 de junio del 2025	

Transacción T-46AADL-001	Cuenta 0035280	Objeto Plano	
Parcela Objeto No. Licencia: BMM100426	63111960646019-29	DESMEMBRACION	150.67
Fecha Aprobación: 10/6/2025	Fecha Vencimiento: 10/6/2026	Documento WSWX5QA	No. Lote

MORGAN
Servicios Topograficos
Ing Bosco Javier Morgan
Lic. Catastral BMM100426

Objeto Lev: Venta de Parte Indivisa

Numero Catastral: 3051-4-05-000-08620

Fecha: 05 de junio del 2025

CUADRO DE CONSTRUCCION

LADO		RUMBO	DISTANCIA	V	COORDENADAS	
EST	PV				Y	X
				1	1,319,012.5014	611,635.5188
1	2	N 01°24'38.91" E	8.529	2	1,319,021.0282	611,635.7288
2	3	N 89°43'14.84" E	17.894	3	1,319,021.1154	611,653.6227
3	4	S 02°46'09.42" W	8.422	4	1,319,012.7033	611,653.2158
4	1	S 89°20'46.89" W	17.698	1	1,319,012.5014	611,635.5188

SUPERFICIE = 150.673 m2

Ejecuta: Ing.Bosco Javier Morgan
Lic. Catastral: BMM100426
Cel: 8883-7568 Email: ingmorgan73@gmail.com
SERVICIOS TOPOGRAFICOS

MORGAN
Servicios Topograficos
Ing Bosco Javier Morgan
Lic Catastral: BMM100426
Cel: 8883 7568 T