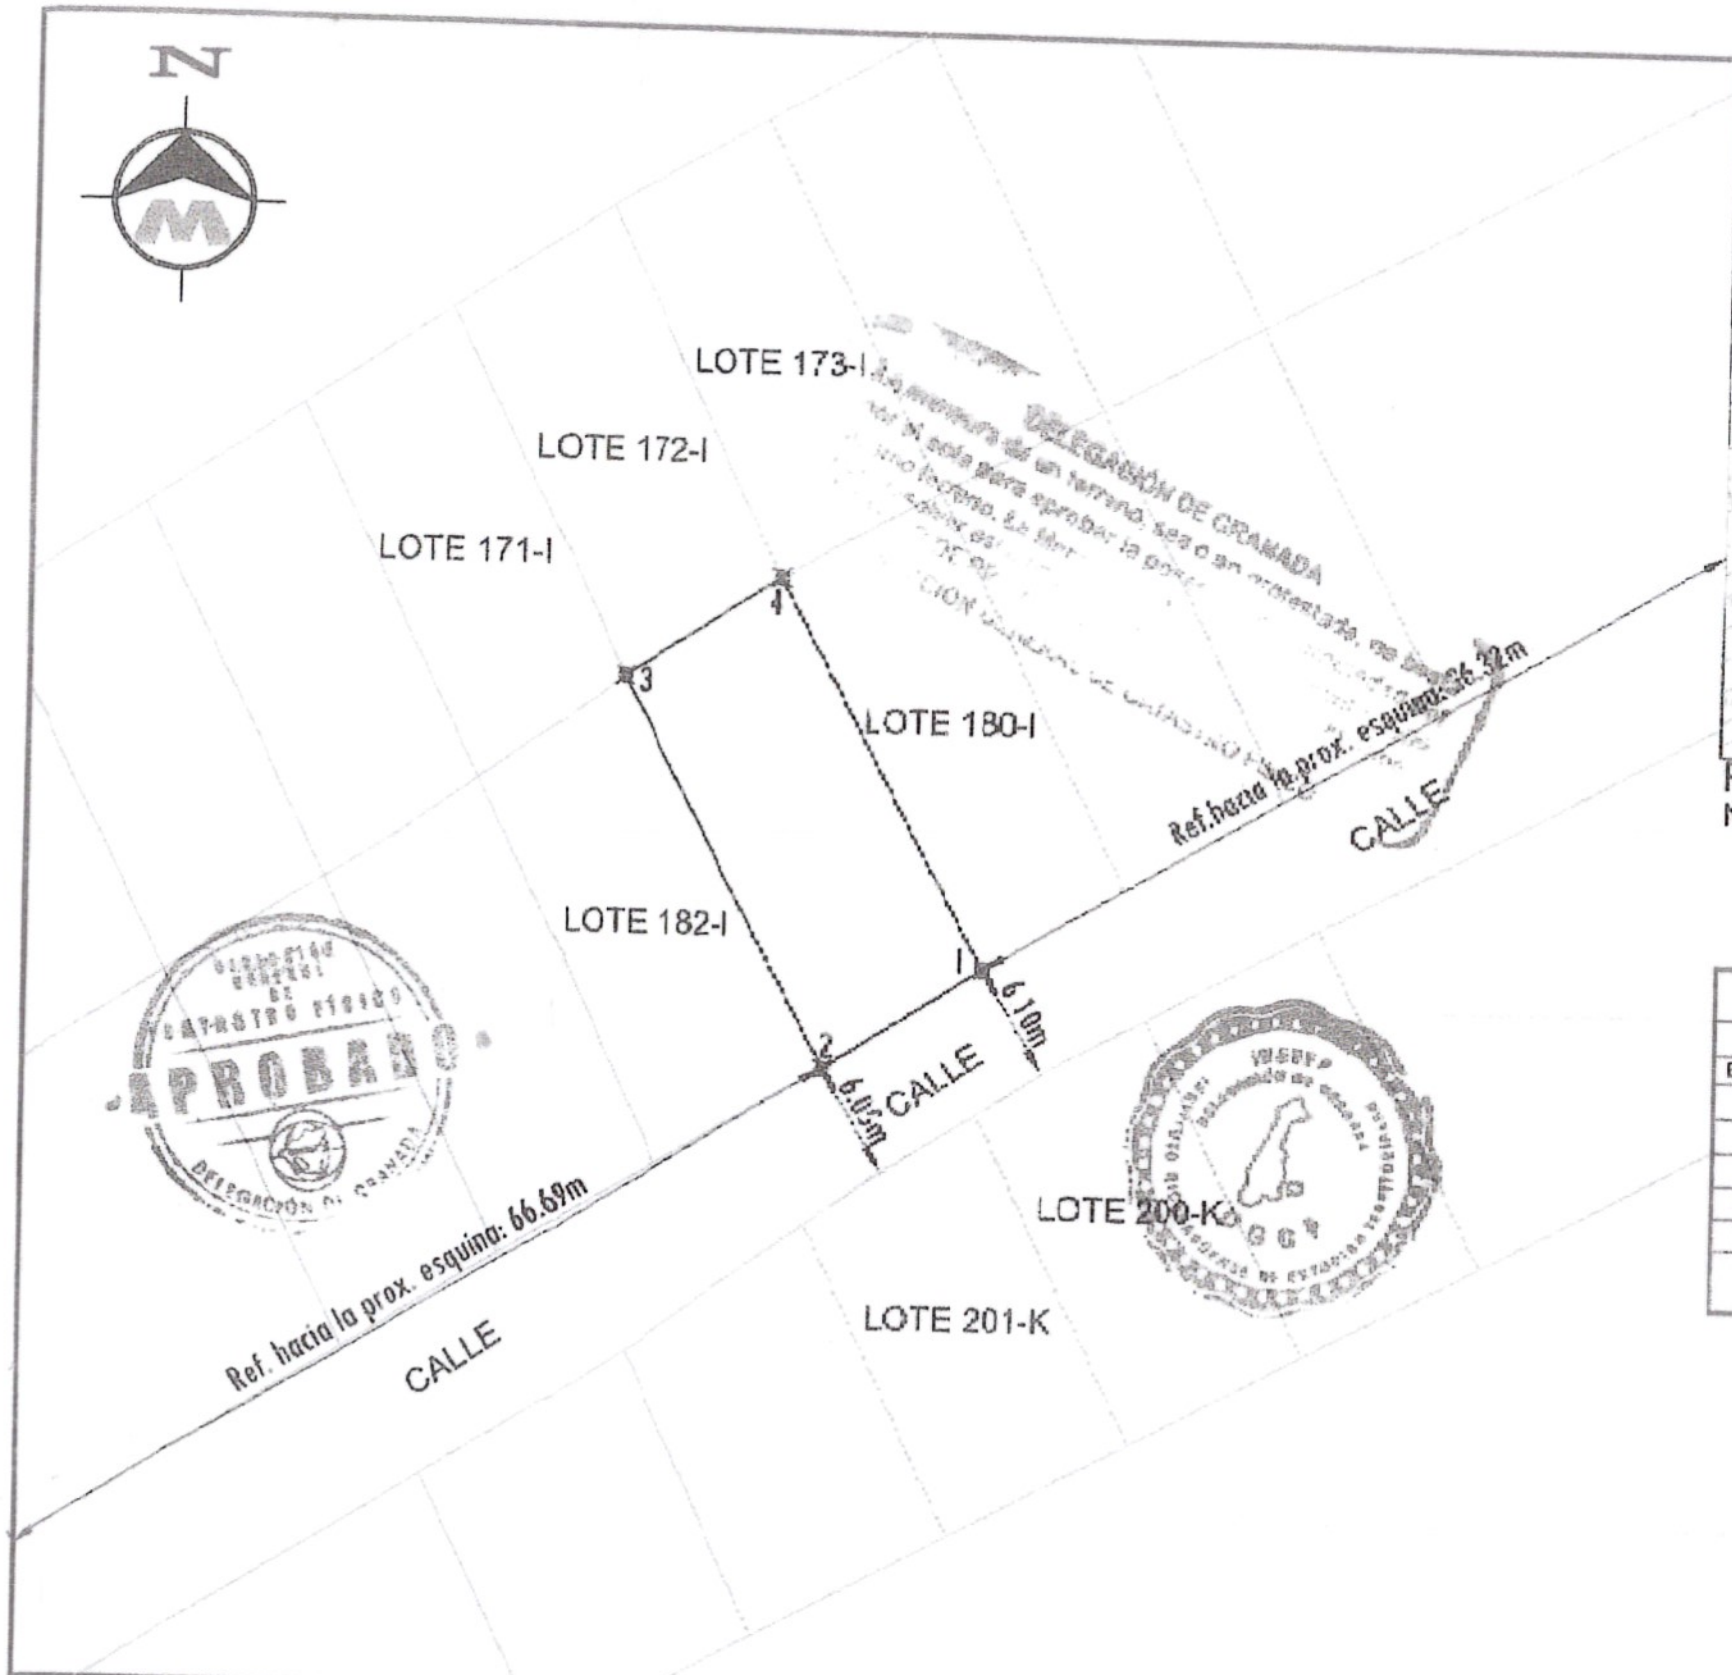

Planta de Ubicación Sin Escala
Número Catastral: 63112820069614

COORDENADAS NO VINCULADAS A LA RED GEODESICA DE NICARAGUA

CUADRO DE CONSTRUCCION

LADO EST	LADO PV	RUMBO	DISTANCIA	V	COORDENADAS Y	COORDENADAS X
				1	1.316.071.8890	611.219.9891
1	2	S 57°43'38.13" W	9.710	2	1.316.066.4882	611.210.7536
2	3	N 29°06'54.76" W	22.816	3	1.316.086.2498	611.199.7498
3	4	N 57°43'54.65" E	9.712	4	1.316.091.4482	611.207.9873
4	1	S 29°06'31.74" E	22.816	1	1.316.071.8890	611.219.9891

SUPERFICIE = 219.973 m2 = 312.01 Vrs2

MORGAN
Servicios Topograficos
Ing. Bosco Javier Morgan
Lic. Catastral: BMM100426
Cel: 8583 7568 T

Objeto Lev: Venta Total	Número Catastral: 63112820069614		FIRMA:
Enajenante: Eddy Antonio Rodriquez Manzanares Cédula: 001-160374-0064P	Ubicacion: Lotificación Vistas del Sur, Lote 181-I Municipio de Granada, Departamento de Granada		Ejecuta: Ing.Bosco Javier Morgan Lic. Catastral: BMM100426 Cel: 8583-7568 Email: ingmorgan@gmail.com SERVICIOS TOPOGRAFICOS
Adquiriente: Pablo Humberto Cisne Oporta Ced: 201-251088-0004R	Área: 219.973 m² = 312.01 Vrs²	Escala: 1 / 500	Fecha: 21 de Noviembre del 2025

Objeto Plano	Área (m²)	No. Lote	
TRASPASO TOTAL	219.97		W8BZ3JV
Cudoc	Documento		
0040663	63112820069614		
Transacion	Parcela Objeto		
T-46H410-001			
Fecha Aprobación: 29/11/2025			Fecha Vencimiento: 29/11/2026
No. Licencia: BMM100426			