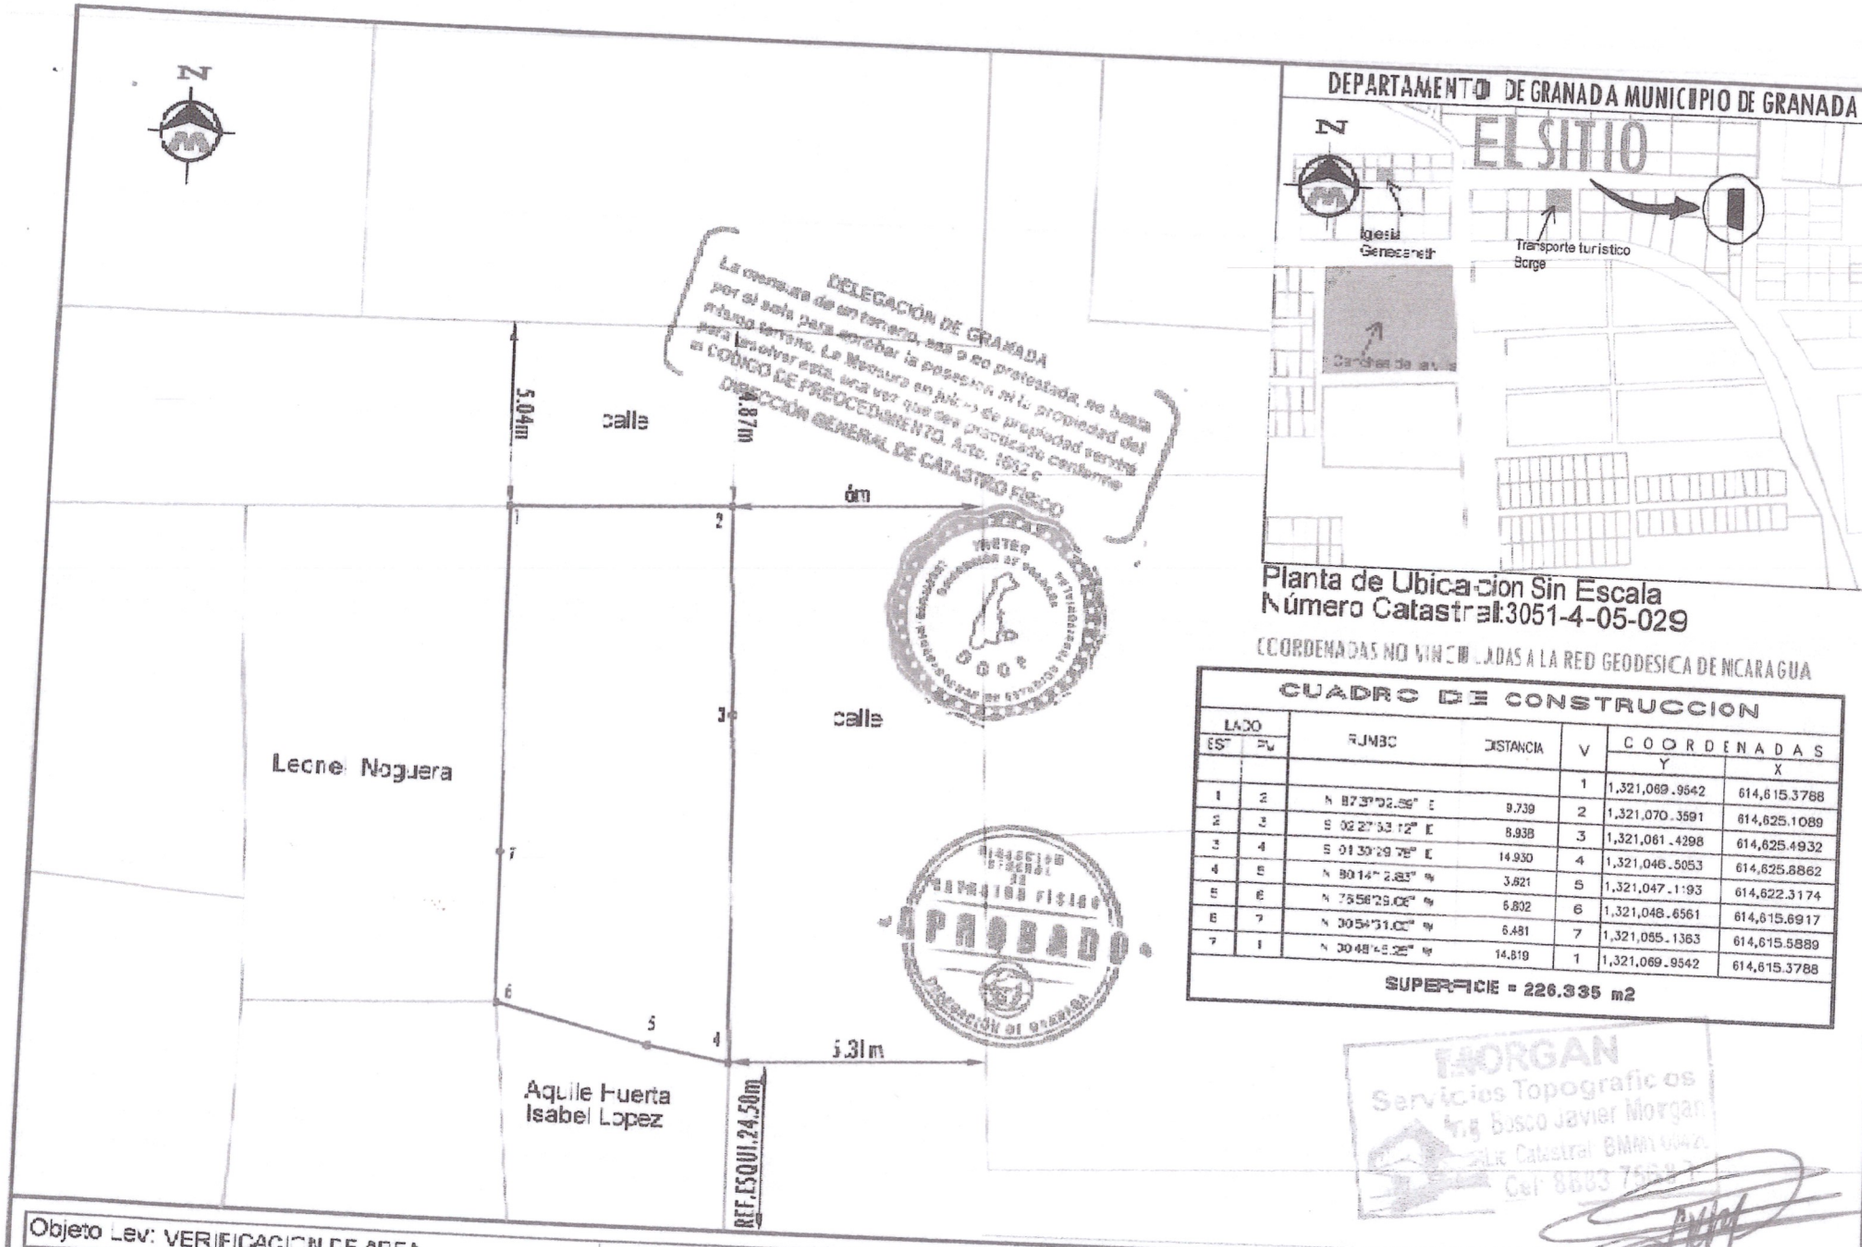

Planta de Ubicacion Sin Escala
Número Catastral:3051-4-05-029

COORDENADAS NO VINCULADAS A LA RED GEODESICA DE NICARAGUA

CUADRO DE CONSTRUCCION

LADO EST	LADO PV	RUMBO	DISTANCIA	V	COORDENADAS Y	COORDENADAS X
				1	1,321,069.9542	614,615.3788
1	2	N 87°39'02.86" E	9.739	2	1,321,070.3591	614,625.1089
2	3	S 02°27'53.12" E	8.938	3	1,321,061.4298	614,625.4932
3	4	S 01°30'29.78" E	14.930	4	1,321,046.5053	614,625.8862
4	5	N 80°14'2.83" W	3.821	5	1,321,047.1193	614,622.3174
5	6	N 75°56'29.06" W	5.802	6	1,321,048.6561	614,615.6917
6	7	N 30°54'31.02" W	5.481	7	1,321,055.1363	614,615.5889
7	1	N 30°48'45.25" W	14.819	1	1,321,069.9542	614,615.3788

SUPERFICIE = 226.335 m2

MORGAN
Servicios Topograficos
Ing. Bosco Javier Morgan
Lic. Catastral BMM100426
Cel: 8683 7568

Objeto Lev: VERIFICACION DE AREA	Número Catastral 3051-4-05-029	Fecha: 5 de Noviembre del 2025	FIRMA:
Propietario: Josefa Guadalupe Montiel Tercero Cédula: 2C1-091263-0003E	Ubicación: Vl.Sandino Grupo Casa N°814 Municipio de Granada. Dpto Granada	Ejecuta: Ing.Bosco Javier Morgan Lic. Catastral: BMM100426 Cel: 8683 7568 Email: ingmorgan73@gmail.com Servicios Topograficos	
	Area:226.335 m2 = 321.04vrs2	Escala: 1 / 300	

Transacción	Cudoc	Objeto Plano	Área (m²)	No. Lote
T-46GEON-001	0040213	VERIFICACIÓN	226.33	
Parcela Objeto	6312416005241 4		Documento	W8BZ12J
No. Licencia: BMM100426	Fecha Aprobación: 24/11/2025		Fecha Vencimiento: 24/11/2026	