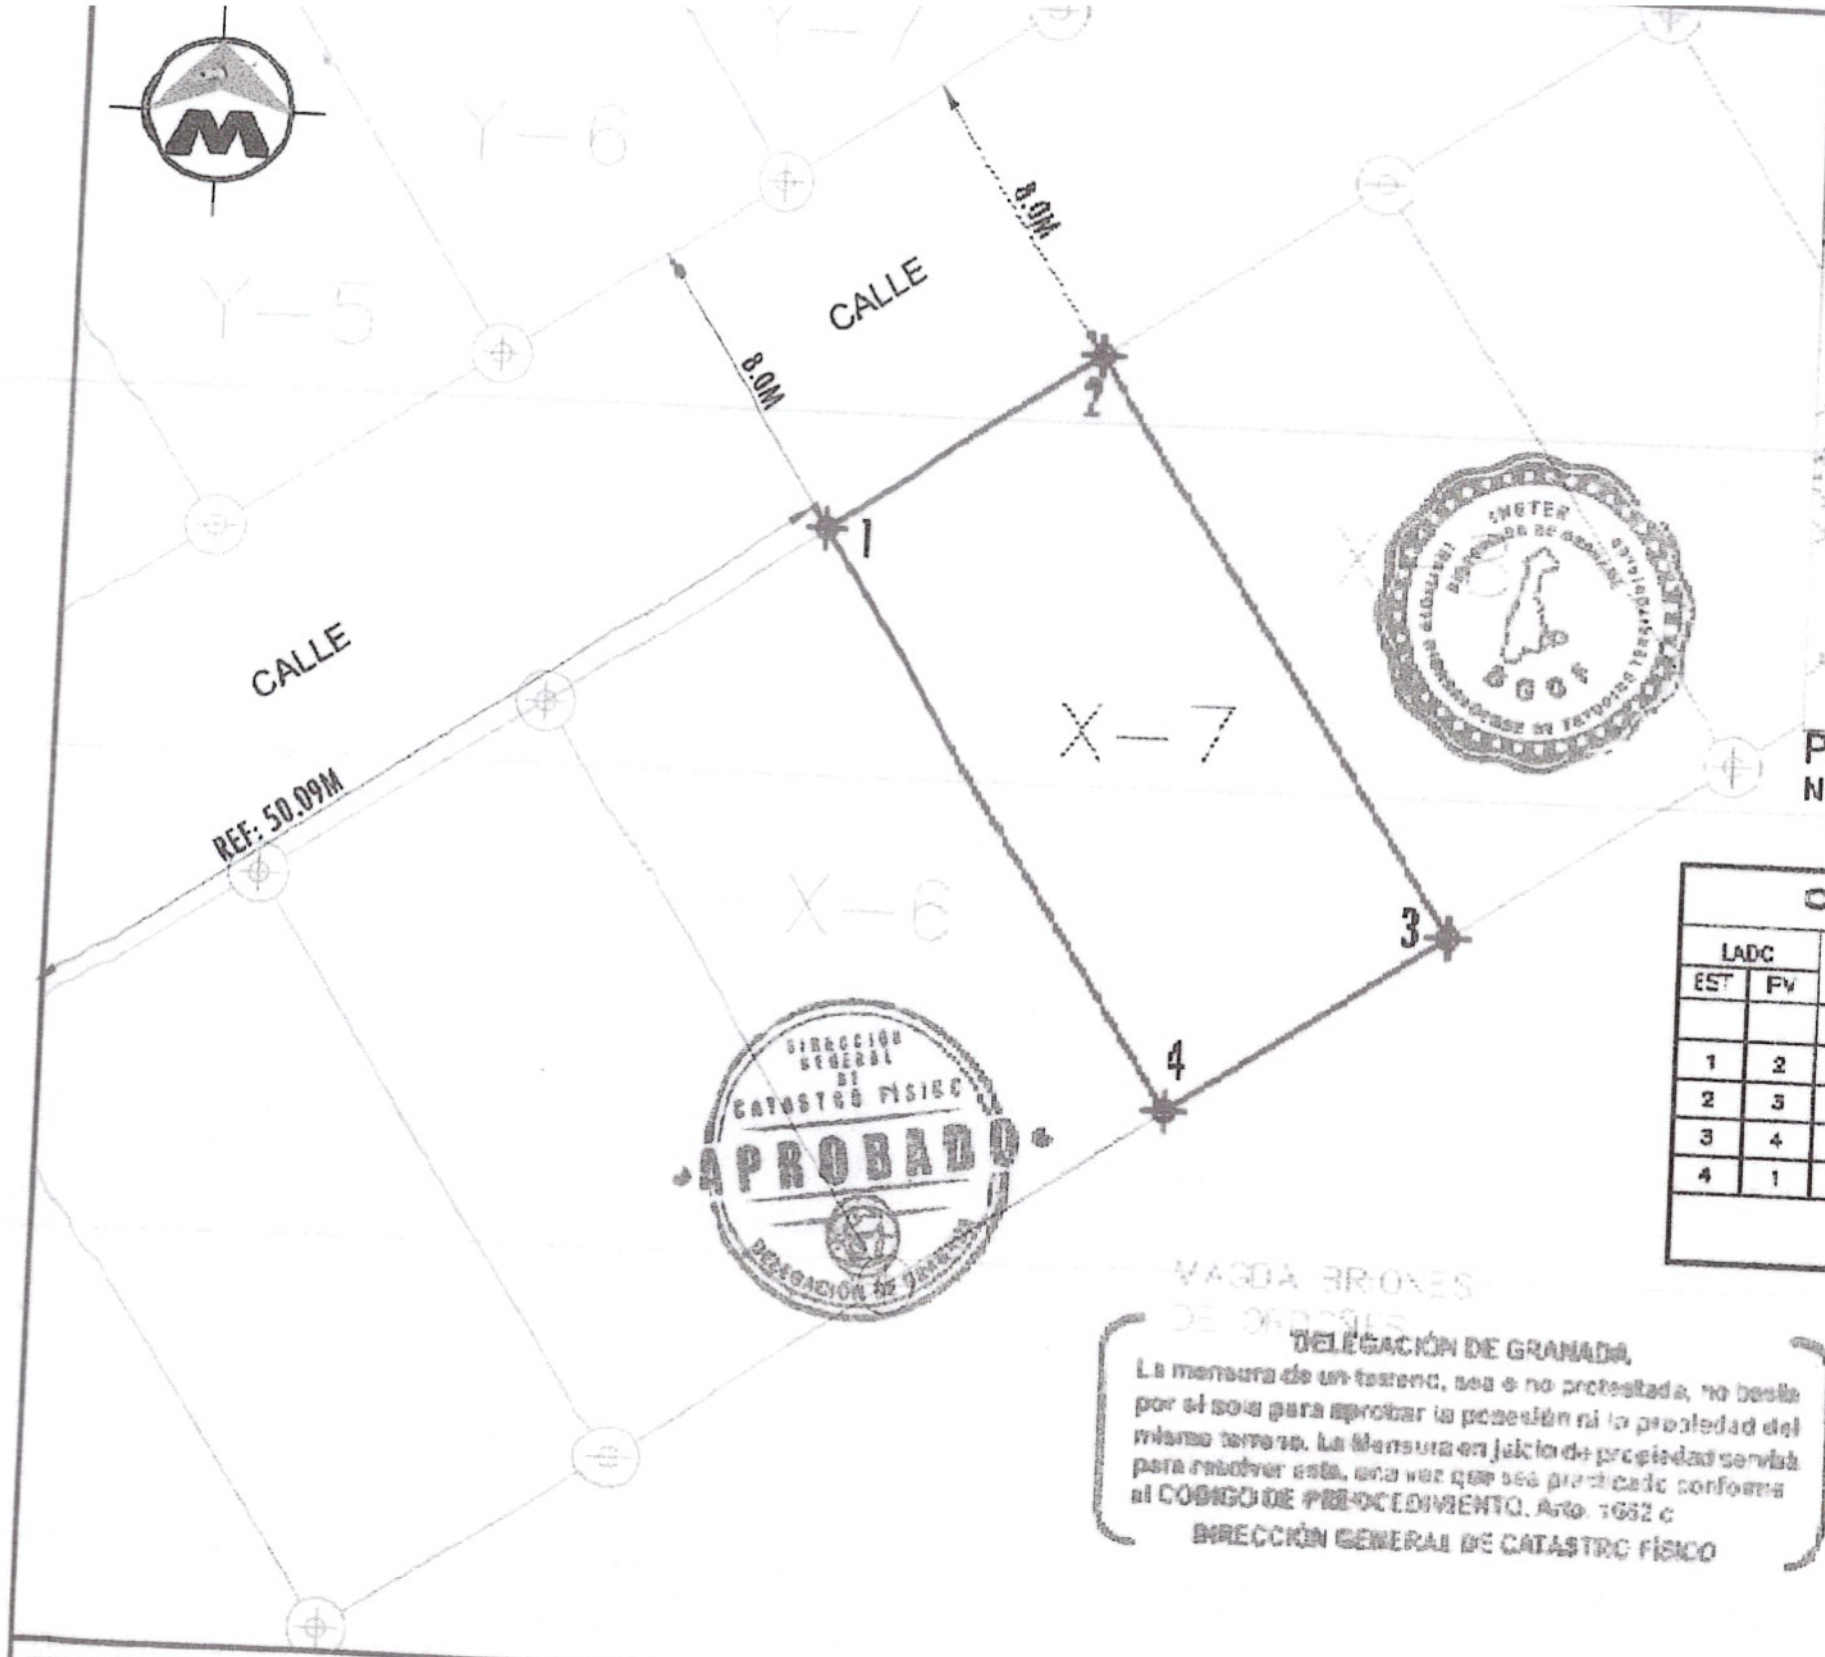

DIRECCIÓN GENERAL DE CATASTRO FÍSICO
APROBADO
DELEGACIÓN DE GRANADA

VAGDA BRONES DE ORDÓÑEZ

DELEGACIÓN DE GRANADA.
La mensura de un terreno, sea o no protestada, no basta por sí sola para aprobar la posesión ni la propiedad del mismo terreno. La Mensura en juicio de propiedad servirá para resolver esta, una vez que sea practicada conforme al CODIGO DE PROCEDIMIENTO. Arto. 1662 c
DIRECCIÓN GENERAL DE CATASTRO FÍSICO

DEPARTAMENTO DE GRANADA. MUNICIPIO DE GRANADA

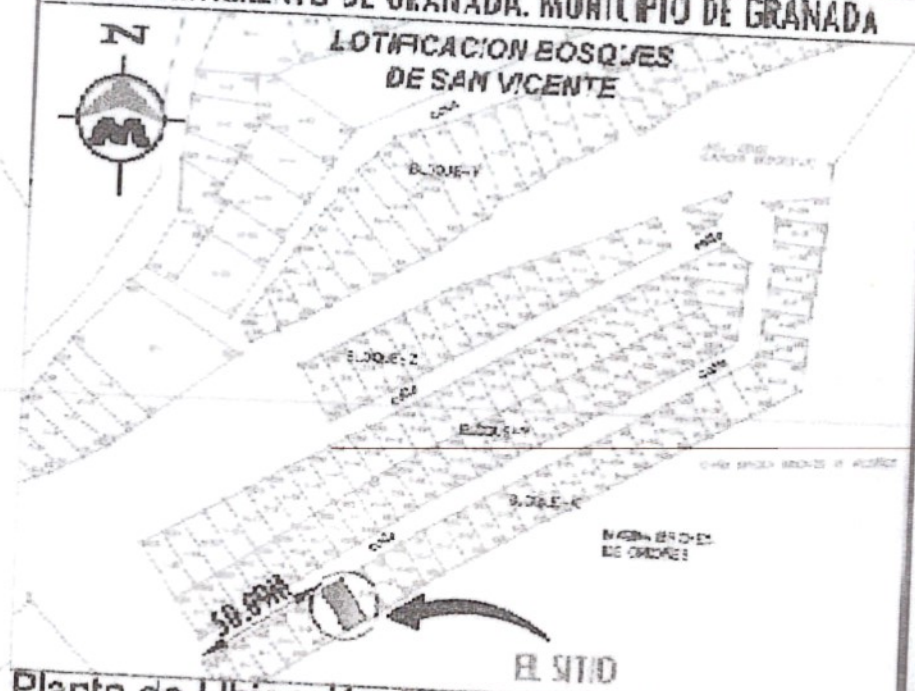

Planta de Ubicación Sin Escala
Número Catastral 3051-4-09-000- (03900) N/C
COORDENADAS NO VINCULADAS A LA RED GEODÉSICA DE NICARAGUA

CUADRO DE CONSTRUCCION

LADO EST	LADO PV	RUMBO	DISTANCIA	V	COORDENADAS Y	COORDENADAS X
				1	1'317,121.4038	512,786.7492
1	2	N 56°23'13.61" E	8.349	2	1'317,121.3324	512,793.7019
2	3	S 33°39'46.87" E	14.898	3	1'317,111.949*	512,803.0595
3	4	S 56°23'12.89" W	8.349	4	1'317,104.329	512,796.1067
4	1	N 33°39'47.01" W	14.898	1	1'317,121.4038	512,786.7492

SUPERFICIE = 141076 m2

Objeto Lev: Venta Parcial (Desmembración)	Número Catastral 3051-4-09-000- (03900) N/C	FIRMA:	
Enajenante: Maria Auxilio Marenco Gutierrez Cédula: 201-260948-0001B	Ubicación Lotificación Bosques San Vicente lote #7 Bloque X Municipio de Granada, Departamento de Granada.	Ejecutor: Ing. Bosco Javier Morgan Lic. Catastral: BMM100426 Cel: 8863-7566 Email: ingmorgan73@gmail.com SERVICIOS TOPOGRAFICOS	
Adquirientes: Darwing de Jesus Mora Romero Cédula: 201-070291-0008N	Area: 141.076 m² = 210.1043 Vrs² Escala 1/250	Fecha: 29 de Octubre de 2025	

MORGAN
Servicios Topograficos
Ing Bosco Javier Morgan
Lic. Catastral BMM100426
Cel 8863 7566 T

Objeto plano	Área (m²)	No. Lote	
DESMEMBRACIÓN	141.08		
Cudoc	Documento	WOBYSOH	
0039908	63112771804719		
Transacción	Fecha Vencimiento: 4/11/2025		
T-46g4X6-001	Fecha Aprobacion: 4/11/2025		
Parcela Objeto			
No. Licencia: BMM100426			