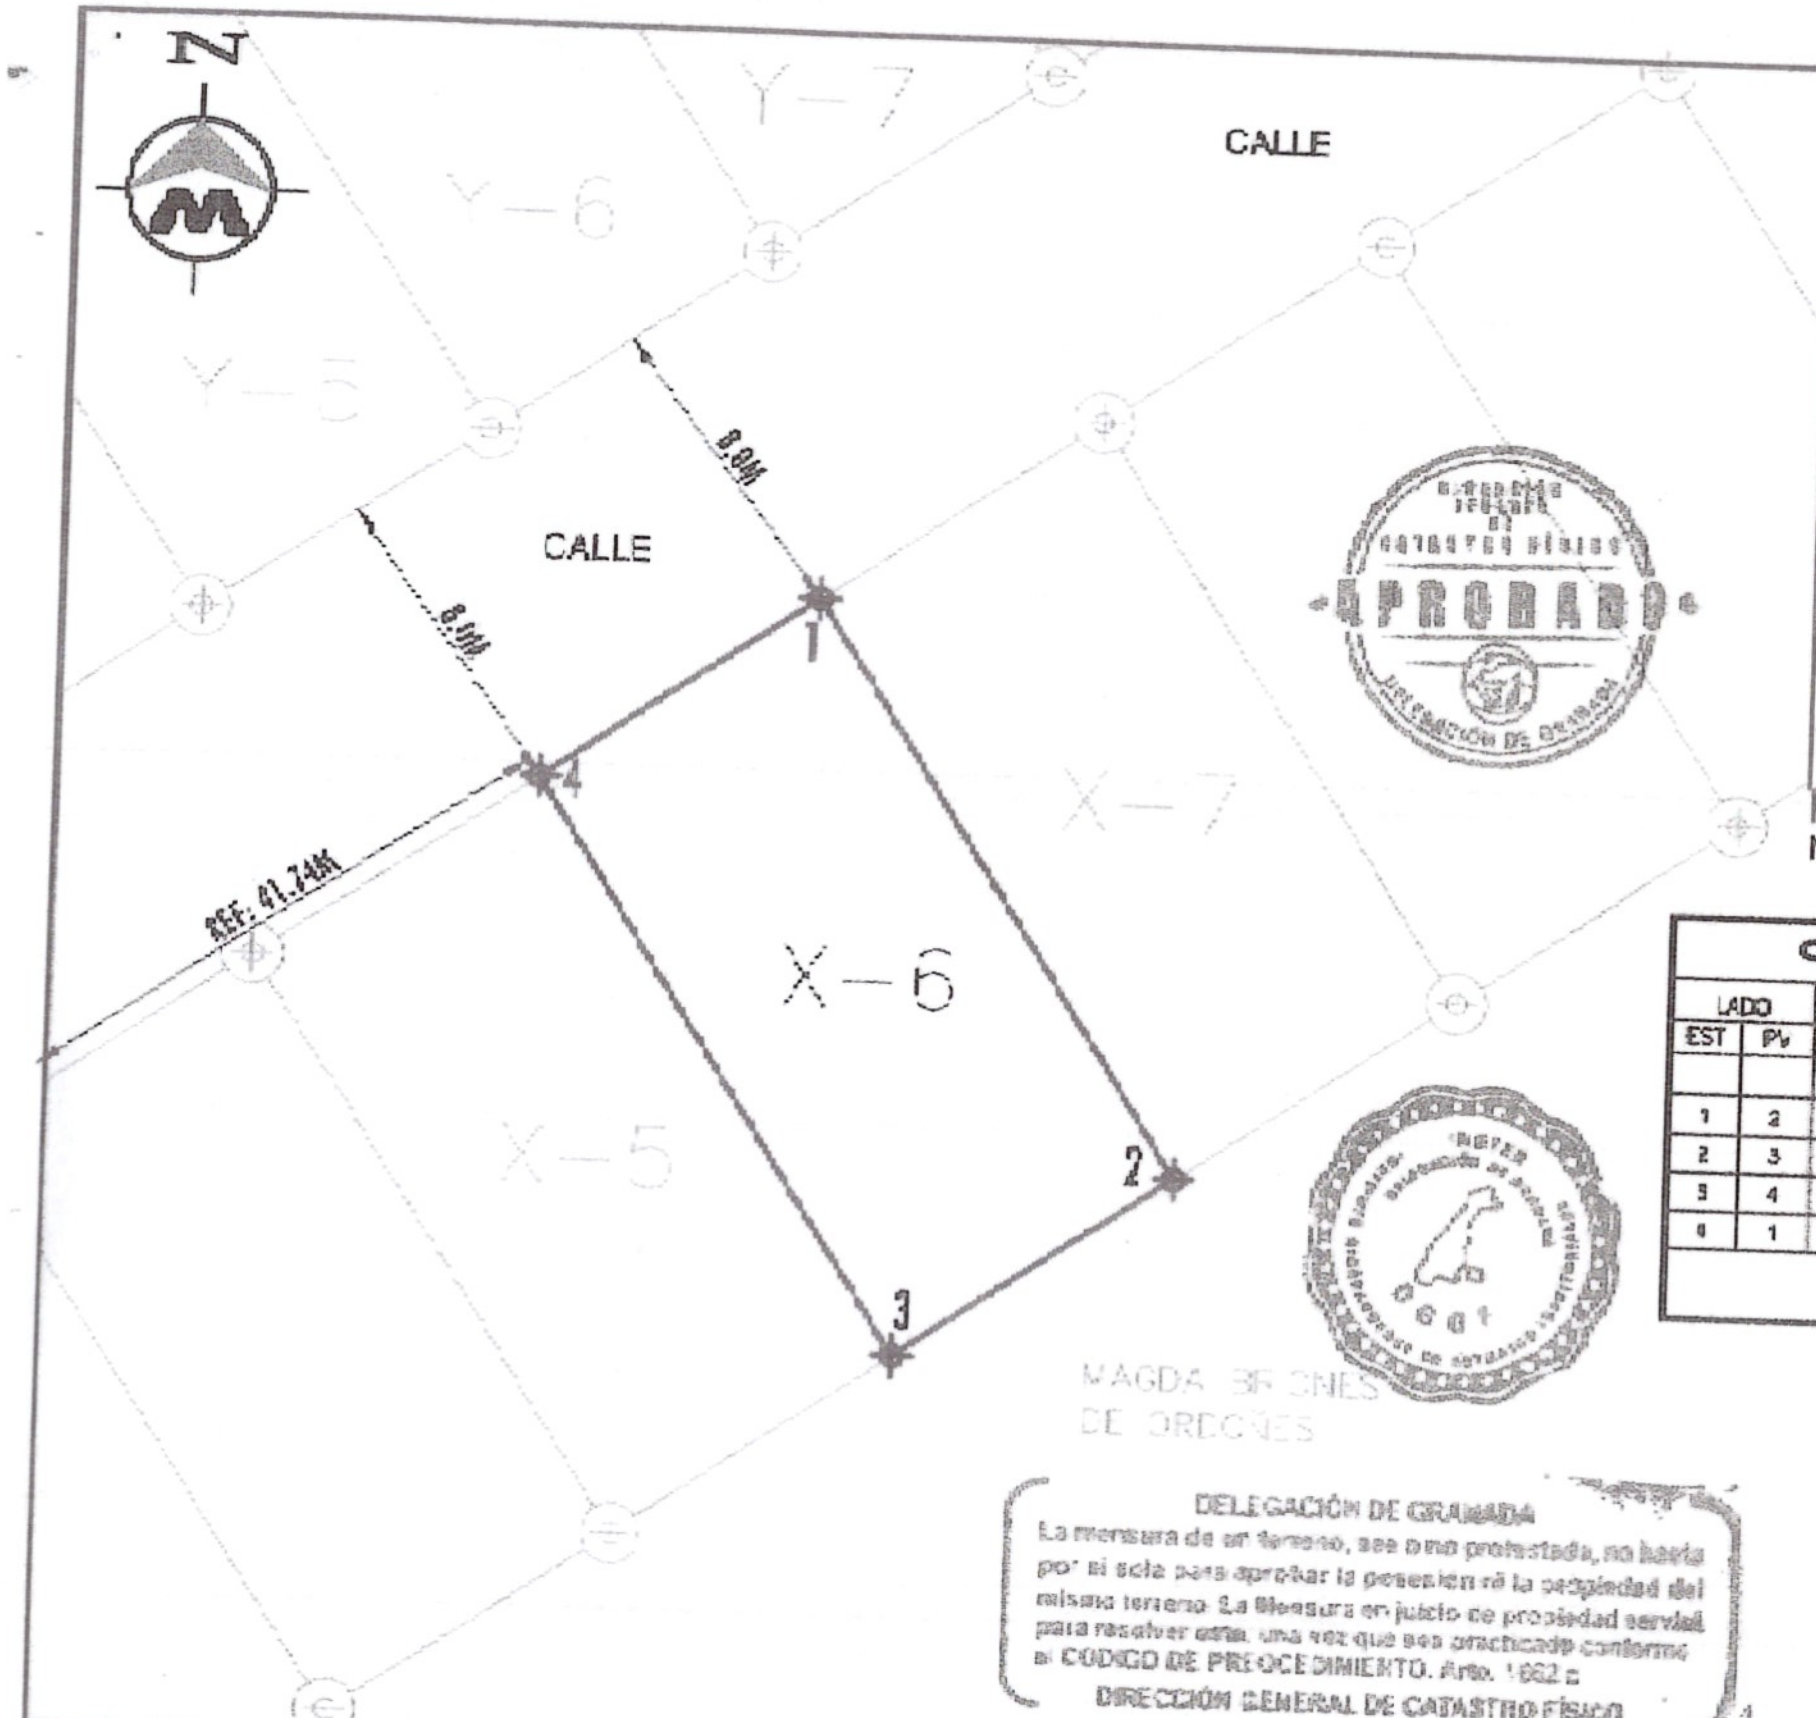

DEPARTAMENTO DE GRANADA. MUNICIPIO DE GRANADA

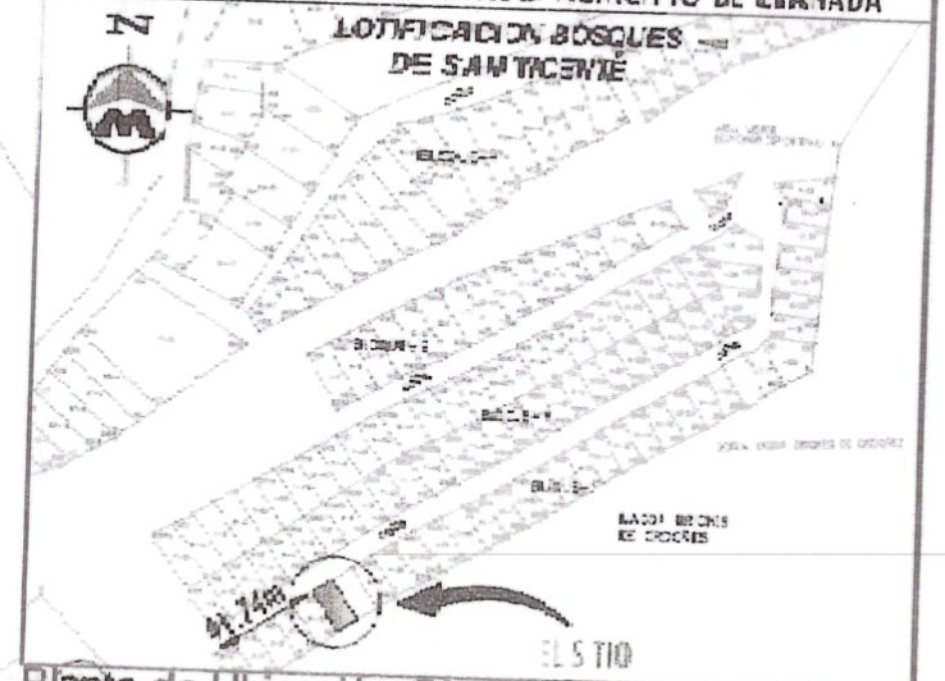

Planta de Ubicación Sin Escala

Número Catastral: 3051-4-09-300- (03900) N/C

(COORDENADAS NO VINCULADAS A LA RED GEODESICA DE NICARAGUA

CUADRO DE CONSTRUCCION

LADO EST	LADO PV	RUMBO	DISTANCIA	-	COORDENADAS Y	COORDENADAS X
					1,317,122.4008	12,786.7492
1	2	S 33°19'47.01" E	16.898		1,317,108.3281	12,796.1037
2	3	S 56°13'13.48" W	8.349		1,317,103.7065	12,789.1510
3	4	N 33°19'48.94" W	16.898		1,317,117.7792	12,779.7966
4	1	N 56°13'13.48" E	8.349		1,317,122.4008	12,786.7492

SUPERFICIE = 140.87 m2

DELEGACIÓN DE GRANADA
La mensura de un terreno, sea o no protestada, no hacía por sí sola para aprobar la posesión ni la propiedad del mismo terreno. La Mensura en juicio de propiedad servirá para resolver esta, una vez que sea anotada conforme al CODIGO DE PROCEDIMIENTO. Arts. 1662 c
DIRECCIÓN GENERAL DE CATASTRO FÍSICO

MORGAN
Servicios Topograficos
Ing. Bosco Javier Morgan
Lic. Catastral BMM100426
Cel: 8843 7568 T

Objeto Lev: Venta Parcial (Desmembración)	Número Catastral: 3051-4-09-300- (03900) N/C	FIRMA:	
Enajenante: Maria Auxilio Marenco Gutierrez Cedula: 281-260948-0001B	Ubicación: Lotificación Bosques San Vicente cte # 6 Bloque X. Municipio de Granada, Departamento de Granada	Ejecutor: Ing. Bosco Javier Morgan Lic. Catastral: BMM100426 Cel: 8843 7568 Email: ingmorgan2@hotmail.com SERVICIOS TOPOGRAFICOS	
Adquirientes: Darwing de Jesus Mora Romero Cédula: 281-070291-0008N	Area: 140.87 m² = 199.812 Vrs²	Escala: 1 / 250	Fecha: 29 de Octubre del 2025

Transacción	Cudoc	Objeto Plano	Area (m²)	No. Lote
T-46G4WL-001	0039927	DESMEMBRACIÓN	140.87	
Parcela Objeto			Documento	
	6311277170732 6		W8BYT7W	
No. Licencia: BMM100426	Fecha Aprobación: 5/11/2025		Fecha Vencimiento: 5/11/2026	