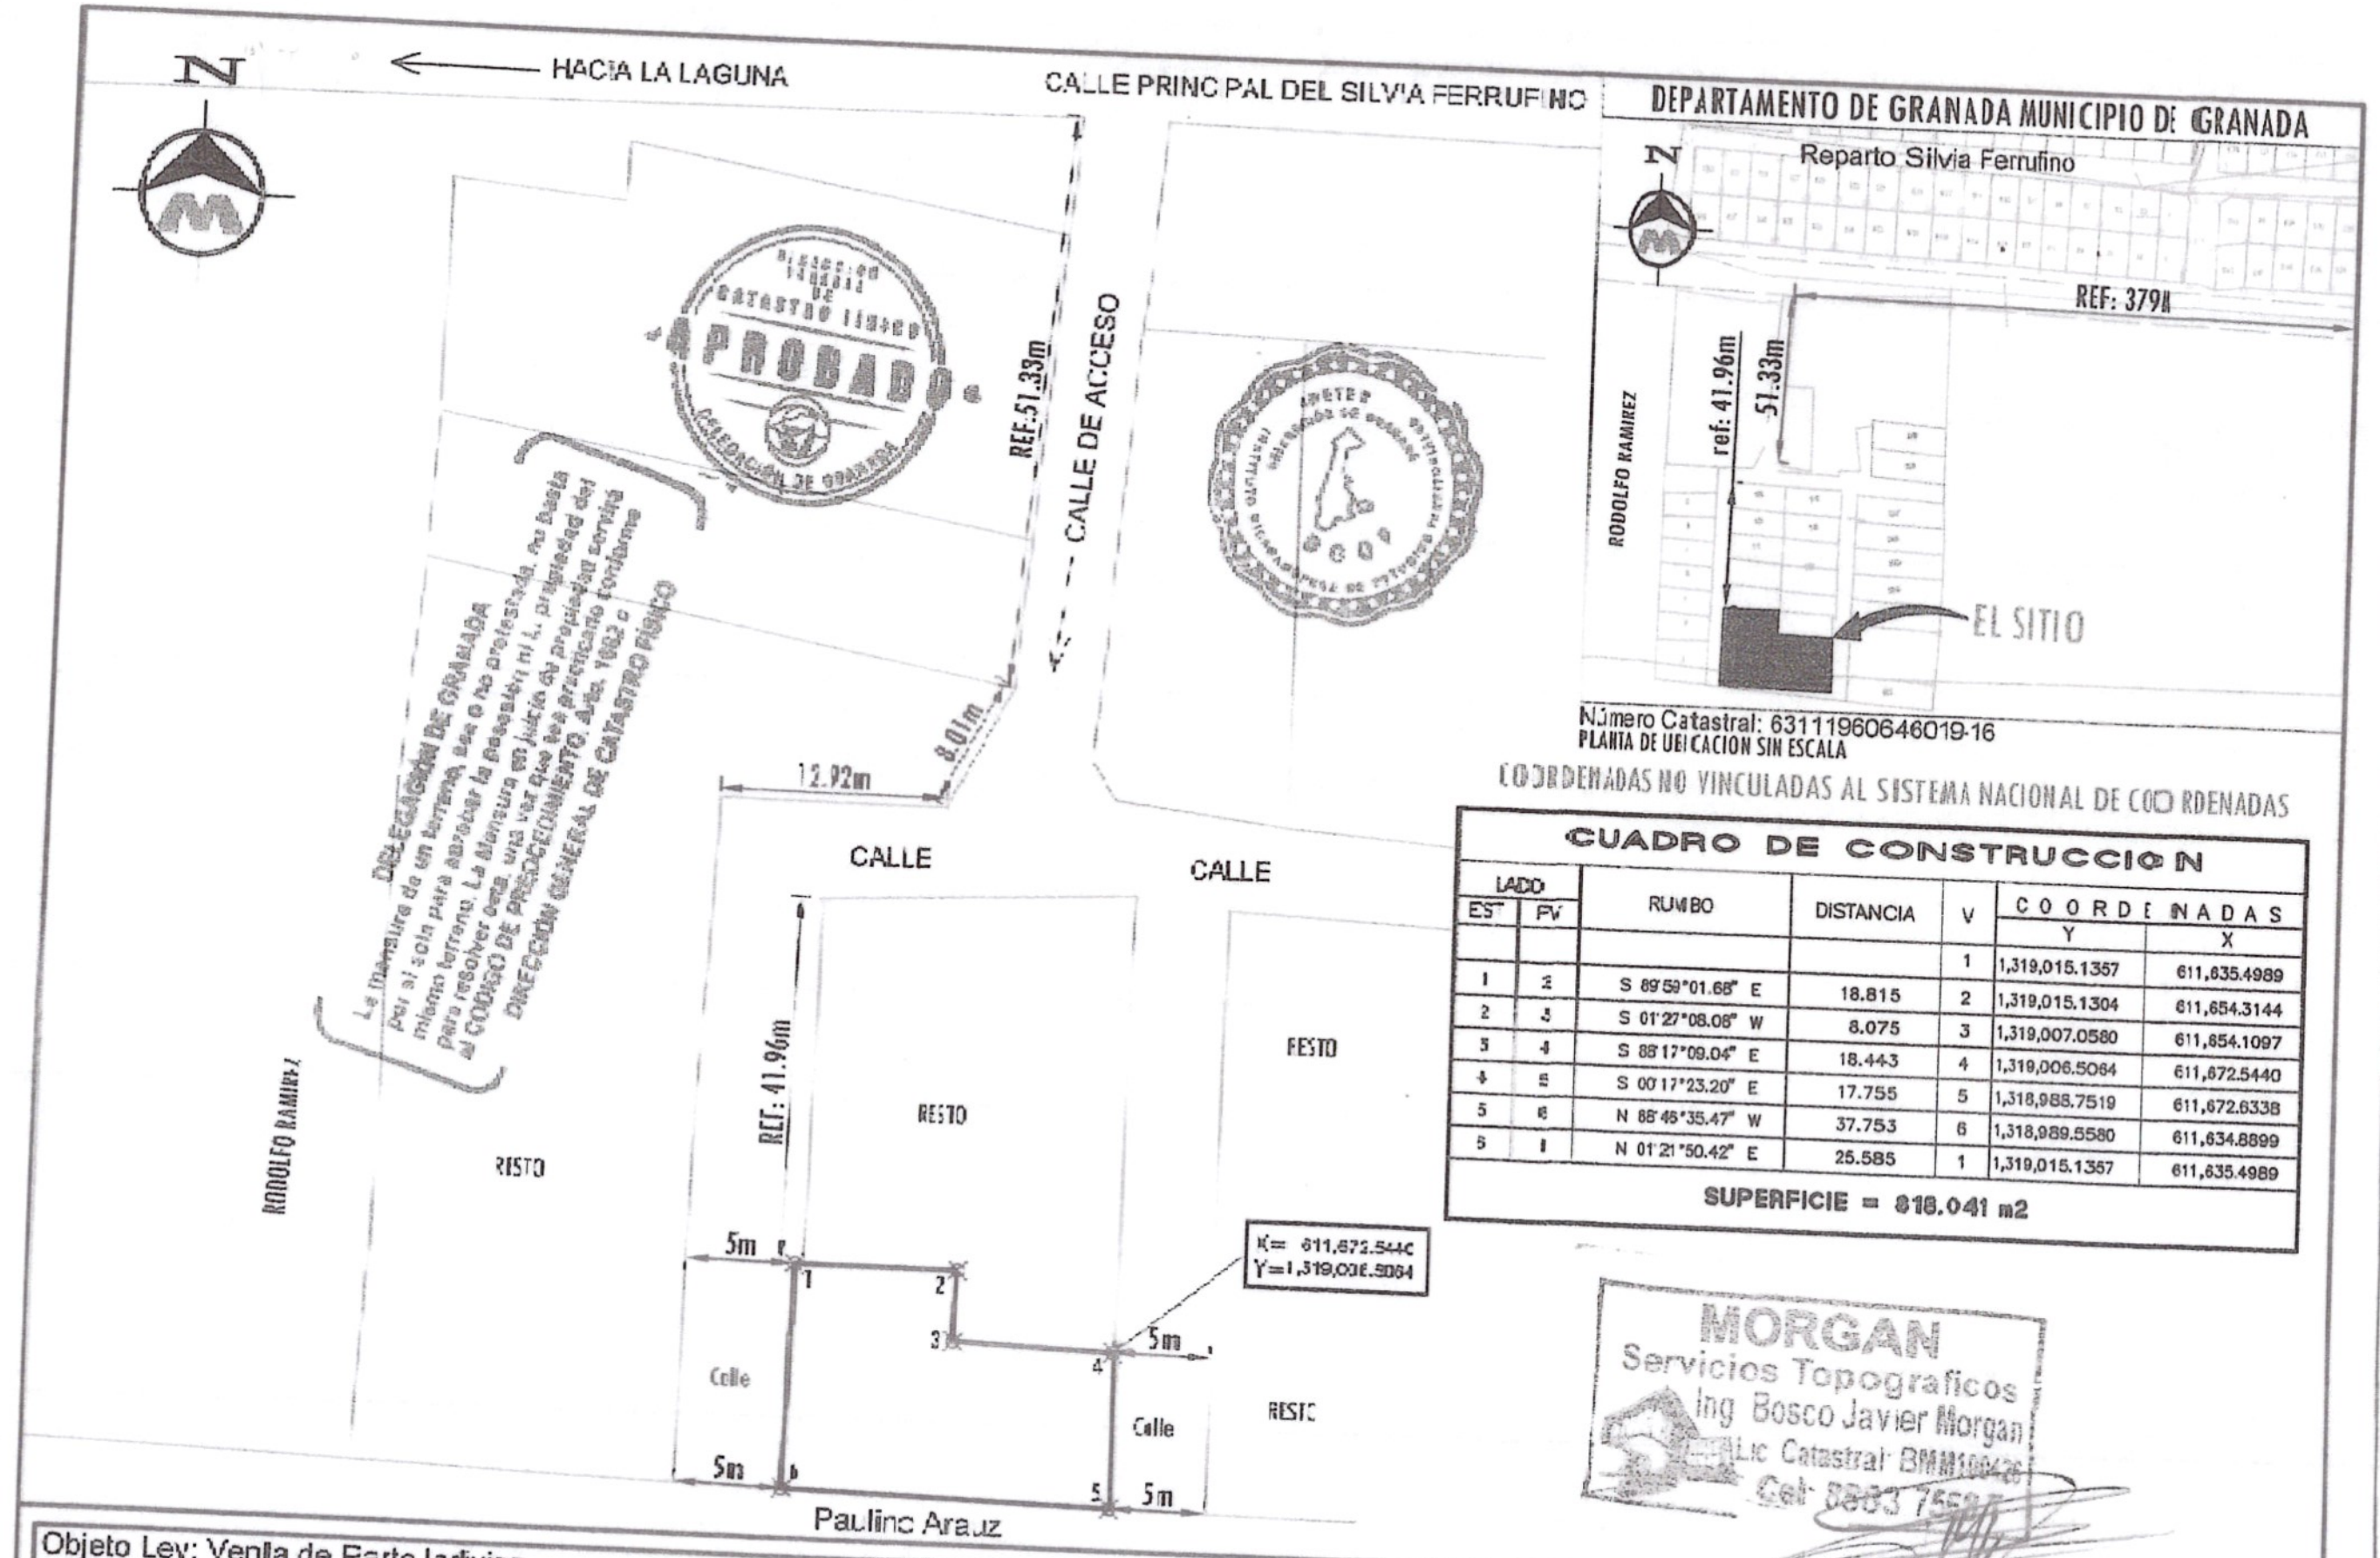

CUADRO DE CONSTRUCCION

LADO EST	LADO PV	RUMBO	DISTANCIA	V	COORDENADAS Y	COORDENADAS X
				1	1,319,015.1357	611,635.4989
1	2	S 89°59'01.68" E	18.815	2	1,319,015.1304	611,654.3144
2	3	S 01°27'08.06" W	8.075	3	1,319,007.0580	611,654.1097
3	4	S 88°17'09.04" E	18.443	4	1,319,006.5064	611,672.5440
4	5	S 00°17'23.20" E	17.755	5	1,318,988.7519	611,672.6338
5	6	N 88°46'35.47" W	37.753	6	1,318,989.5580	611,634.8899
6	1	N 01°21'50.42" E	25.585	1	1,319,015.1357	611,635.4989

SUPERFICIE = 818.041 m2

Objeto Lev: Venta de Parte Indivisa	Numero Catastral: 3051-4-C5-000-08620		FIRMA:
Enajenante: Augusto Cesar Marenco Balladares Cédula: 201-151237-0005L	Ubicación: De la primera entrada al Reparto Silvia Ferrufino 379m W. 51.33 m al S 8.01 m S-W y 12.92m Oeste 41.96m S. Municipio de Granada. Departamento de Granada.		Ejecuta: Ing.Bosco Javier Morgan Lic. Catastral: BMM100426 Cel: 8883-7568 Email: ingmorgan73@gmail.com SERVICIOS TOPOGRAFICOS
Adquiriente: Ester Maria Ruiz Mendoza Cédula: 001-101162-0005E	Área: 818.041 m²= 1,160.32vrs2	Escala: 1/1000	Fecha: 29 de Octubre del 2025

Transacción	Cudoc	Objeto Plano	Área (m²)
T-46GENH-001	0040210	DESMEMBRACIÓN	818.04
Parcela Objeto			
No. Licencia: BMM100426	Fecha Aprobación: 11/11/2025	Documento	No. Lote
		W8BYVID	
	Fecha Vencimiento: 11/11/20		