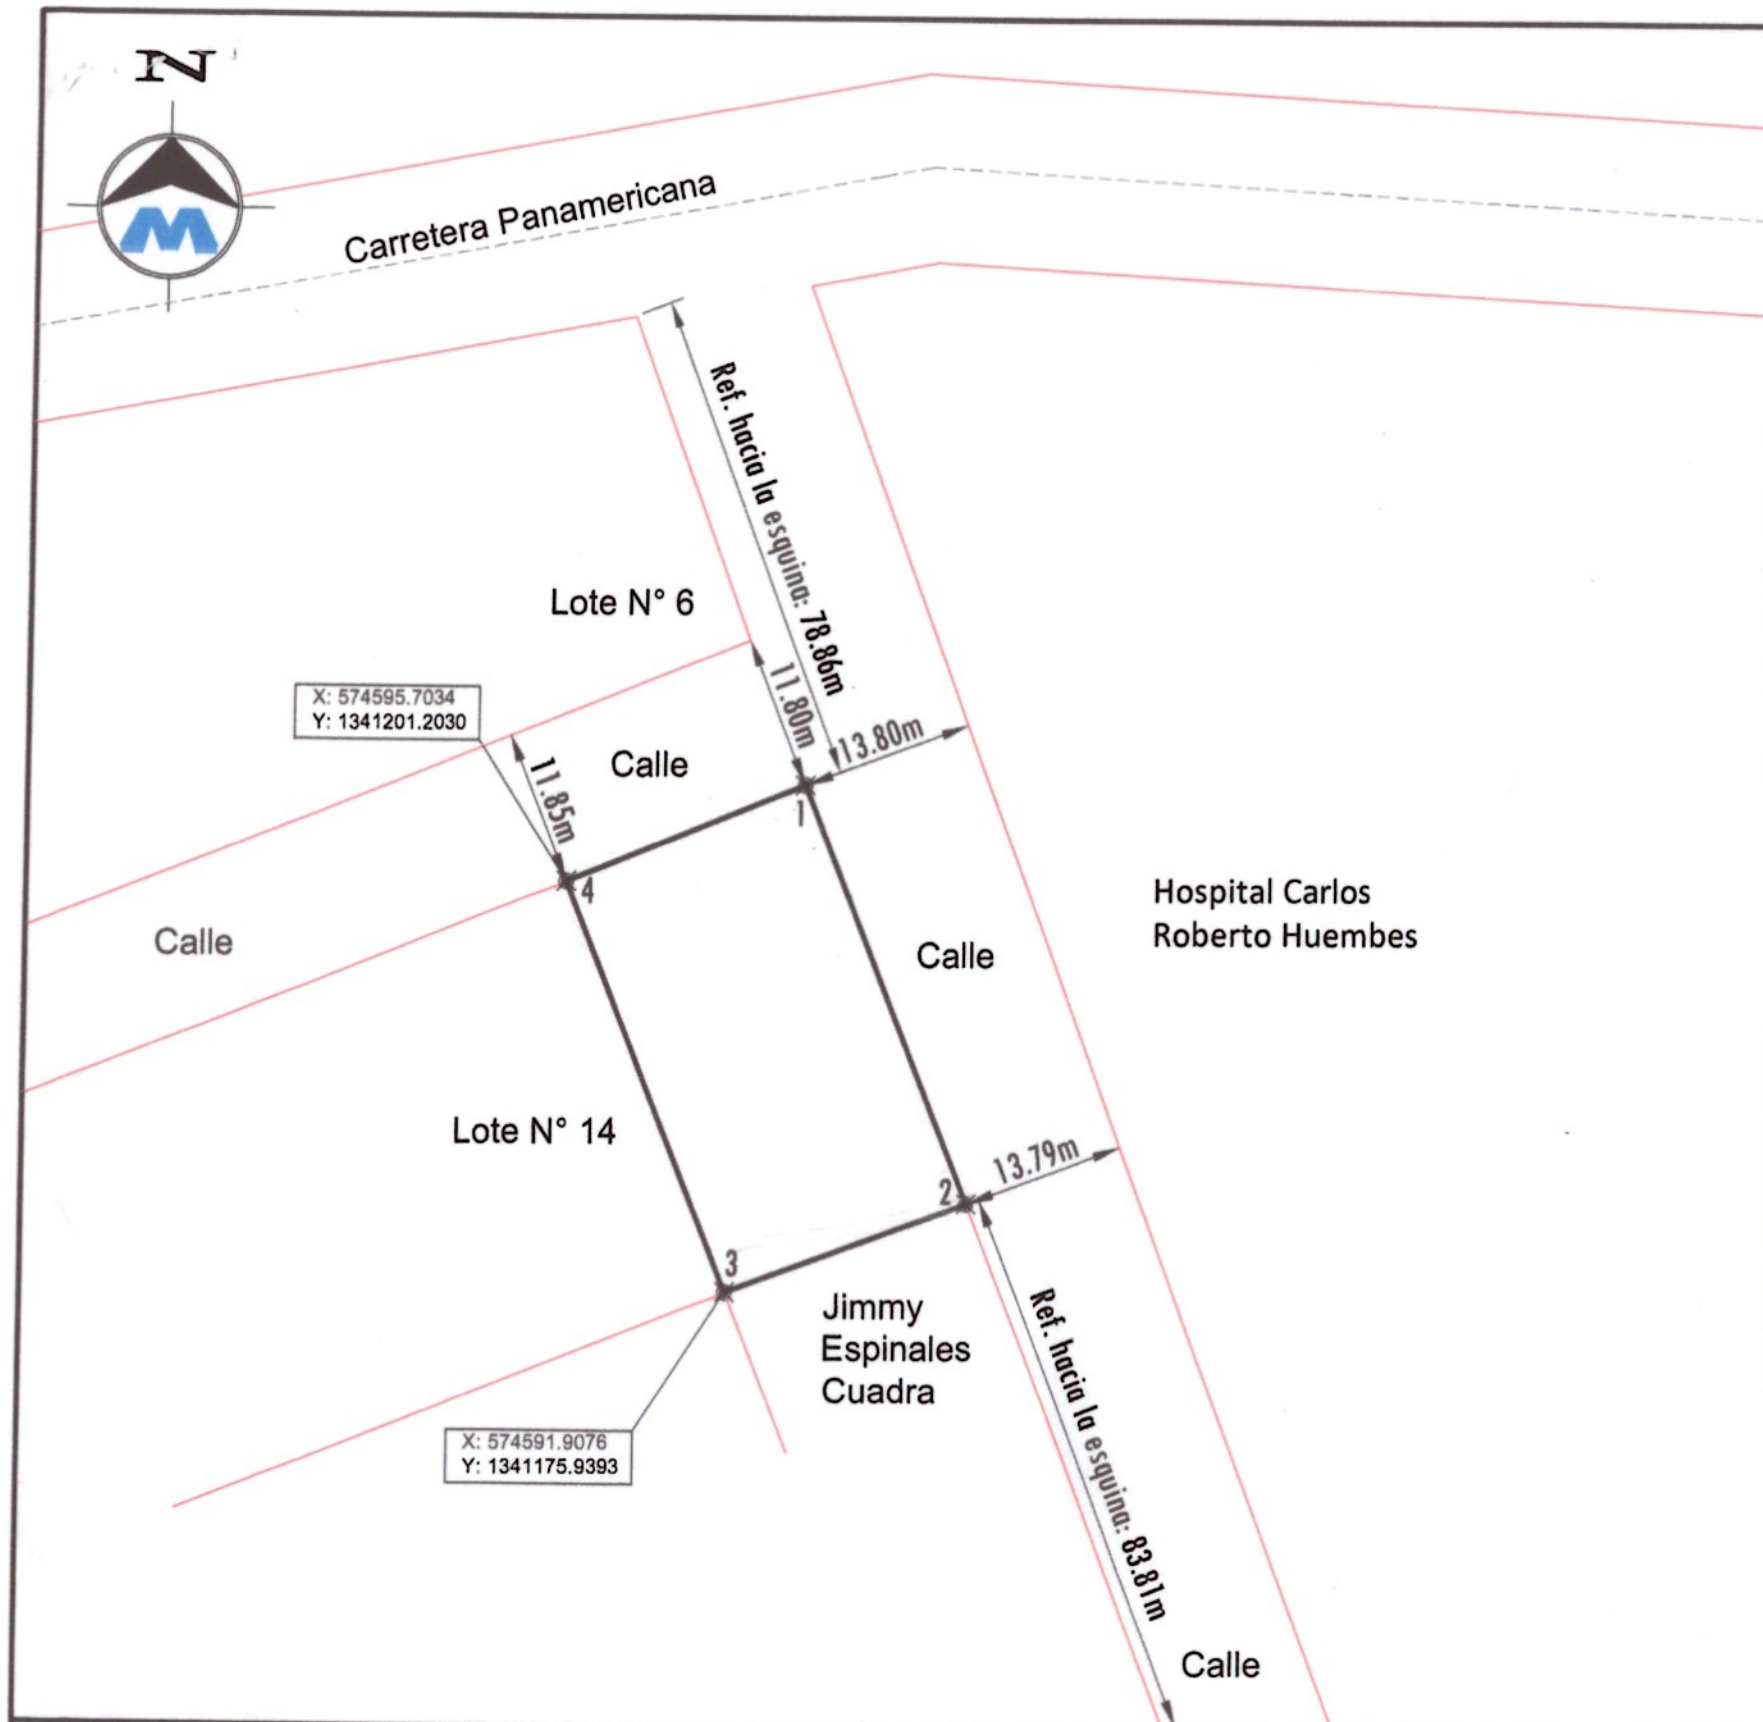

DEPARTAMENTO DE MANAGUA MUNICIPIO DE CIUDAD SANDINO

Planta de Ubicación Sin Escala
Número Catastral: 53744151992123

COORDENADAS NO VINCULADAS A LA RED GEODESICA DE NICARAGUA

CUADRO DE CONSTRUCCION

LADO EST	LADO PV	RUMBO	DISTANCIA	V	COORDENADAS Y	COORDENADAS X
				1	1,341,201.2030	574,595.7034
1	2	S 21°43'02.81" E	22.370	2	1,341,180.4211	574,603.9809
2	3	S 69°38'03.75" W	12.878	3	1,341,175.9393	574,591.9076
3	4	N 21°50'37.63" W	21.965	4	1,341,196.3270	574,583.7350
4	1	N 67°50'02.09" E	12.924	1	1,341,201.2030	574,595.7034

SUPERFICIE = 285.931 m2 = 405.57 Vrs2

Objeto Lev: Compraventa total	Número Catastral: 53744151992123	FIRMA:	SELLO
Enajenante: Chung Ming Lee Ced. de Residencia: 280520140270	Ubicación: Residencial Las Piedrecitas, costado Oeste del Hospital Carlos Roberto Huembes. Municipio de Ciudad Sandino, Departamento de Managua.	Ejecuta: Ing. Bosco Javier Morgan Mercado Lic. Catastral: BMM100426 Cel: 8883-7568 Email: ingmorgan73@gmail.com SERVICIOS TOPOGRAFICOS	
Adquiriente: Fernando Josué Davila Espinoza Cédula: 001-131102-1038K	Área: 285.931 m² = 405.57 Vrs² — Escala: 1 /500	Fecha: 22 de Octubre del 2025	

ESPACIO PARA ESQUELA

Objeto Lev: Compraventa total
Número Catastral: 53744151992123

COORDENADAS NO VINCULADAS A LA RED GEODESICA DE NICARAGUA

CUADRO DE CONSTRUCCION

LADO		RUMBO	DISTANCIA	V	COORDENADAS	
EST	PV				Y	X
				1	1,341,201.2030	574,595.7034
1	2	S 21°43'02.81" E	22.370	2	1,341,180.4211	574,603.9809
2	3	S 69°38'03.75" W	12.878	3	1,341,175.9393	574,591.9076
3	4	N 21°50'37.63" W	21.965	4	1,341,196.3270	574,583.7350
4	1	N 67°50'02.09" E	12.924	1	1,341,201.2030	574,595.7034

SUPERFICIE = 285.931 m2 = 405.57 Vrs2

Ejecuta: Ing. Bosco Javier Morgan
Lic. Catastral: BMM100426
Cel: 8883-7568 Email: ingmorgan73@gmail.com
SERVICIOS TOPOGRAFICOS