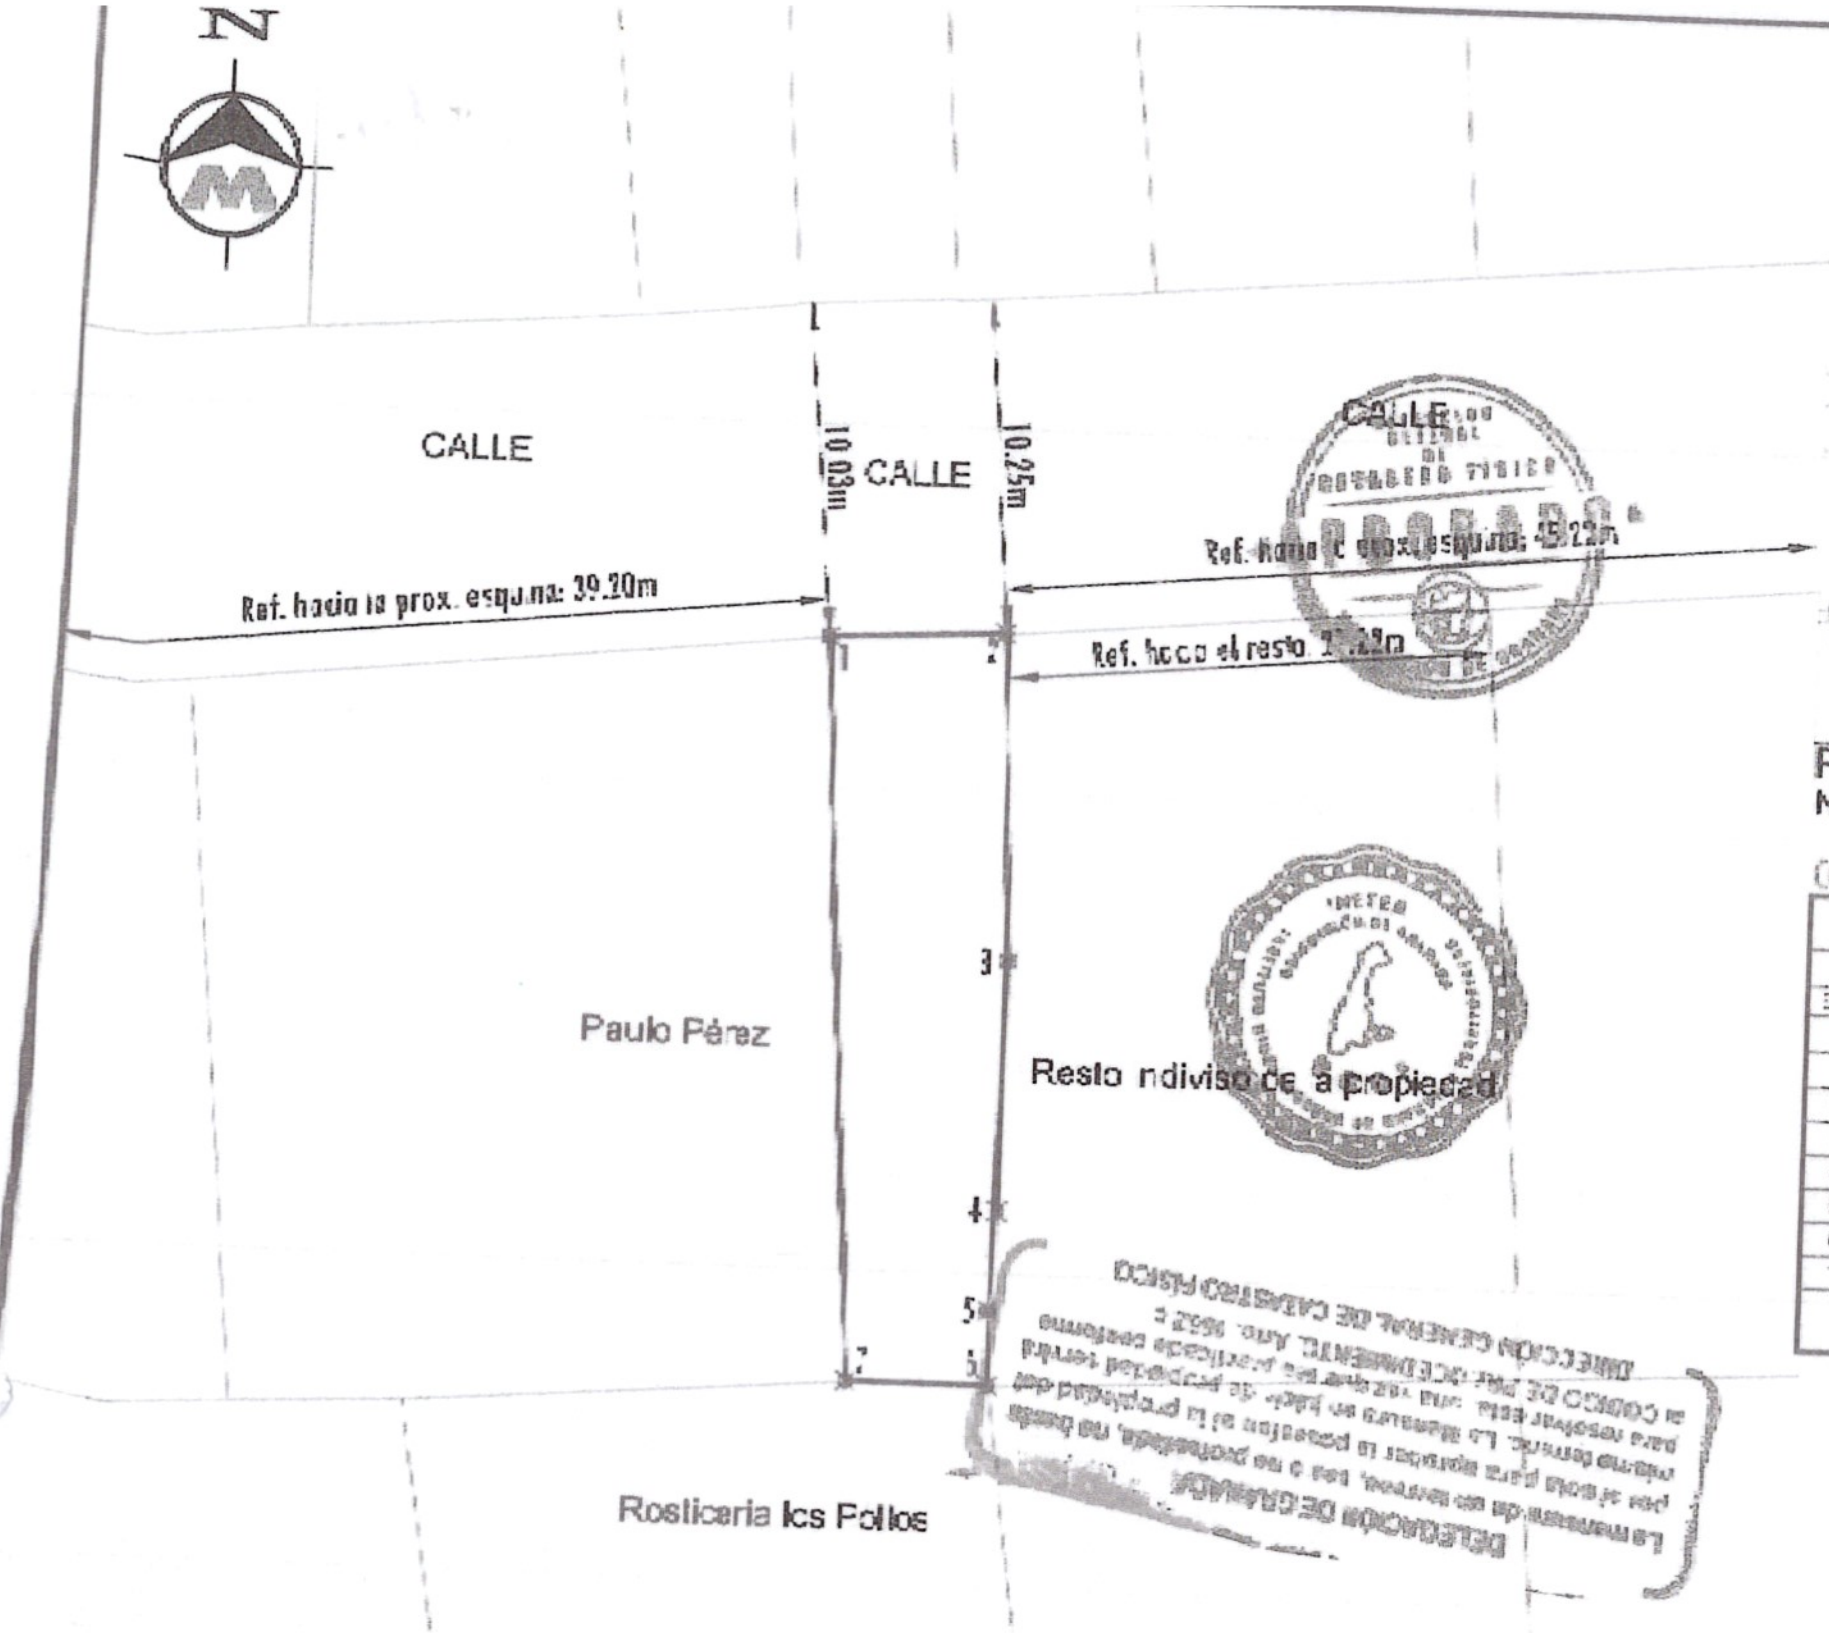

DEPARTAMENTO DE GRANADA MUNICIPIO DE NANDAIME

Planta de Ubicación Sin Escala
Numero Catastral: 2951-2-08-082-14500

COORDENADAS NO VINCULADAS A LA RED GEODESICA DE NICARAGUA

CUADRO DE CONSTRUCCION

LADO EST	PV	RUMBO	DISTANCIA	V	COORDENADAS Y	COORDENADAS X
					291,457.1800	642,890.3200
1	2	N 67° 18'48" E	5.400	2	291,457.4218	642,895.7135
2	3	S 02°11'16" E	5.774	3	291,451.9975	642,896.0657
3	4	S 01°-35'21" W	7.497	4	291,420.1589	642,895.4256
4	5	S 02°44'35.22" W	2.988	5	291,417.1171	642,895.7591
5	6	S 01°14'43.45" E	2.213	6	291,414.1652	642,895.8568
6	7	S 89°57'27.45" W	4.304	7	291,414.1668	642,891.5568
7	1	N 03° 32'38" W	20.215	1	291,437.1800	642,890.3200

SUPERFICIE = 111.141 m2 = 157.84 Vrs2

MORGAN
Servicios Topograficos
Ing Bosco Javier Morgan
Lic. Catastral: BMM100426
Cel. 8883-7566

Objeto Lev: Donación de una parte indivisa	Número Catastral: 2951-2-08-082-14500		FIRMA:	SELLO
Enajenante: Manuela Salvadora Barberena Guadamuz Ced: 202-231244-0000C	Ubicación: Bo Oscar Turcios, de la Alcaldía 2cal Norte 2c y 45.22 m al O. Municipio de Nandaime, Departamento de Granada.		Ejecutor: Ing. Bosco Javier Morgan Lic. Catastral: BMM100426 Cel. 8883-7566 Email: wmorgan73@gmail.com SERVICIOS TOPOGRAFICOS	
Adquiriente: Gady Alberto Solis Barberena Ced: 202-160595-0001Q	Área: 111.141 m²= 157.84 Vrs²	Factor de escala: 1.4184151	Escala: 1/300	Fecha: 29 de Octubre del 2025

Objeto Plano	Área (m²)	No. Lote	
DESMEMBRACIÓN	111.14		
62092994011810-2	Documento	W8BYS01	
Fecha Aprobación: 4/11/2025		Fecha Vencimiento: 4/11/2026	

Transacción	Catastro		
T-46241R-0111	0039911		
Parcela Objeto			
No. Licencia: BMM100426			