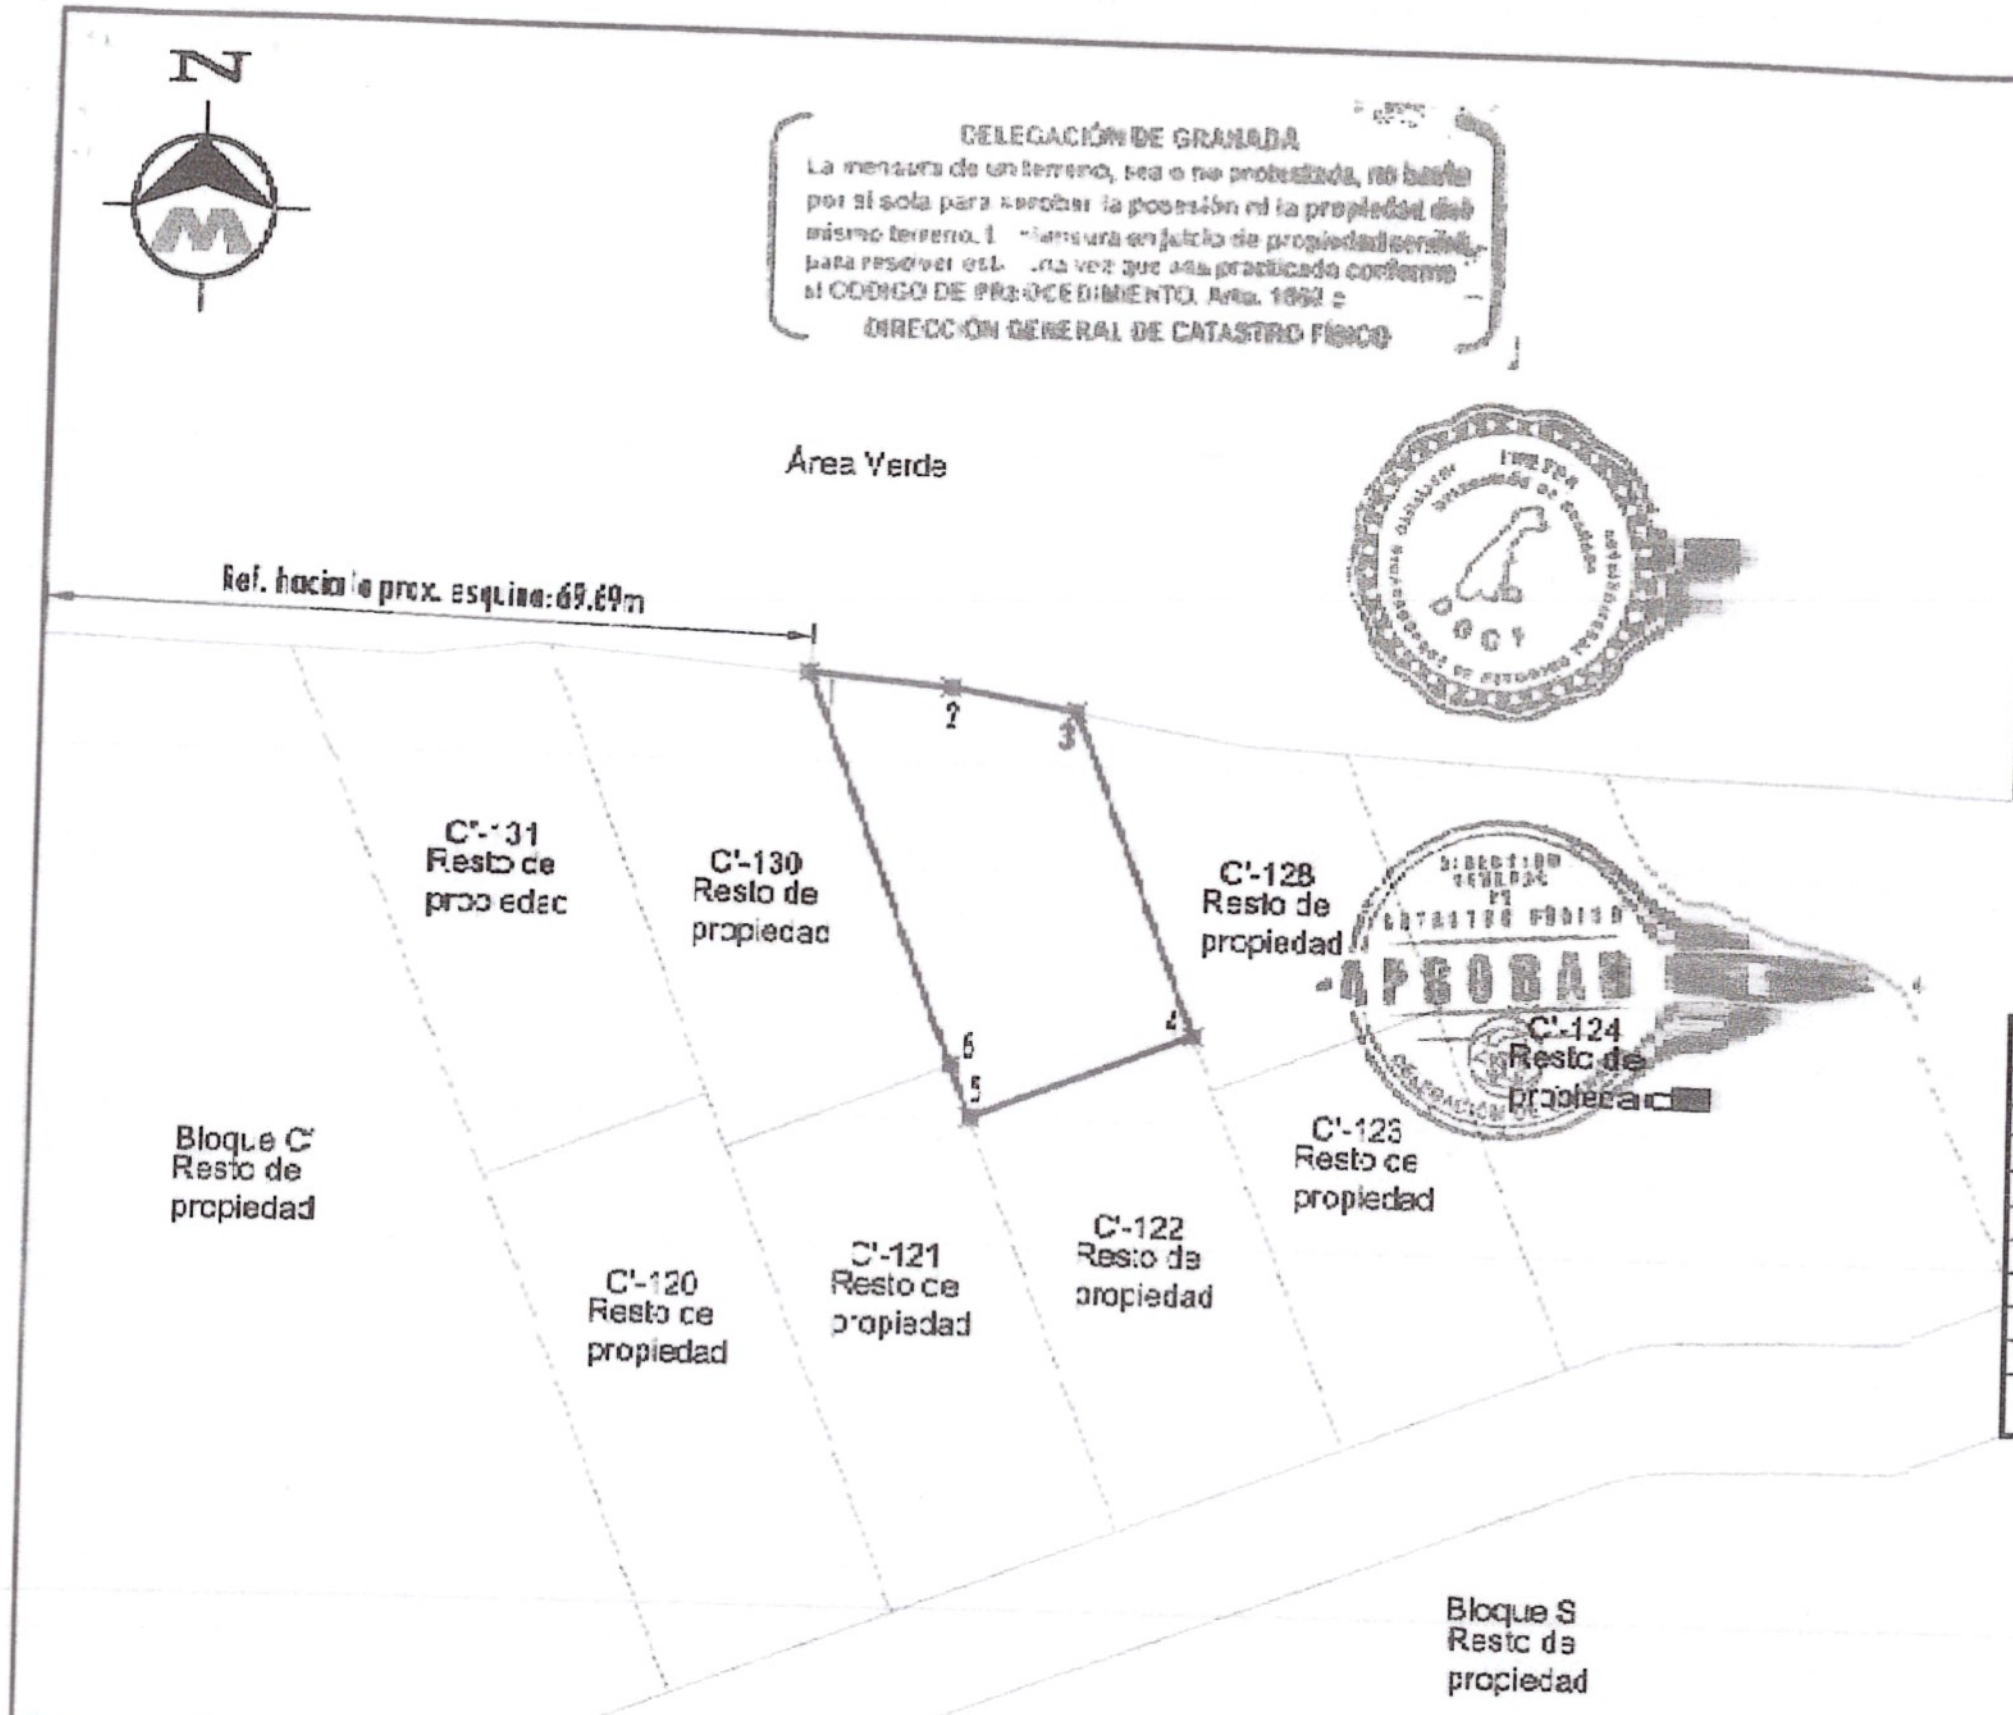

Planta de Ubicación Sin Escala
Número Catastral: 3051-4-09-000-(03903) N/C

COORDENADAS NO VINCULADAS A LA RED GEODESICA DE NICARAGUA

CUADRO DE CONSTRUCCION

LADO EST	LADO PV	RUMBO	DISTANCIA	V	COORDENADAS Y	COORDENADAS X
				1	1,317,607.8080	581215.7585
1	2	S 85°37'23.30" E	7.140	2	1,317,607.2631	581222.8778
2	3	S 80°56'31.28" E	6.459	3	1,317,606.2463	581229.2560
3	4	S 21°23'32.65" E	17.049	4	1,317,590.3720	581235.4746
4	5	S 68°36'28.30" W	11.996	5	1,317,585.9958	581224.3032
5	6	N 21°23'28.26" W	2.775	6	1,317,588.5793	581223.2912
6	1	N 21°23'32.65" W	20.651	1	1,317,607.8080	581215.7585

SUPERFICIE = 244.690 m2 = 347.07 Vrs2

MORGAN
Servicios Topograficos
Ing Bosco Javier Morgan
Lic Catastral BMM100426
Cel: 8[illegible]7566 1

Objeto Lev: Venta Parcial (Desmembración)	Número Catastral: 3051-4-09-000-(03903) N/C	FIRMA
Enajenante: Maria Auxiliadora Marenco Gutierrez Cédula: 201-260948-0001B	Ubicación: Lotificacion Bosques San Vicente lote # 12[illegible] Bloque C'. Municipio de Granada. Departamento de Gra[illegible]nada.	Ejecuta: Ing.Bosco Javier Morgan Lic. Catastral: BMM100426 Cel: 8[illegible]7566 Email: ingmorgan[illegible]23@gmail.com SERVICIOS TOPOGRAFICOS
Adquiriente: Gustavo Adolfo Rivas Ortega Cédula: 281-020375-0002P	Área: 349.879 m² = 496.27 Vrs² / Escala: 1 / [illegible]00	Fecha: 20 de Octubre del 2025

Transacción	Cudoc	Objeto Plano	Área (m²)	No. Lote
T-46FOZJ-001	0039575	DESMEMBRACIÓN	244.69	

No. Licencia: BMM100426	Parcela Objeto	Fecha Aprobación: 31/10/2025	Documento	Fecha Vencimiento: 31/10/2026
	6311371598571 6		W8BYRG7	