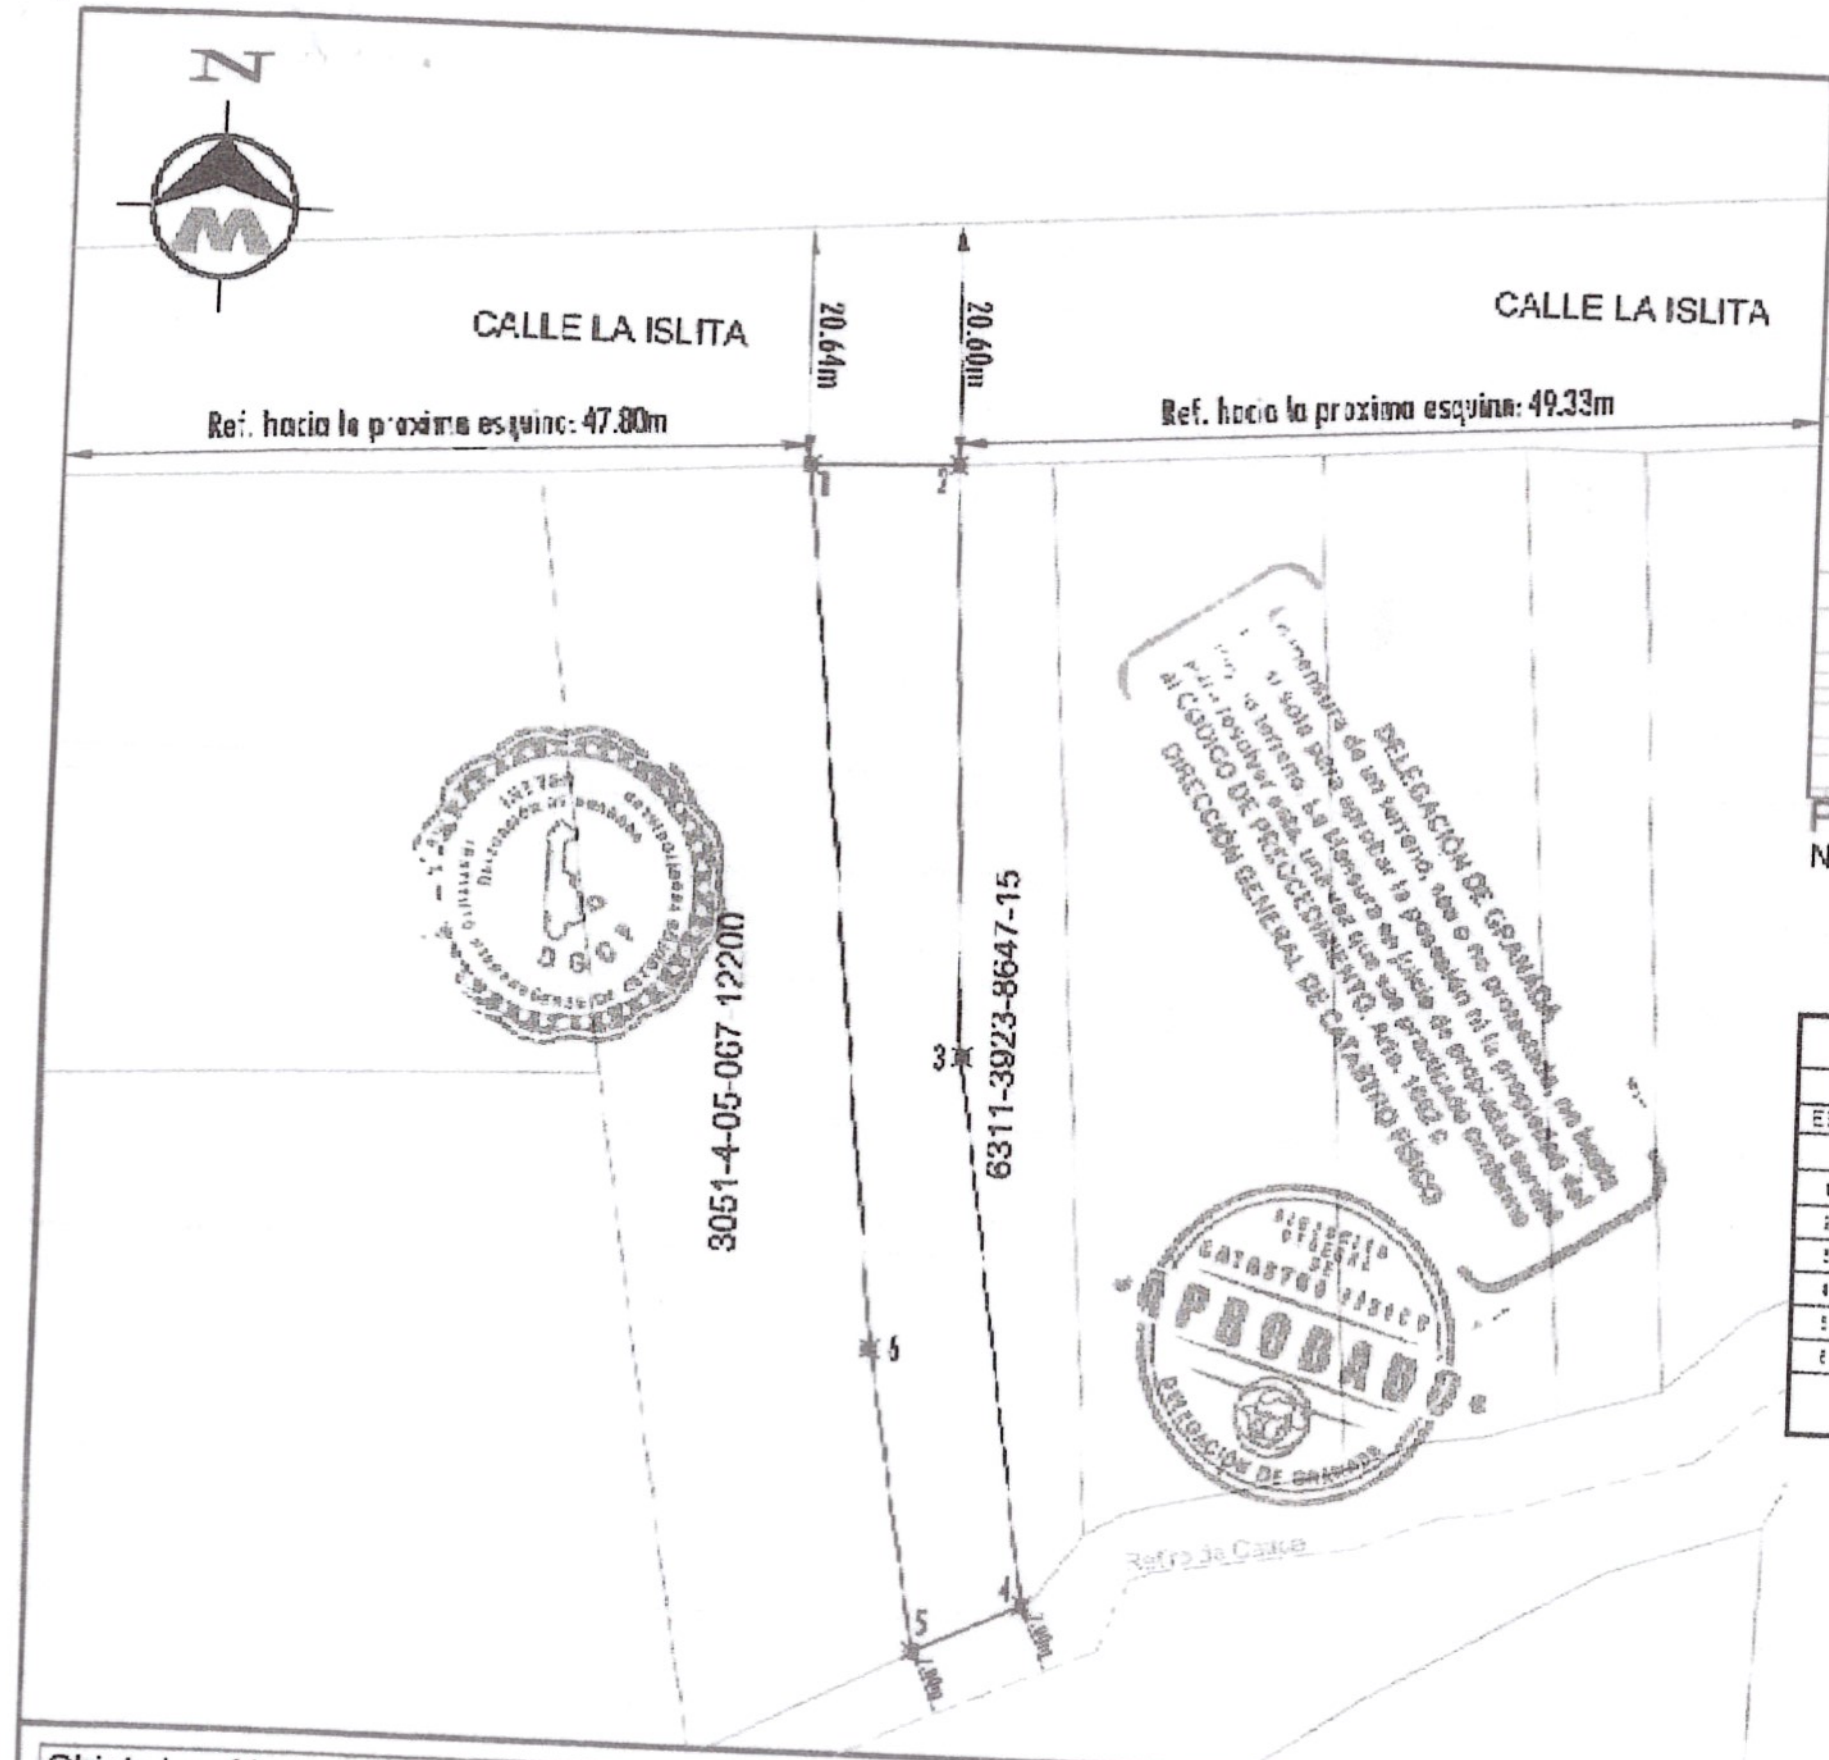

Planta de Ubicación Sin Escala
Número Catastral: 6311-3923-8606-18

COORDENADAS NO VINCULADAS A LA RED GEODESICA DE NICARAGUA

CUADRO DE CONSTRUCCION

LADO EST	LADO PV	RUMBO	DISTANCIA	V	COORDENADAS Y	COORDENADAS X
					[illegible]	[illegible]
1	2	N 88°[illegible] E	[illegible]	[illegible]	[illegible]	[illegible]
2	3	S 02°[illegible] E	[illegible]	[illegible]	[illegible]	[illegible]
3	4	S 08°[illegible] E	[illegible]	[illegible]	[illegible]	[illegible]
4	5	S 65°[illegible] W	[illegible]	[illegible]	[illegible]	[illegible]
5	6	N 09°[illegible] W	[illegible]	[illegible]	[illegible]	[illegible]
6	1	N 05°[illegible] W	[illegible]	[illegible]	[illegible]	[illegible]

SUPERFICIE = 176.89 m2 = 250.90 Vrs2

MORGAN
Servicios Topograficos
Ing Bosco Javier Morgan

Objeto Lev: Venta Total	Número Catastral: 6311-3923-8606-18	FIRMA:	
Enajenante: Yesseria del Socorro Mena Lezama Cédula: 201-231278-0003D	Ubicación: Barrio la Islita, ote 1, manzana 1. Bloque "Y". Municipio de Granada, Departamento de Granada.	Ejecuta: Ing.Bosco Javier Morgan Lic. Catastral: BMM100425 Cel: [illegible] Email: [illegible] SERVICIOS TOPOGRAFICOS	
Adquiriente: ILDAURA DELGADO LARA Ced: 408-011147-0002R	Área: 176.89 m² = 250.90 Vrs²	Escala: 1 / 350	Fecha: 10 de Octubre del 2025

Transacción T-46FCIU-001	Cudoc 0039183	Área (m²) 176.89	No. Lote
Parcela Objeto	Objeto Plano TRASPASO TOTAL	Documento 6311392386061 8	W8BXVHQ
No. Licencia: BMM100426	Fecha Aprobación: 10/11/2025		Fecha Vencimiento: 10/11/2026