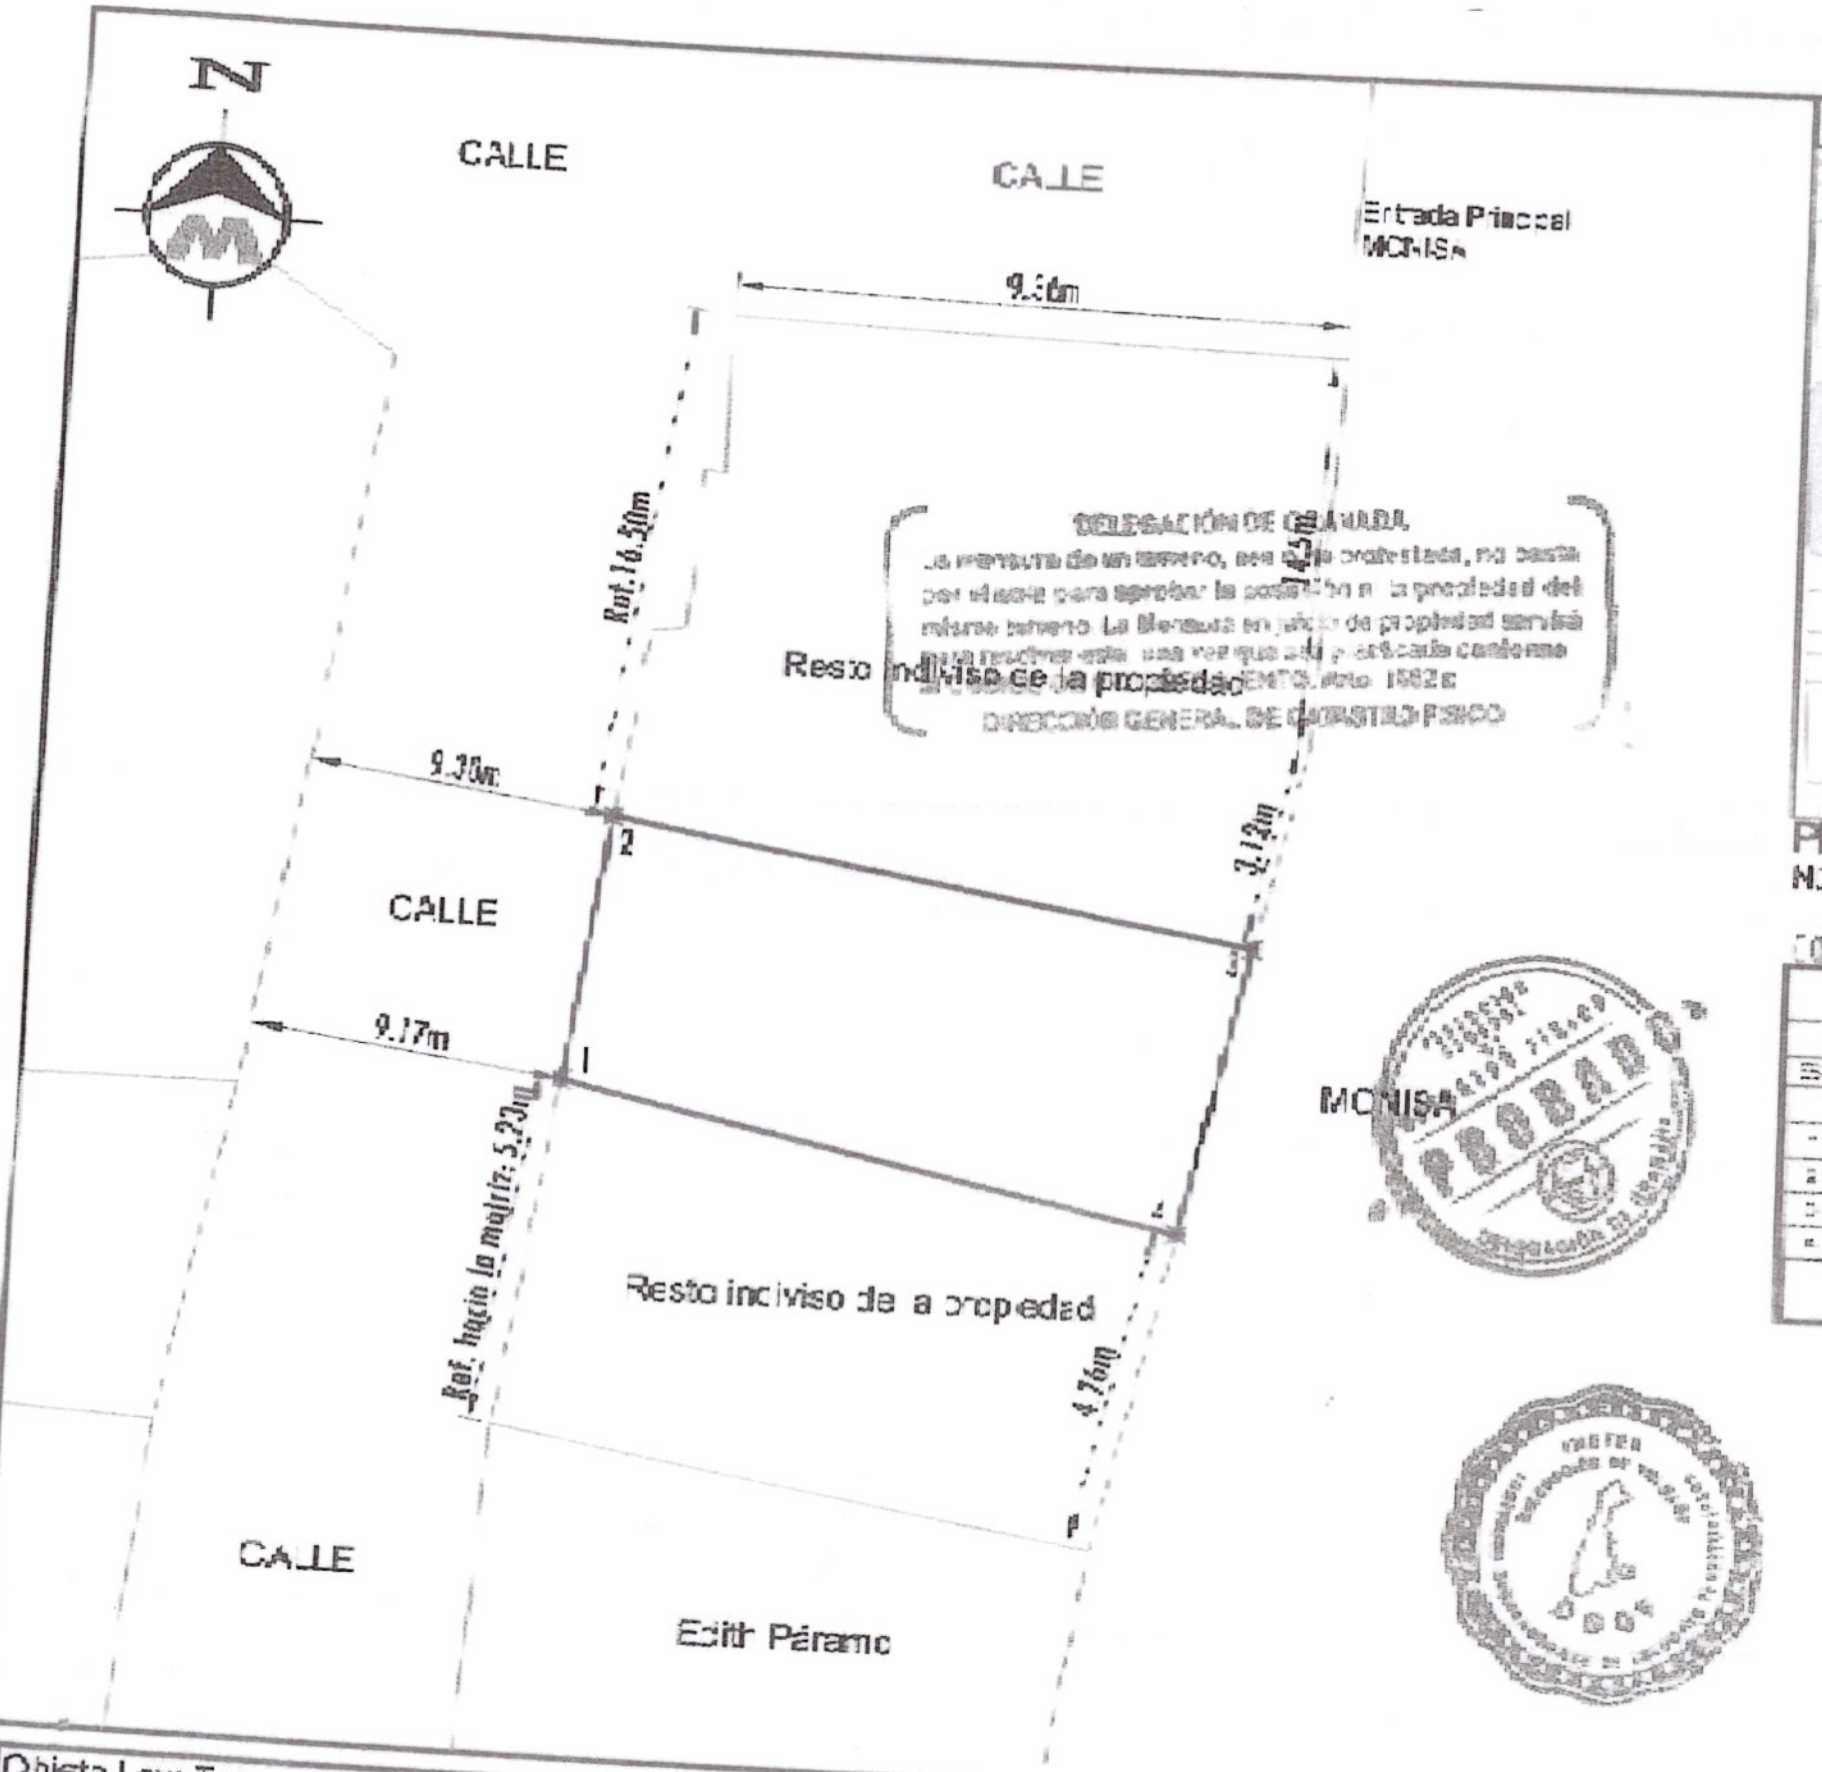

DELEGACIÓN DE GRANADA
La mención de un terreno, sea de propiedad, no basta por sí sola para acreditar la posesión de la propiedad del mismo terreno. La Mención en [illegible] de propiedad servirá para [illegible] esta una vez que [illegible] y [illegible] conforme [illegible] Arto. 1582 C
DIRECCIÓN GENERAL DE CATASTRO FÍSICO

DEPARTAMENTO DE GRANADA MUNICIPIO DE GRANADA

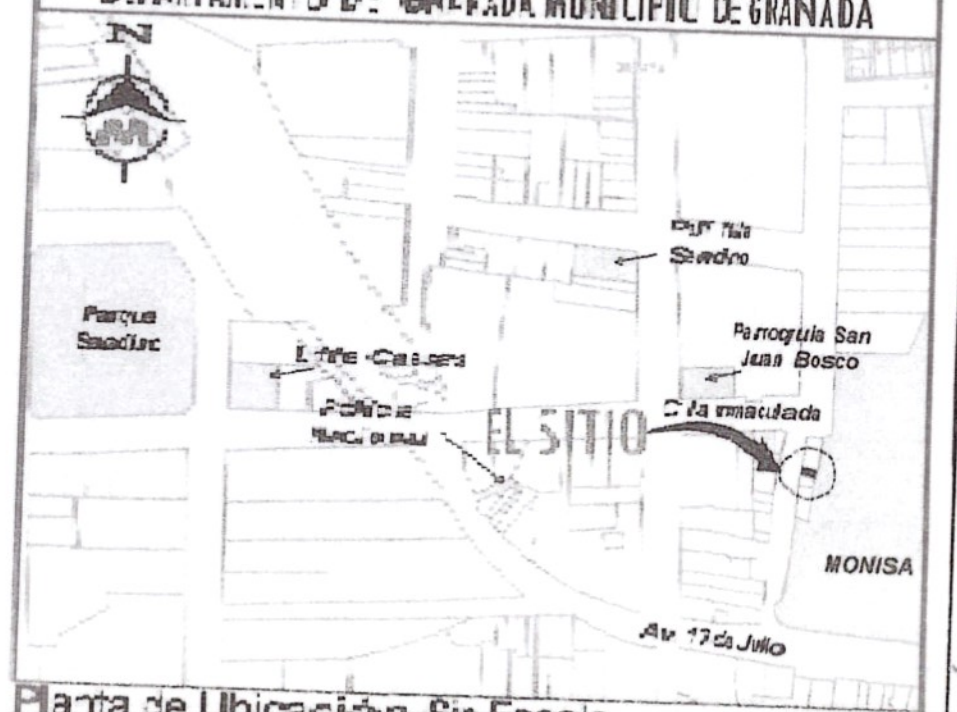

Planta de Ubicación Sin Escala
Número Catastral: 3051-4-36-058-04503

COORDENADAS NO VINCULADAS A LA RED GEODESICA DE NICARAGUA

CUADRO DE CONSTRUCCIÓN

LADO	RUMBO	DISTANCIA	V	COORDENADAS Y	COORDENADAS X
			1	1,319,758.856	614,060.3611
1 - 2	N 09°28'59.06" E	9.00	2	1,319,763.790	614,060.9431
2 - 3	S 81°09'02.57" E	9.40	3	1,319,762.275	614,070.6649
3 - 4	S 12°15'4.35" W	4.00	4	1,319,757.841	614,069.6586
4 - 1	N 79°29'58.87" W	9.73	1	1,319,758.856	614,060.3611

SUPERFICIE = 40.520 m2 = 57.47 Vrs2

MORGAN
Servicios Topograficos
Ing. Bosco Javier Morgan
Lic. Catastral BMM100426
Cel: 8883-7568

Objeto Lev: Transcripción por testamento abierto de su parte indivisa	Número Catastral 3051-4-36-058-04503	FIRMA:	SELLO
Enajenante: Luis Manuel Hernandez Bravo (q.e.p.d.) Certificado de defunción Tomo: 10018, Folio: 82	Ubicación Barrio San Juan Bosco, de la entrada principal de Monisa 9.30 m al O 16.50m al Sur Municipio de Granada Departamento de Granada.	Ejecutó: Ing. Bosco Javier Morgan Lic. Catastral: BMM100426	
Adquiriente: Javier Hernandez Ruiz Ced: 201-190069-0003F	Área: 40.520 m² = 57.47 Vrs² Factor de escala: 1.418415	Escala: 1/150	Fecha: 17 de Octubre del 2025

Transacción	Cudoc	Objeto Plano	Área (m²)	No. Lote
T-46FMBM-001	0039478	DESMEMBRACIÓN	40.52	
Parcela Objeto	631149075694 15-1		Documento	W8BYWE0
Lic. Licencia: BMM100426	Fecha Aprobación: 12/11/2025		Fecha Vencimiento: 12/11/2026	