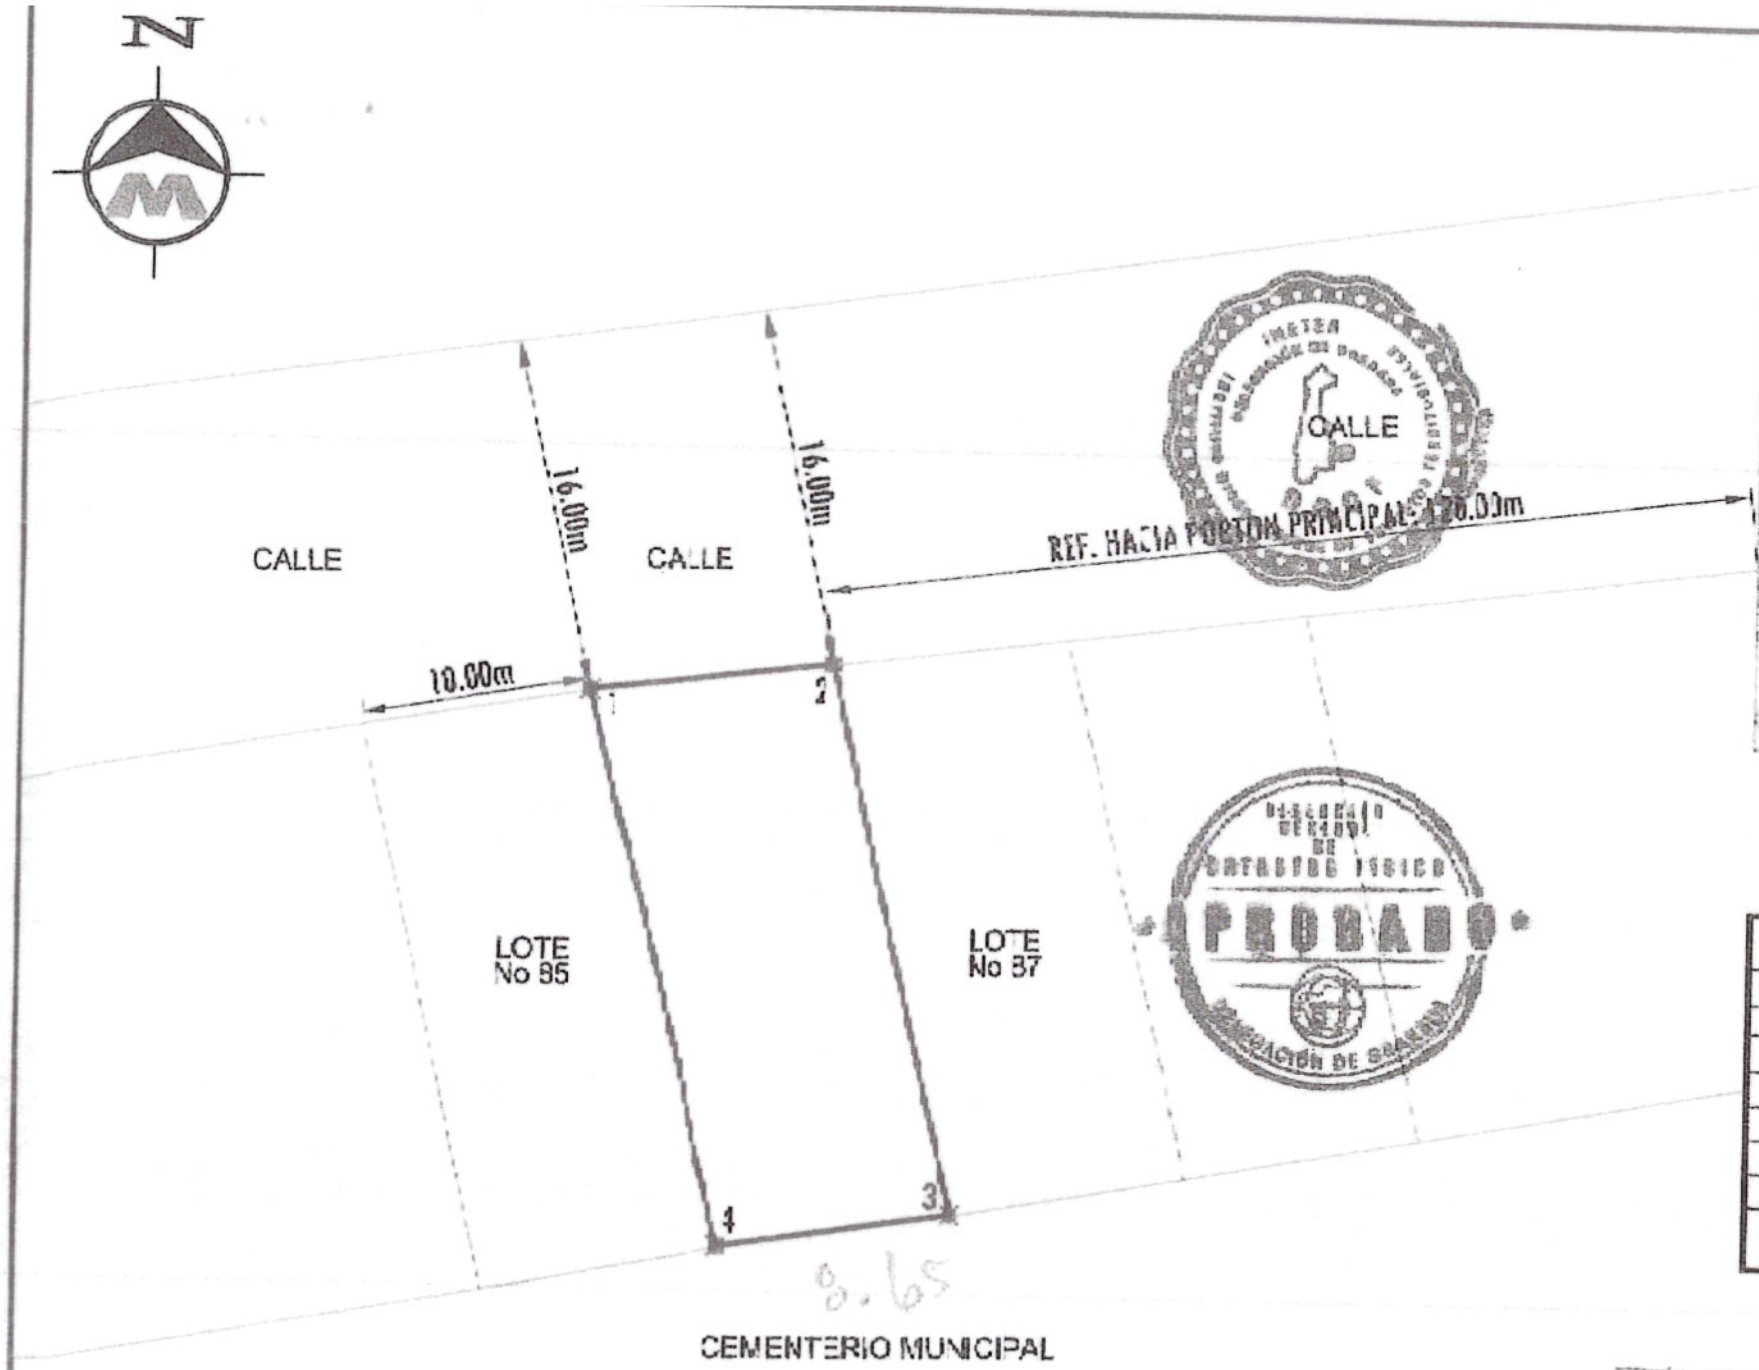

Planta de Ubicación Sin Escala
Número Catastral: 63112832143315

COORDENADAS NO VINCULADAS A LA RED GEODESICA DE NICARAGUA

CUADRO DE CONSTRUCCION

LADO EST	LADO PV	RUMBO	DISTANCIA	V	COORDENADAS Y	COORDENADAS X
				1	1,318,254.0171	612,294.9918
1	2	N 82°56'44.41" E	9.893	2	1,318,255.2321	612,304.8100
2	3	S 13°28'44.07" E	22.376	3	1,318,235.4693	612,310.0130
3	4	S 81°13'30.85" W	9.507	4	1,318,232.0190	612,300.6173
4	1	N 14°20'40.95" W	22.706	1	1,318,254.0171	612,294.9918

SUPERFICIE = 217.419 m2 = 308.39 Vrs2

DELEGACIÓN DE GRANADA
La mensura de un terreno, sea o no protestada, no basta por sí sola para aprobar la posesión ni la propiedad del mismo terreno. La Mensura en juicio de propiedad servirá para resolver esta, una vez que sea practicado conforme al CODIGO DE PROCEDIMIENTO. Arto. 1862 c
DIRECCION GENERAL DE CATASTRO FISICO

MORGAN
Servicios Topograficos
Ing. Bosco Javier Morgan
Lic Catastral BMM100426
Cel: 8883 7568 T

José Dolores Gonzalez Cruz (Menor de edad)
Representado por José Rene Gonzalez Colomer
Ced: 201-010177-0006S

Objeto Lev: Compraventa Total	Número Catastral: 63112832143315	FIRMA:
Enajenante: José Luis Dominguez Madriga Ced: 201-261155-0012N	Ubicacion: Lotificación Vistas del Sur, Lote No 86. Municipio de Granada Departamento de Granada.	Ejecuta: Ing. Bosco Javier Morgan Lic. Catastral: BMM100426 Cel: 8883-7568 E-mail: ingmorgan73@gmail.com SERVICIOS TOPOGRAFICOS
Adquiriente: José Dolores Gonzalez Cruz Certificado de nacimiento: Tomo: 297 Folio: 444 Representado por Jose Rene Gonzalez Colomer Magaly Auxiliadora Gonzalez Cruz Ced: 201-260301-1000D	Área: 217.42 m² = 308.39 Vrs² Escala: 1 / 500	Fecha 14 de Octubre del 2025

Transacción	Cudoc	Objeto Plano	Área (m²)	No. Lote
T-46FIKF-001	0039336	TRASPASO TOTAL	217.42	
Parcela Objeto		63112832143315	Documento	WBBYOUG
No. Licencia: BMM100426	Fecha Aprobación: 30/10/2025		Fecha Vencimiento: 30/10/2026 11:44:26	