COORDENADAS NO VINCULADAS A LA RED GEODESICA DE NICARAGUA

CUADRO DE CONSTRUCCION LOTE "A"

LADO EST	LADO PV	RUMBO	DISTANCIA	V	COORDENADAS Y	COORDENADAS X
				1	1,346,594.8700	625,265.6900
1	2	S 26°15'45.00" E	4.495	2	1,346,590.8100	625,265.6500
2	3	S 36°35'41.84" E	5.723	3	1,346,583.0700	625,271.5200
3	4	S 29°29'28.88" E	14.544	4	1,346,570.4100	625,278.6500
4	5	S 24°02'46.28" E	34.837	5	1,346,536.7700	625,285.6900
5	6	S 25°14'10.51" E	74.364	6	1,346,566.5300	625,322.9900
6	7	S 82°13'41.66" W	130.103	7	1,346,550.9100	625,198.6500
7	8	S 81°50'01.15" W	94.612	8	1,346,537.5300	625,103.4200
8	9	N 07°54'46.38" W	125.571	9	1,346,561.3800	625,085.2300
9	10	N 72°17'40.22" E	10.428	10	1,346,564.5300	625,095.2400
10	11	S 65°30'26.47" E	34.996	11	1,346,548.9500	625,127.5600
11	12	N 77°54'11.39" E	38.625	12	1,346,556.7300	625,165.3300
12	1	N 67°22'28.58" E	108.302		1,346,594.8700	625,265.6900

SUPERFICIE = 24,666.597 m2 = 34,988.04 Vrs2

COORDENADAS NO VINCULADAS A LA RED GEODESICA DE NICARAGUA

CUADRO DE CONSTRUCCION LOTE "B"

LADO EST	LADO PV	RUMBO	DISTANCIA	V	COORDENADAS Y	COORDENADAS X
				13	1,346,569.2700	625,331.4540
13	14	N 85°11'34.02" W	78.033	14	1,346,537.1656	625,299.5152
14	15	N 26°35'44.27" W	65.400	15	1,346,595.8739	625,270.6963
15	16	N 17°20'58.18" W	1.525	16	1,346,597.3330	625,270.2400
16	17	N 81°30'00.09" E	720.242	17	1,346,603.7583	625,982.5713
17	18	S 07°01'02.89" E	142.091	18	1,346,457.8015	626,000.5629
18	19	S 82°25'05.33" W	549.309	19	1,346,566.6080	625,460.2940
19	13	S 82°20'08.70" W	133.061	13	1,346,569.2700	625,331.4540

SUPERFICIE = 98,383.130 m2 = 139,548.11 Vrs2

DEPARTAMENTO DE GRANADA MUNICIPIO DE GRANADA

Planta de Ubicación Sin Escala
Número Catastral: 63245616553214 Lote "A"
63245667335311 Lote "B"

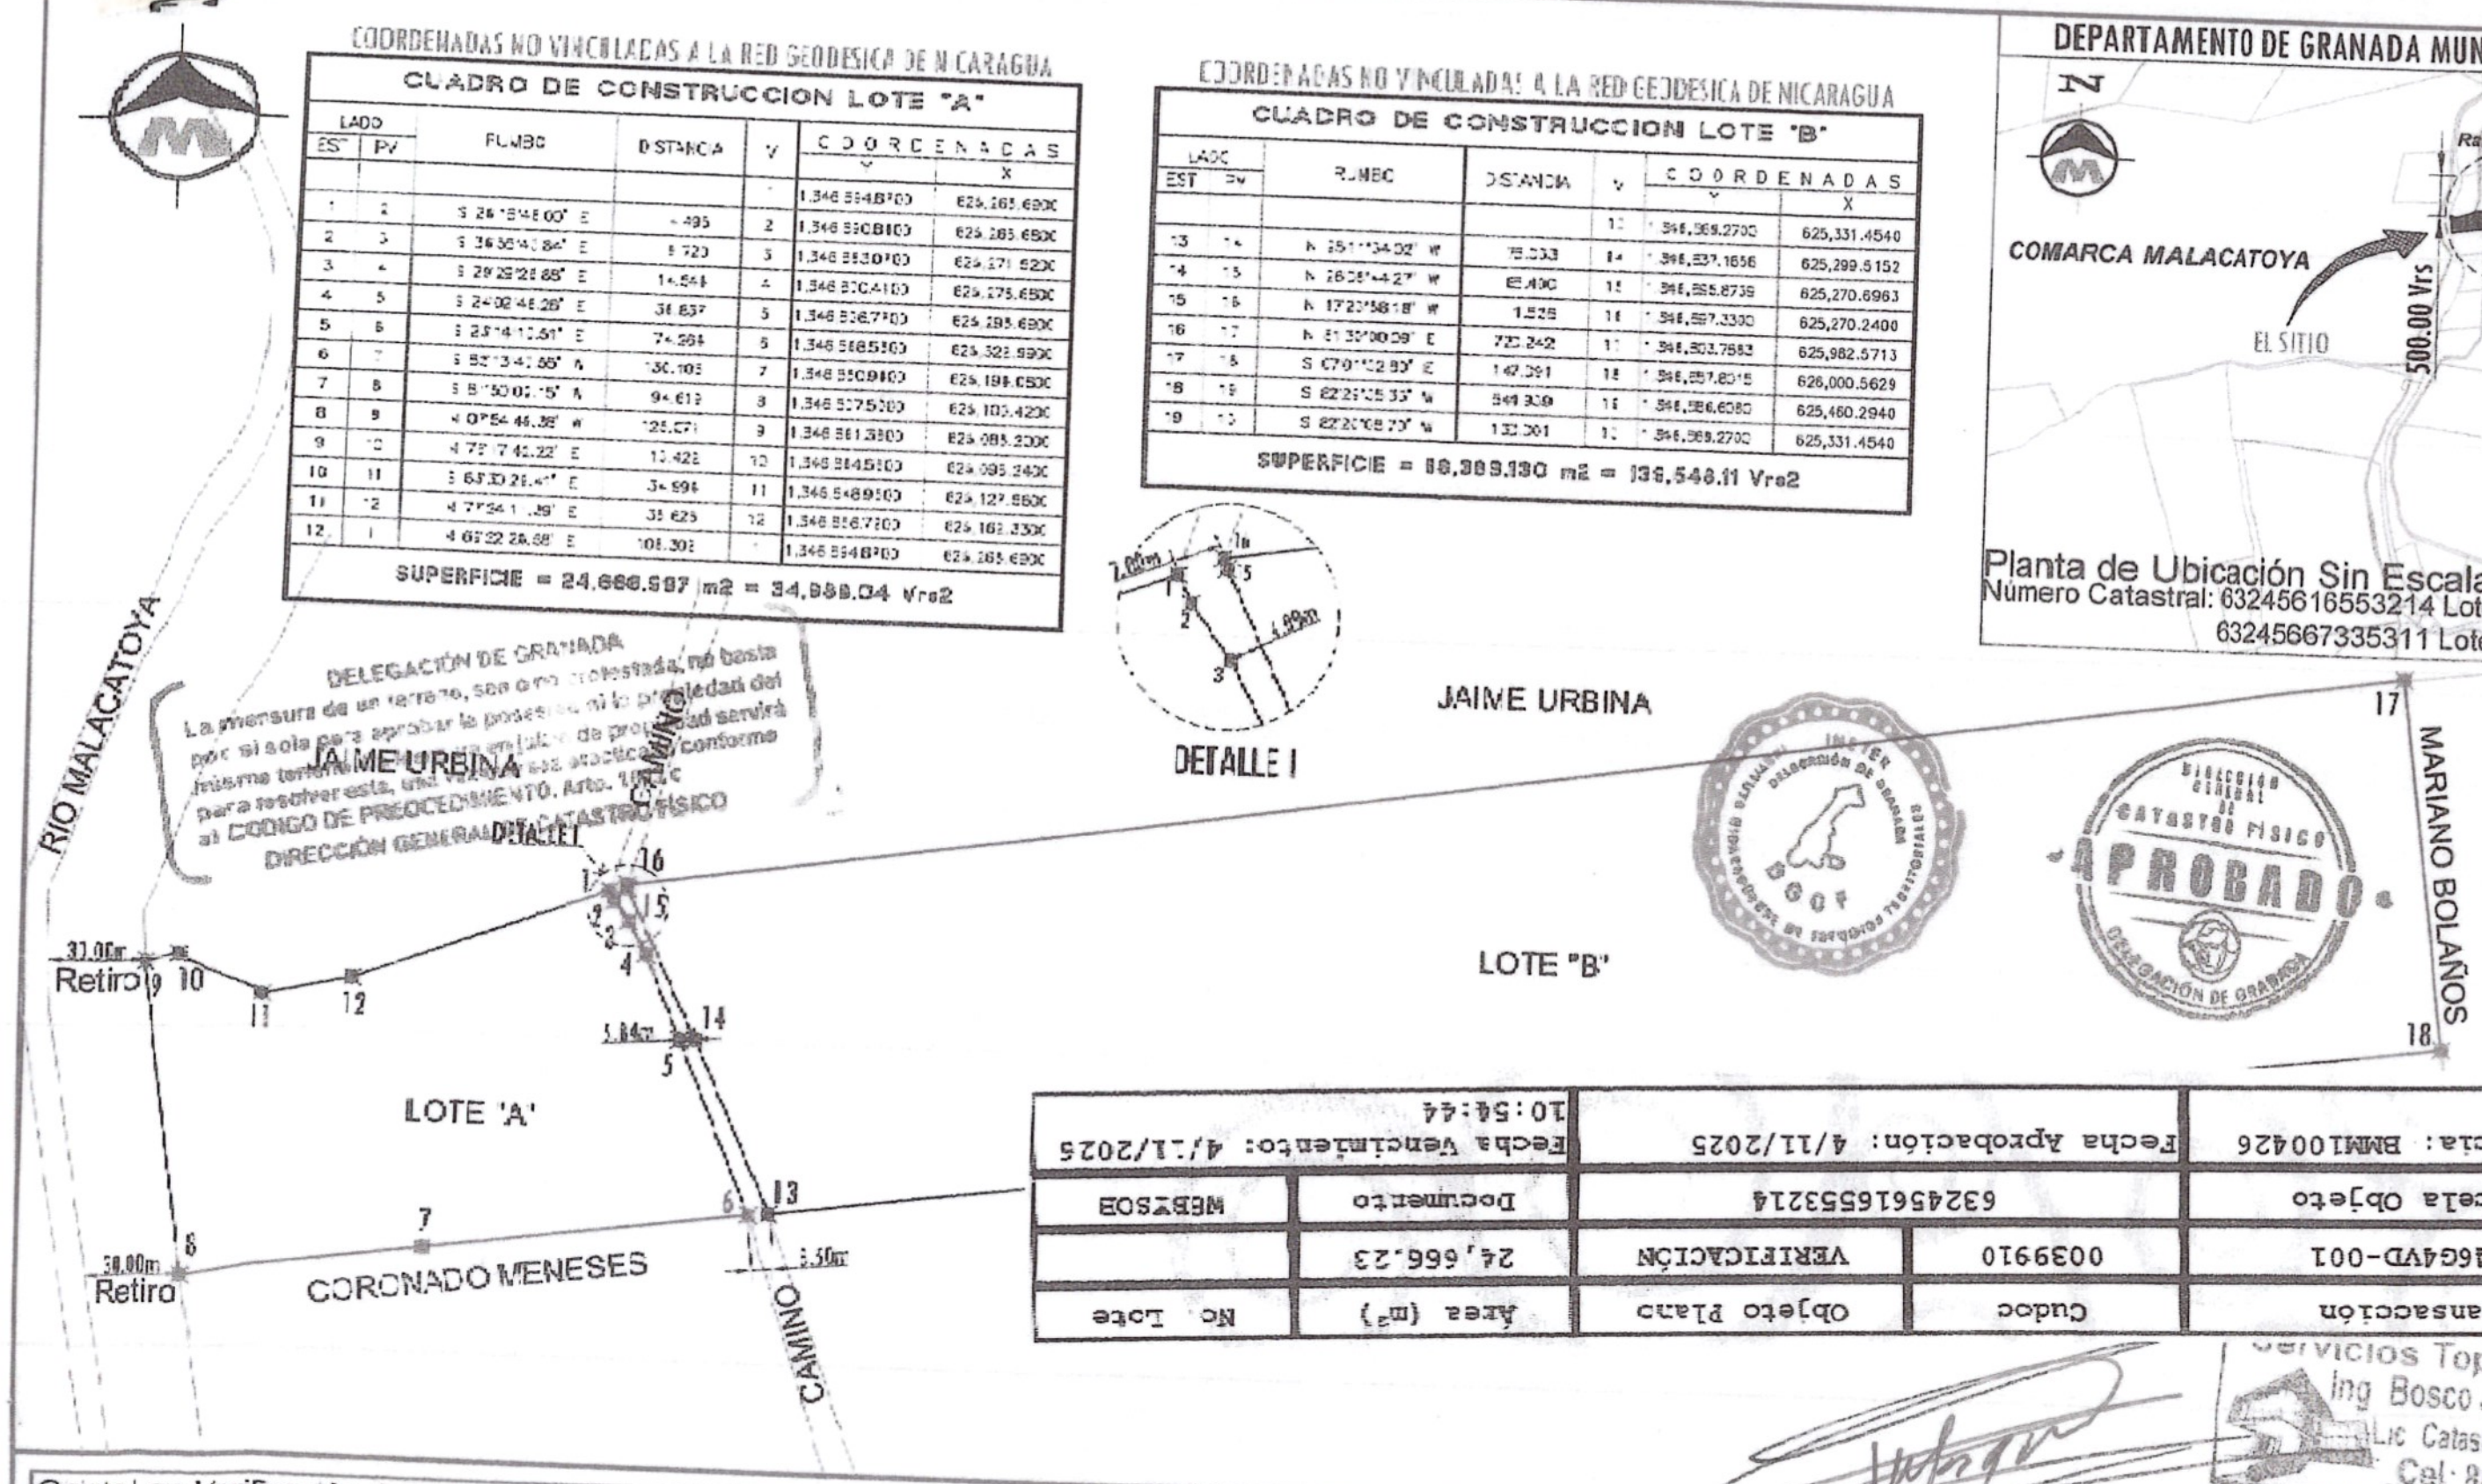

Transaccion	Cudoc	Objeto plano	Area (m²)	No. Lote
T-46G4VD-001	0039910	VERIFICACIÓN	24,666.23	
Parcela Objeto	63245616553214		Documento	WEBYSOS
No. Licencia: BMM100426	Fecha Aprobación: 4/11/2025		Fecha Vencimiento: 4/11/2025 10:54:44	

T-46G4WO-001	0039909	VERIFICACIÓN	98,383.13
Parcela Objeto	63245667335311		Documento
No. Licencia: BMM100426	Fecha Aprobación: 4/11/2025		Fecha Vencimiento: 4/11/2026 10:54:05

Servicios Topograficos
Ing Bosco Javier Morgan
Lic Catastral: BMM19042
Cel: 8883 7568 T

Objeto Lev: Verificación de area	Número Catastral: 63245616553214 Lote "A" 63245667335311 Lote "B"	FIRMA:
Propietario: Jose Gustavo Herrera Pasaporte: 491282636	Ubicación: Comca Malacatoya de Rancho Irene 500 Vrs al S. Municipio de Granada, Departamento de Granada.	Ejecuta: Ing Bosco Javier Morgan Lic. Catastral: BMM100426 Cel: 8883-7568 Email: ingmorgan73@gmail.com SERVICIOS TOPOGRAFICOS
Factor de escala: 1.418415	Área Lote "A": 24,666.99 m2 = 34,988.04 Vrs2 Área Lote "B": 98,383.13 m2 = 139,548.11 Vrs2	Escala: 1 / 3,500
		Fecha: 29 de Octubre del 2025